

CASULO SENSORIAL

ZC-ARQ-002 · REV 00 — CONCEITO (VARIANTE) · 18/09/2026

A mesma concha, os mesmos arcos, o mesmo Bico e o mesmo banho do Casulo. Muda o que se vê e onde se dorme: um cinturão transparente nos vãos da suíte, com cortina, que abre por zíper; uma cama com dossel e véu no meio dele, olhando a fachada de vidro e o Bico; um lounge de chão sob o Bico; a mini cozinha em L atrás, junto ao banho. Duas coleções de mobiliário: Zion New Luxury e Boho / Bali.

9,4 m²

DE CINTURÃO TRANSPARENTE

4

PAINÉIS DE CRISTAL T3/T4

0

ARCOS ALTERADOS

47

ITENS FF&E BALI

Variante conceitual: não substitui o Casulo (ZC-ARQ-001 / ZG-TEC-001); reaproveita 100 % da estrutura, da fundação e do banho. Onde depende de cálculo ou norma,

 VALIDAÇÃO OBRIGATÓRIA — ENGENHEIRO/ARQUITETO. Sem preços: **PREÇO A COTAR**.

O QUE MUDA E POR QUÊ

sensorial com a natureza: ver, ouvir, sentir o ar; privacidade em camadas

OS QUATRO MOVIMENTOS

#	MOVIMENTO	COMO
1	Cinturão transparente	vãos A2-A3 e A3-A4 (x 2,85 a 5,25), dos dois lados, do trilho de base a z 1,85; a lona vira PVC cristal (ou ETFE), soldada por HF na linha da terça T5; zíper #10 na base abre a parede inteira
2	Cama olhando a paisagem	king com dossel de teca a 2,40 m e véu de voile nas 4 faces (também mosquitoeiro), sobre tablado de 0,15 m, no meio do cinturão; pés para o vidro e o Bico; sem cabeceira na parede
3	Lounge de chão sob o Bico	futons, almofadas em kilim, mesa baixa de tronco, cadeira suspensa de rattan: leve, para sentar no chão e olhar a mata
4	Cozinha atrás, junto ao banho	mini cozinha em L (1,35 m na concha + 0,65 m na parede do banho): geladeira, forno + cooktop de indução, cuba, air fryer; closet de 1,10 m do lado direito da mesma parede: água, esgoto e energia na mesma parede molhada

AS TRÊS CAMADAS DA LATERAL

CAMADA	MATERIAL	FUNÇÃO
1 · Cristal	PVC cristal 0,7 mm (M2) ou ETFE 250 µm em 2 folhas (melhor no frio); keder Ø10 nos arcos, zíper na base	vista, chuva, vento; abre nos dias bons
2 · Tela	tela mosquitoiera poliéster 18 x 16 fios no trilho de harpão	abrir a parede sem entrar bicho
3 · Cortina	voile de linho com barra de macramê + blackout motorizado em trilho curvo de alumínio a 0,12 m do forro	privacidade e luz em camadas; blackout à noite e no inverno

O QUE NÃO MUDA

Concha, arcos A0 a A7, Bico, Espinha de Luz, fachada de vidro, banho na cauda, fundação, grelha, deck

Lotes 1 e 2 idênticos ao Casulo (mesma estrutura metálica e mesma infraestrutura)

Lote 3: 4 painéis de lona viram cristal (T3D/E, T4D/E); os demais são iguais

Lote 4: nova coleção de mobiliário (Bali) ou a atual (New Luxury), sobre a mesma marcenaria acoplada

NÚMEROS

	CASULO	SENSORIAL
Membrana opaca (m2)	102,6	94,7
Vidro + cristal na concha (m2)	6,0	13,8
Cinturão transparente (m2)	—	9,4
Janelas Olho	6	3 (as 3 da suite viram cinturão)
Cama	x 4,50 a 6,55, cabeceira no banho	x 2,60 a 4,65, dossel, pés para o vidro
Cozinha	x 1,20 a 3,20 (estar)	x 5,25 a 6,60 em L (junto ao banho)
Closet	x 3,40 a 4,50	x 5,40 a 6,50 (dir.)

ATENÇÃO

Sem isolamento nas laterais do cinturão: carga térmica de inverno maior (climatização 12k → 18k BTU a confirmar), risco de condensação no cristal em noites frias (ETFE duplo reduz), e o blackout cumpre a privacidade à noite.

⚠️ VALIDAÇÃO OBRIGATÓRIA — ENGENHEIRO/ARQUITETO

 para o balanço térmico e para a fixação do dossel (peso próprio + cadeira suspensa no arco A1).


ZION CASULO SENSORIAL · PLANTA DE LAYOUT

Variante: cinturão transparente nos vãos A2-A4 · cama com dossel olhando a fachada e o Bico · lounge de chão · mini cozinha em L junto ao banho · 1:50



Cinturão transparente T3/T4: cristal com zíper, tela mosquiteira + cortina de voile e blackout em trilho curvo

Mini cozinha em L (1,35 + 0,65 m): geladeira, forno + cooktop de indução, cuba, air fryer

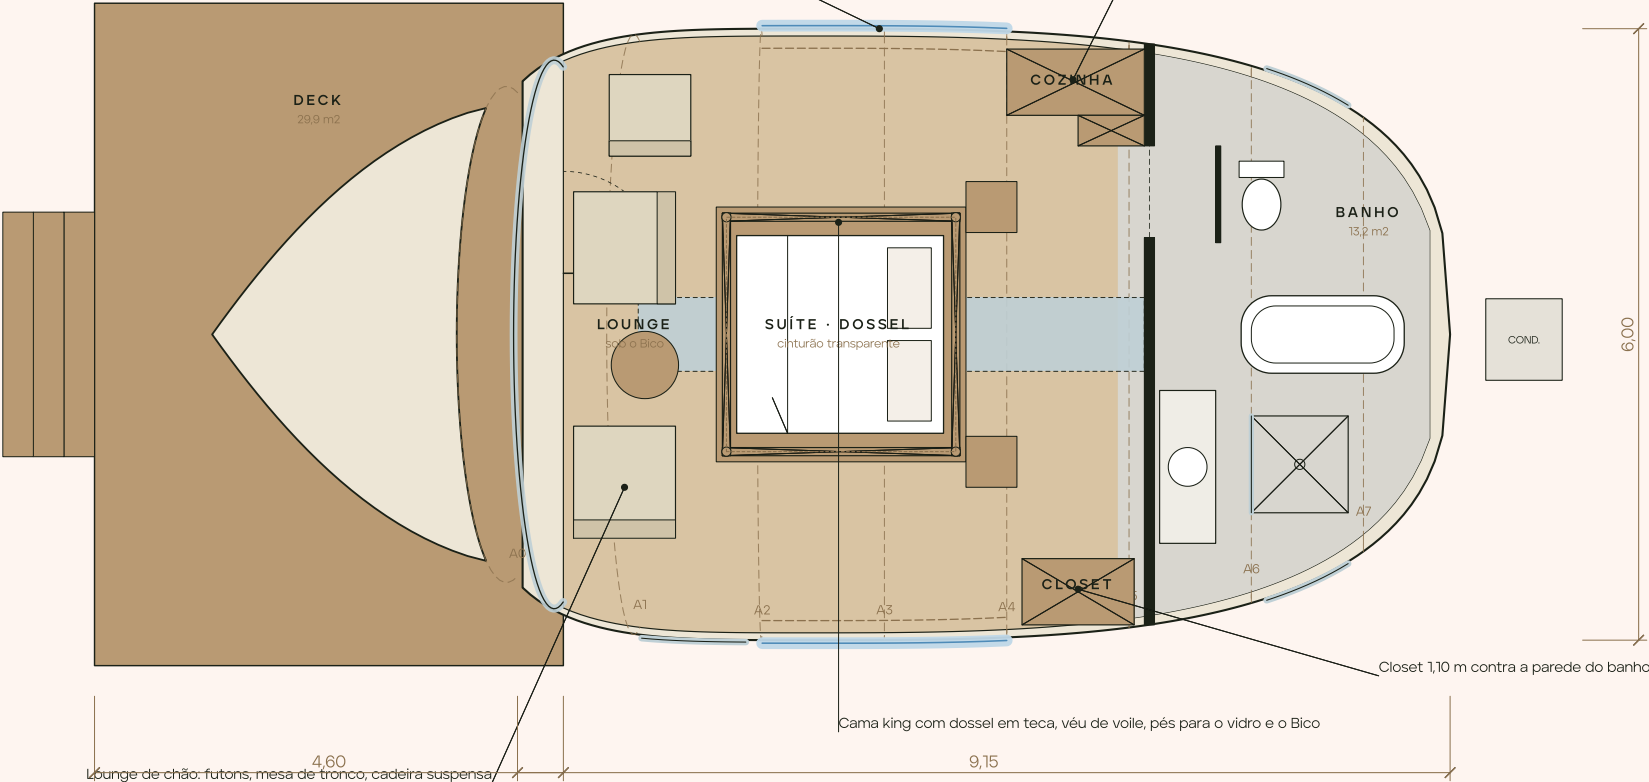


Lounge de chão: futons, mesa de tronco, cadeira suspensa

Cama king com dossel em teca, véu de voile, pés para o vidro e o Bico



Closet 1,10 m contra a parede do banho

 ZION HOTEL GROUP INTERNATIONAL	PLANTA DE LAYOUT · VARIANTE	
	Cinturão transparente A2-A4 · dossel · cozinha em L atrás · closet	
ZION CASULO SENSORIAL ZION GLAMPING COLLECTION	ESCALA 1:50 (A1) · cotas em metros	FOLHA VS-01
	PROJETO CONCEITUAL · ESTUDO PRELIMINAR	SET 2026

ZION CASULO · ELEVACÃO LATERAL DIREITA
Vista do lado das Janelas Olho (olhar para +y) · comprimento 12,15 m com o Bico · deck 4,60 m

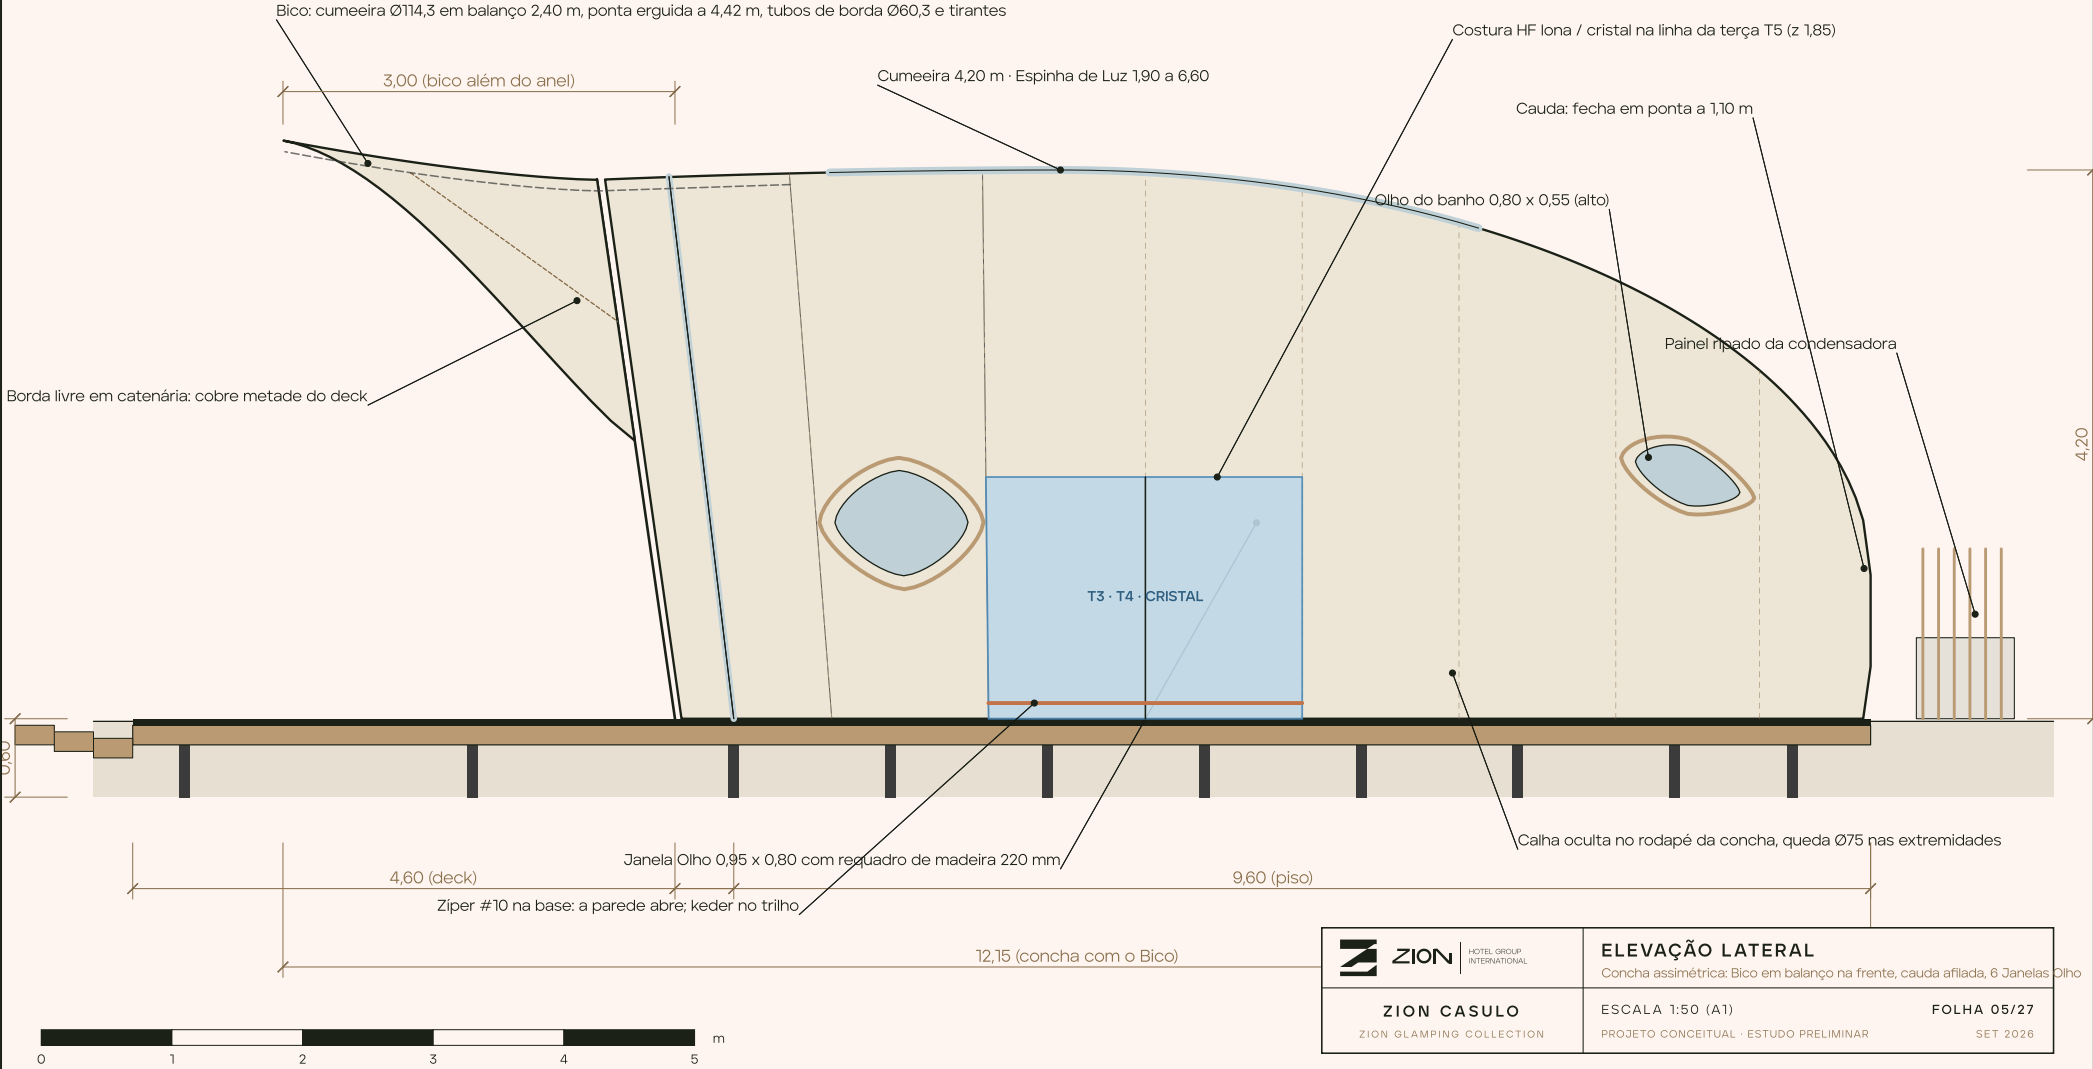

ZION CASULO SENSORIAL · CORTE TRANSVERSAL PELO CINTURÃO
Plano x = 3,8 (suíte) · olhar para +x · as três camadas da lateral: cristal, tela, cortina · dossel · 1:40

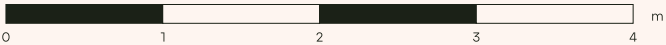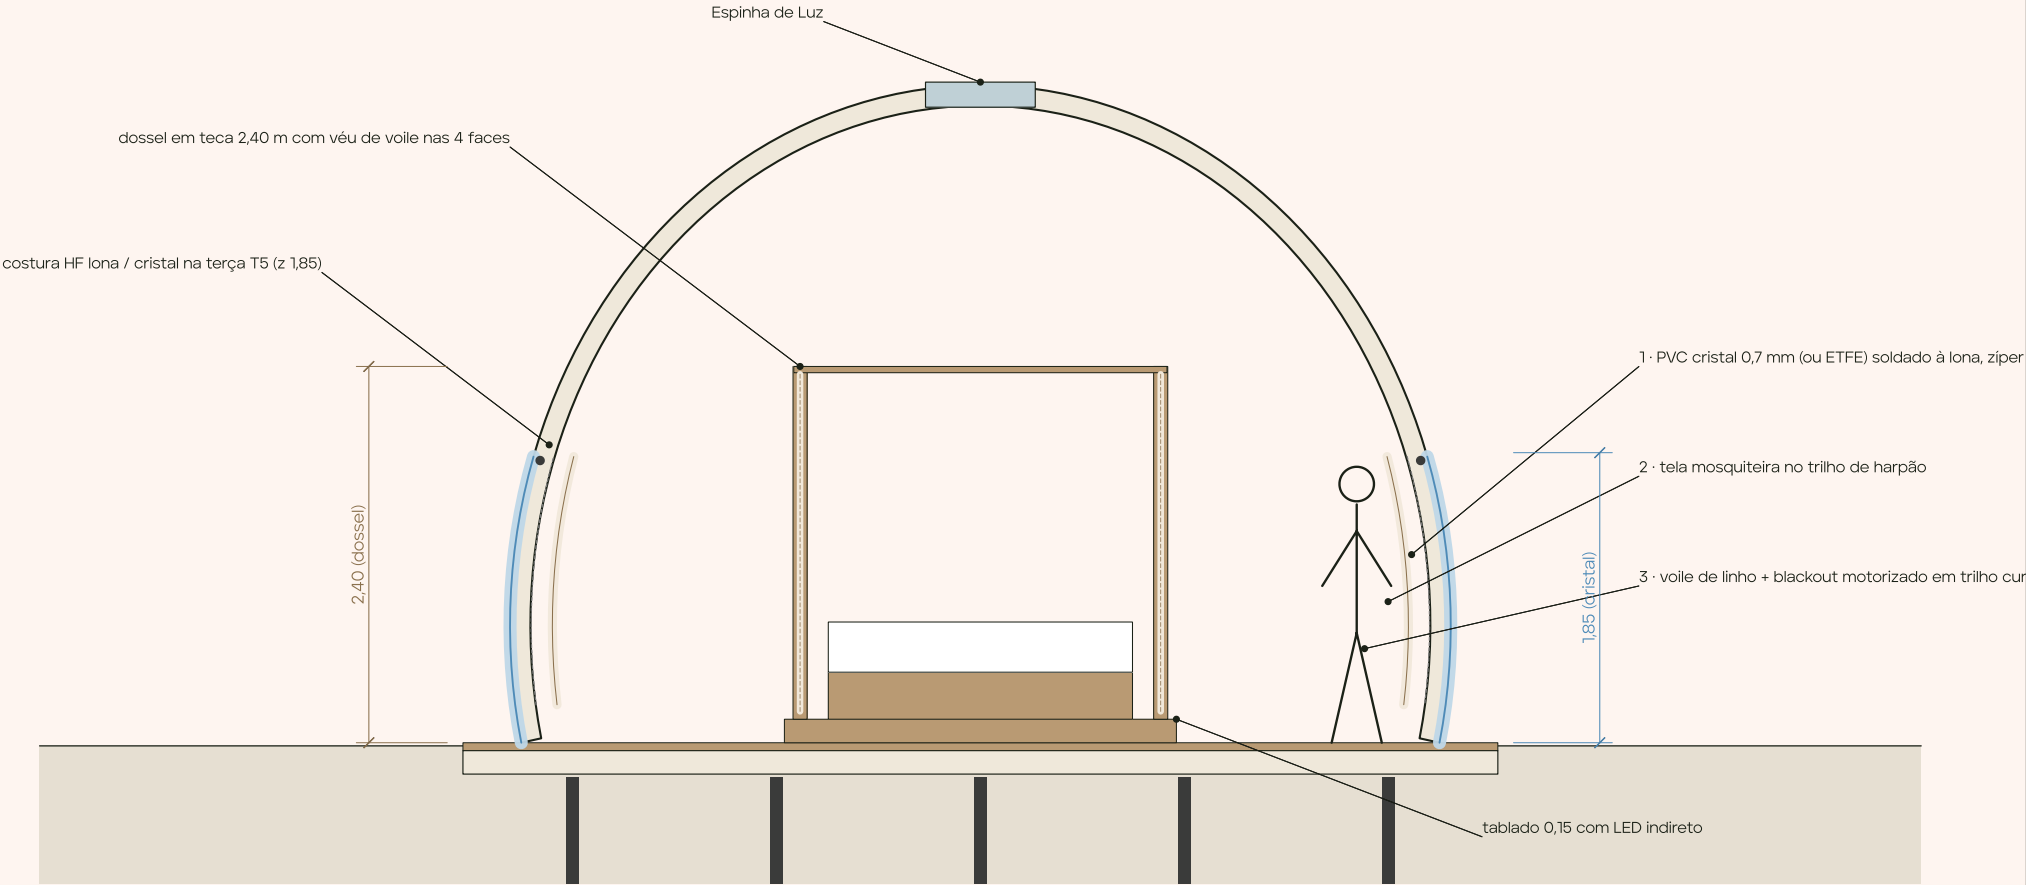

ZION HOTEL GROUP INTERNATIONAL ZION CASULO SENSORIAL ZION GLAMPING COLLECTION	CORTE TRANSVERSAL PELO CINTURÃO Três camadas: cristal com zipper, tela, cortina de voile + blackout	
	ESCALA 1:40 (A1) PROJETO CONCEITUAL · ESTUDO PRELIMINAR	FOLHA VS-03 SET 2026

ZION CASULO · VISTA ISOMÉTRICA
Projeção isométrica a partir da frente e da lateral direita · sem escala



- ① Concha em membrana PVDF tensionada sobre 8 arcos elípticos
- ② Bico: membrana em balanço 2,40 m sobre o deck, ponta erguida a 4,42 m
- ③ Espinha de Luz na cumeeira (4,70 m)
- ④ 6 Janelas Olho em lente com requadro de madeira
- ⑤ Deck frontal 4,60 x 6,50 m em cumaru
- ⑥ Cauda afilada com a banheira e a condensadora oculta

 ZION HOTEL GROUP INTERNATIONAL	VISTA ISOMÉTRICA Volumetria do casulo com deck e fachada panorâmica	
	ZION CASULO ZION GLAMPING COLLECTION	FOLHA 08/27 ESCALA sem escala PROJETO CONCEITUAL · ESTUDO PRELIMINAR SET 2026

RENDERS EXTERIOR · CASULO E CASULO SENSORIAL LADO A LADO

modelo 3D da variante (cocoon_s/3d) · mesma câmera nas duas versões


EXTERIOR FRONTAL · CASULO




EXTERIOR FRONTAL · SENSORIAL



EXTERIOR LATERAL · CASULO

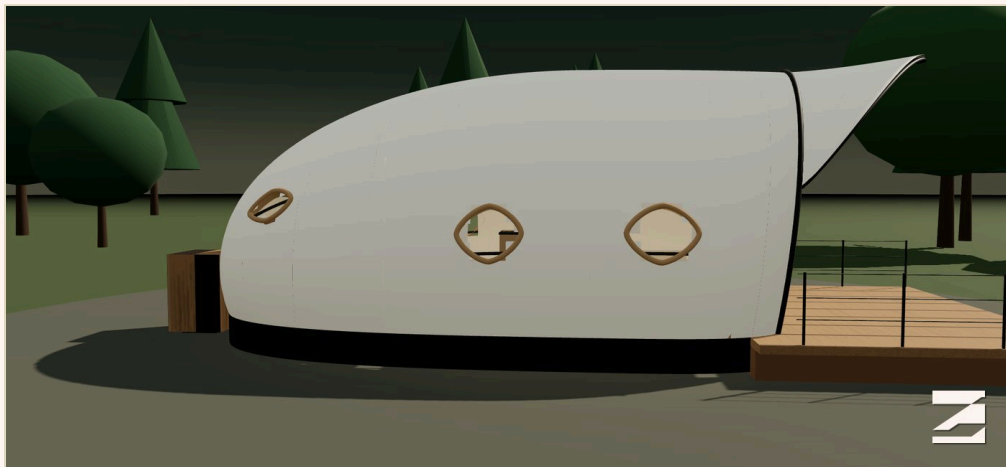

EXTERIOR LATERAL · SENSORIAL

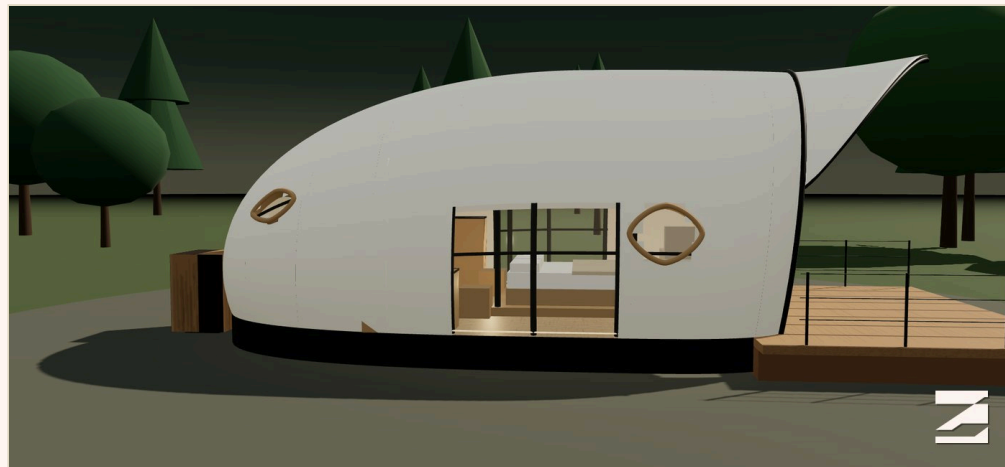

RENDERS INTERIOR · CASULO E CASULO SENSORIAL LADO A LADO

modelo 3D da variante (cocoon_s/3d) · mesma câmera nas duas versões


INTERIOR · SUÍTE · CASULO



INTERIOR · SUÍTE · SENSORIAL



INTERIOR · ESTAR / LOUNGE · CASULO

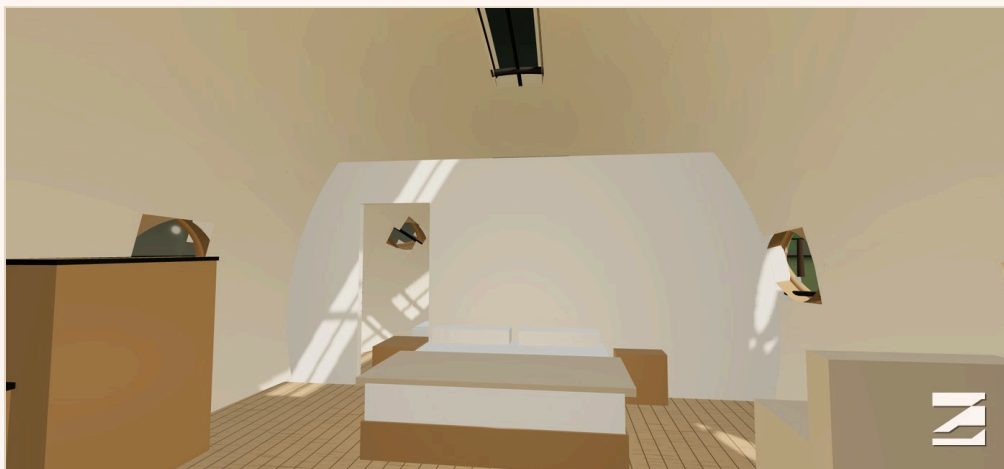

INTERIOR · ESTAR / LOUNGE · SENSORIAL



LONA · O QUE MUDA NO LOTE 3

2 padrões de cristal (T) substituem a parte baixa dos painéis P3 e P4 · costura HF lona / cristal na terça T5 · zíper na base · mapa e padrões em cocoon_s/lona/

CÓD.	QTD	CAIXA (M)	M2	MATERIAL
T3D	2	1,24 x 1,87	2,26	PVC cristal 0,7 mm (ou ETFE 250 µm em 2 folhas) soldado por HF à lona; keder Ø10 nas laterais; zíper na base
P3D	2	1,27 x 3,64	4,50	PVDF tipo II 1050 g/m2 (poliéster de alta tenacidade, PVC + laca PVDF), cor creme Zion, tratamento anti-fungo,
T4D	2	1,38 x 1,94	2,24	PVC cristal 0,7 mm (ou ETFE 250 µm em 2 folhas) soldado por HF à lona; keder Ø10 nas laterais; zíper na base
P4D	2	1,43 x 3,60	4,30	PVDF tipo II 1050 g/m2 (poliéster de alta tenacidade, PVC + laca PVDF), cor creme Zion, tratamento anti-fungo,

Os demais painéis (P0 a P2, P5 a P8, forros F1 a F8) são os mesmos do Casulo. O confeccionista solda o cristal à lona em fábrica; o painel chega como uma peça só por lado e vão, com o zíper e os keders prontos.



ZION CASULO SENSORIAL · MAPA DOS PAINÉIS DE LONA E REVESTIMENTO

11 padrões externos · 8 padrões internos · costuras sobre a estrutura · códigos usados nas pranchas LN e no DXF

TIPOS DE BORDA (ver LN-90)

-  KEDER Ø10 - desliza no perfil duplo keder do arco / caibro
-  KEDER Ø13 - perfil de arremate de base com calha (trilho 100 x 50)
-  CLAMP - barra de alumínio 40 x 6 parafusada (M8 @150) sobre EPDM
-  ZIPER - ziper YKK #10 duplo na base do cristal (parede que abre) + keder Ø13 no trilho
-  SOLDA HF LONA-CRISTAL - emenda de 40 mm entre a lona opaca e o PVC cristal (linha da terça)
-  BOLSA - lona envolve o tubo de borda (Ø60,3) e fecha com fita keder
-  BORDA LIVRE - bainha dupla 30 mm
-  HARPÃO - perfil de alumínio 40 x 20 nos arcos / terças / cabos

QUADRO DE PAINÉIS

Cód.	Qtd	Caixa (m)	Área m2	Grupo
P1	1	1,72 x 1,46	15,64	Lona Externa
P2	1	1,48 x 1,64	15,15	Lona Externa
T3D	2	1,24 x 1,87	2,26	Lona Externa
P3D	2	1,27 x 3,64	4,50	Lona Externa
T4D	2	1,38 x 1,94	2,24	Lona Externa
T4D	2	1,43 x 3,60	4,30	Lona Externa
P6D	2	2,06 x 5,30	6,35	Lona Externa
P6	1	2,57 x 10,32	12,72	Lona Externa
P7	1	2,99 x 8,49	11,02	Lona Externa
P8	1	3,13 x 5,02	9,57	Lona Externa
P9	1	2,83 x 6,32	9,99	Lona Externa
F1	1	0,98 x 10,70	9,07	Forro
F2	1	1,47 x 10,82	14,72	Forro
P8	1	1,29 x 10,82	13,27	Forro
F4	1	1,58 x 10,76	12,84	Forro
F5	1	1,99 x 10,40	12,47	Forro
F6	1	2,45 x 9,54	11,80	Forro
F7	1	2,80 x 7,81	10,01	Forro
F8	1	2,40 x 5,06	5,01	Forro

Total Iona externa: 111,2 m2 de forma final (+ 12 a 15 % de sobras, bolsas e emendas)

Total forro / revestimento interno: 89,2 m2 de forma final (+ 12 a 15 % de sobras, bolsas e emendas)

trilho de base 100 x 50 com perfil de arremate E02 (keder Ø13 + calha)

Vista lateral direita · costuras sobre os arcos A0 a A7 (perfil duplo keder) · painéis externos P0 a P8 · forros F1 a F8 (harpão)

HOTEL GROUP
INTERNATIONAL

MAPA DOS PAINÉIS DE LONA

Costuras sobre a estrutura · códigos dos padrões

ZION CASULO SENSORIAL
ZION GLAMPING COLLECTION

ESCALA s/ escala

PROJETO CONCEITUAL · ESTUDO PRELIMINAR

FOLHA LN-01

SET 2026

ZION CASULO SENSORIAL · PADRÃO DE CORTE T3D

Painel T3D · entre A2 (x 2.85) e A3 (x 4.05) · CRISTAL (PVC transparente 0,7 mm) · cinturão sensorial · LONA EXTERNA · geometria de forma final (sem compensação) · metros

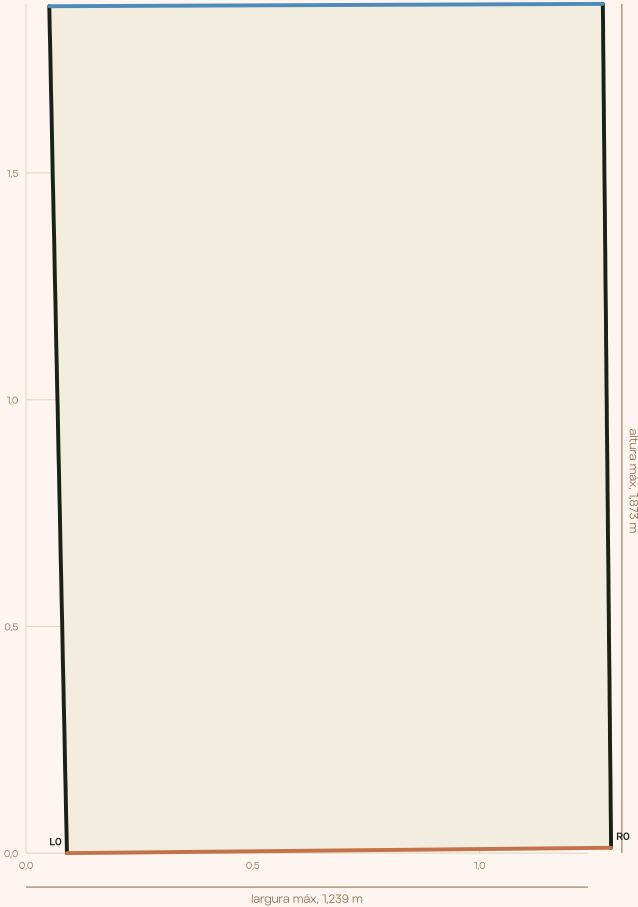


TABELA DE ESTAÇÕES (ao longo da borda L, a cada 0,50 m)

s (m)	xL	yL	xR	yR	largura
0,000	0,090	0,000	1,290	0,012	1,200
0,500	0,080	0,500	1,285	0,510	1,206
1,000	0,069	1,000	1,280	1,008	1,211
1,500	0,059	1,500	1,275	1,506	1,217
2,000	0,049	2,000	1,271	2,004	1,222
2,500	0,039	2,499	1,266	2,503	1,227
3,000	0,029	2,999	1,261	3,001	1,232
3,500	0,021	3,499	1,257	3,500	1,236
4,000	0,013	3,999	1,254	4,000	1,240
4,500	0,007	4,499	1,250	4,499	1,243
5,000	0,003	4,999	1,248	4,999	1,245
5,500	0,000	5,499	1,247	5,499	1,247
6,000	0,000	5,999	1,247	5,999	1,247
6,500	0,002	6,499	1,248	6,499	1,246
7,000	0,006	6,999	1,250	6,999	1,244
7,500	0,011	7,499	1,253	7,499	1,241
8,000	0,019	7,999	1,256	7,998	1,237
8,500	0,027	8,499	1,260	8,497	1,233
9,000	0,036	8,999	1,265	8,996	1,229
9,500	0,046	9,499	1,269	9,494	1,224
10,000	0,056	9,999	1,274	9,993	1,218
10,500	0,066	10,499	1,279	10,491	1,213
11,000	0,077	10,999	1,284	10,989	1,207
11,500	0,087	11,498	1,289	11,487	1,202
11,647	0,090	11,645	1,290	11,634	1,200

DADOS DO PAINEL

- QUANTIDADE
2 (códigos: T3D, T3E)
- ÁREA DE FORMA FINAL
2,26 m2
- COMPRIMENTO L / R
11,65 / 11,62 m
- CAIXA (LARG. X ALT.)
1,24 x 1,87 m
- MATERIAL
PVC cristal 0,7 mm (ou ETFE 250 µm em 2 folhas) soldado por HF à lona; keder Ø10 nas laterais; zíper na base
- BORDAS E RECORTES
- KEDER Ø10 - desliza no perfil duplo keder do arco / calbro
 - ZÍPER - zíper YKK #10 duplo na base do cristal (parede que abre) + keder Ø13 no trilho
 - SOLDA HF LONA-CRISTAL - emenda de 40 mm entre a lona opaca e o PVC cristal (linha da terço)

ZION HOTEL GROUP INTERNATIONAL	PADRÃO DE CORTE T3D Lona Externa
ZION CASULO SENSORIAL ZION GLAMPING COLLECTION	ESCALA ver malha (m) PROJETO CONCEITUAL · ESTUDO PRELIMINAR

FOLHA LN-13
SET 2026

ZION CASULO SENSORIAL · PADRÃO DE CORTE T4D

Painel T4D · entre A3 (x 4.05) e A4 (x 5.25) · CRISTAL (PVC transparente 0,7 mm) · cinturão sensorial · LONA EXTERNA · geometria de forma final (sem compensação) · metros

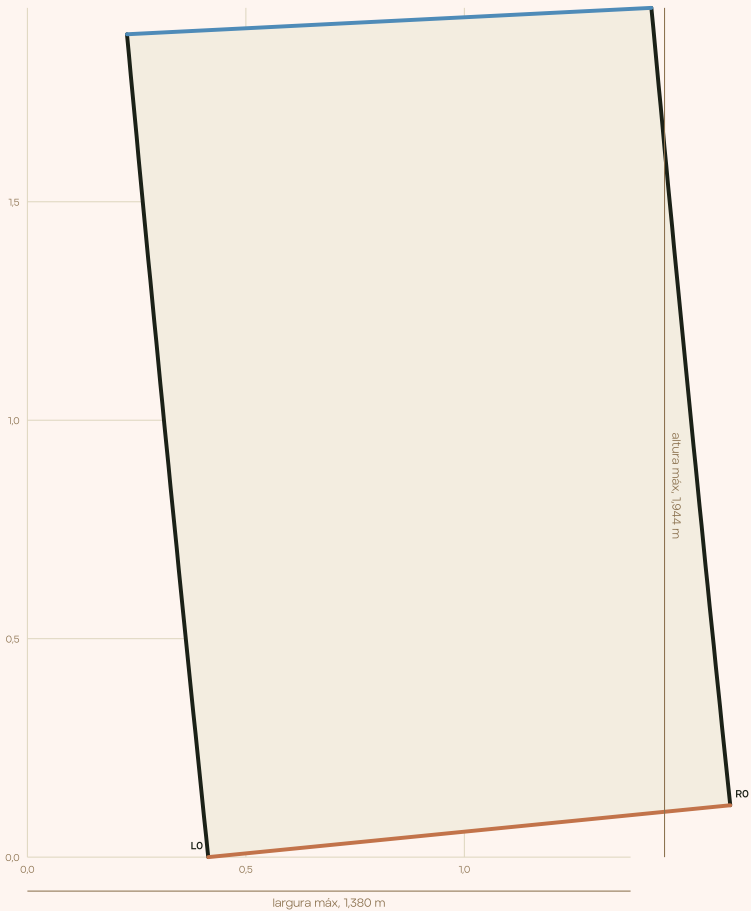


TABELA DE ESTAÇÕES (ao longo da borda L, a cada 0,50 m)

s (m)	xL	yL	xR	yR	largura
0,000	0,414	0,000	1,608	0,119	1,200
0,500	0,363	0,497	1,559	0,600	1,200
1,000	0,313	0,995	1,511	1,082	1,201
1,500	0,265	1,493	1,464	1,564	1,201
2,000	0,218	1,990	1,418	2,048	1,202
2,500	0,173	2,488	1,375	2,532	1,202
3,000	0,131	2,987	1,334	3,018	1,203
3,500	0,093	3,485	1,297	3,507	1,204
4,000	0,060	3,984	1,265	3,998	1,205
4,500	0,032	4,483	1,238	4,491	1,206
5,000	0,013	4,983	1,219	4,987	1,206
5,500	0,002	5,483	1,208	5,484	1,206
6,000	0,001	5,983	1,207	5,982	1,206
6,500	0,009	6,483	1,215	6,480	1,206
7,000	0,027	6,982	1,233	6,976	1,206
7,500	0,062	7,482	1,257	7,470	1,205
8,000	0,085	7,981	1,289	7,961	1,204
8,500	0,122	8,479	1,325	8,450	1,203
9,000	0,163	8,978	1,365	8,937	1,203
9,500	0,207	9,476	1,408	9,422	1,202
10,000	0,253	9,973	1,453	9,905	1,201
10,500	0,301	10,471	1,499	10,388	1,201
11,000	0,351	10,969	1,547	10,870	1,200
11,500	0,401	11,466	1,596	11,351	1,200
11,622	0,414	11,588	1,608	11,469	1,200

BADOS DO PAINEL

QUANTIDADE
2 (códigos: T4D, T4E)
ÁREA DE FORMA FINAL
2,24 m2
COMPRIMENTO L / R
11,62 / 11,38 m
CAIXA (LARG. X ALT.)
1,38 x 1,94 m
MATERIAL
PVC cristal 0,7 mm (ou ETFE 250 µm em 2 folhas) soldado por HF à lona; keder Ø10 nas laterais; zíper na base

BORDAS E RECORTES

- KEDER Ø10 - desliza no perfil duplo keder do arco / calbro
- ZÍPER - zíper YKK #10 duplo na base do cristal (parede que abre) + keder Ø13 no trilho
- SOLDA HF LONA-CRISTAL - emenda de 40 mm entre a lona opaca e o PVC cristal (linha da terça)

ZION HOTEL GROUP INTERNATIONAL	PADRÃO DE CORTE T4D Lona Externa
ZION CASULO SENSORIAL ZION GLAMPING COLLECTION	ESCALA ver malha (m) PROJETO CONCEITUAL · ESTUDO PRELIMINAR FOLHA LN-15 SET 2026

- NOTAS**
- Padrão = geometria de forma final da superfície entre as costuras; o confeccionista aplica a compensação do tecido (ensaio biaxial típico 0,5 a 1,5 % no urdume e 2 a 4 % na trama) e as sobras de bolsa/keder.
 - Origem (0, 0) no canto inferior esquerdo da caixa; eixo x horizontal, y vertical; L0 → L1 é a borda esquerda (costura de referência), R0 → R1 a direita; estações medidas ao longo de L.
 - Marcar em cada painel: código, modelo, orientação (L/R, base), linhas de presilha e centros dos recortes; etiqueta de tecido cosida no verso.
 - Camadas por dentro (não fazem parte deste painel): tela mosquiteira fixa no trilho de harpão e cortina de voile + blackout em trilho curvo.

COLEÇÃO BOHO / BALI · FF&E DA VARIANTE

47 itens · dossel, tablado, rattan, futons, voile, juta, macramê, cerâmica, lanternas de latão · sem preços (PREÇO A COTAR)

DIREÇÃO DE ARTE

TEMA	ESCOLHA
Paleta	creme, areia, terracota, oliva, madeira clara de teca
Materiais	teca e bambu laminado, rattan natural (sintético no deck), linho, algodão cru, juta, kilim, cerâmica artesanal, latão
Luz	2700 K, pendentes de rattan, lanternas de vela LED, LED indireto no tablado e no rodapé; nenhuma luz direta sobre a cama
Umidade de montanha	tecidos antimofo, madeira tratada, rattan sintético nas peças externas, ventilação cruzada com o cinturão aberto
Ritual	chá e café na cozinha atrás, banho de banheira sob o Olho baixo, deck com daybed suspenso sob o Bico

A OUTRA COLEÇÃO

Zion New Luxury (carvalho, quartzito, latão, linho cru) continua disponível para a variante: só o mobiliário solto muda; a marcenaria acoplada (cozinha, closet, bancada) é a mesma.

MOBILIÁRIO

CÓD.	ITEM	UN.	QTD	AMBIENTE
M19	Cama king com dossel (Bali)	un	1	Suíte · no cinturão transparente, pés para o vidro
M20	Tablado de madeira	un	1	Suíte
M03	Criado-mudo suspenso	un	2	Suíte · criados baixos em teca
M16	Ripado da cabeceira	m2	6	Banho · parede do banho, lado do banho
M22	Futon e almofadas de chão	cj	1	Lounge · sob o Bico
M23	Mesa baixa de tronco	un	1	Lounge
M21	Cadeira suspensa de rattan	un	1	Lounge
M18	Mini cozinha acoplada	un	1	Cozinha · mini cozinha em L atrás, junto ao banho
M10	Closet / armário	un	1	Closet · closet 1,10 m à direita
M12	Bancada do banho	un	1	Banho · bancada 1,50 m
M13	Espelho com iluminação	un	1	Banho

LUMINÁRIAS E DECORAÇÃO

CÓD.	ITEM	UN.	QTD	AMBIENTE
F01	Arandela de leitura	un	2	Suíte
F12	Luminárias de rattan e lanternas	cj	1	Geral
F13	Tapetes de juta e kilim	cj	1	Estar · suíte
F11	Cortinas laterais em voile + blackout	m	9,6	Cinturão transparente · 2 vãos x 2 lados = 9,6 m de trilho
F06	Cortinas e blackout	m	6,5	Fachada · voile na fachada de vidro
F07	Cortina da lanterna / óculo	un	1	Espinha de Luz
F14	Curadoria Bali	vb	1	Geral
F10	Plantas e vasos	vb	1	Geral · plantas em vasos de barro

EQUIPAMENTOS

CÓD.	ITEM	UN.	QTD	AMBIENTE
E16	Geladeira sob bancada	un	1	Cozinha
E13	Cooktop de indução 2 bocas	un	1	Cozinha
E14	Forno elétrico compacto	un	1	Cozinha
E15	Air fryer	un	1	Cozinha
E17	Depurador de ar slim	un	1	Cozinha
E02	Cafeteira de cápsulas + chaleira	cj	1	Cozinha
E03	Cofre eletrônico	un	1	Closet
E04	Caixa de som / rádio	un	1	Lounge
E06	Secador de cabelo	un	1	Banho
E10	Fechadura eletrônica	un	1	Porta PV1
E11	Termostato e automação de cenas	un	1	Ático técnico

ENXOVAL E OS&E

CÓD.	ITEM	UN.	QTD	AMBIENTE
O01	Enxoval de cama	cj	1	Suíte
O02	Enxoval de banho	cj	1	Banho
O03	Amenities	cj	1	Banho
O04	Louças, talheres e copos	cj	1	Cozinha
O09	Utensílios de cozinha	cj	1	Cozinha
O05	Manta, almofadas e decoração têxtil	cj	1	Geral

O06	Cabides, lixeiras, acessórios	cj	1	Geral
O07	Sinalização e papelaria Zion	cj	1	Geral
O08	Kit de segurança	cj	1	Geral

DECK E EXTERIOR

CÓD.	ITEM	UN.	QTD	AMBIENTE
D08	Daybed suspenso do deck	un	1	Deck - sob o Bico
D02	Mesa e cadeiras de deck	cj	1	Deck
D04	Balizadores e lanternas de deck	cj	1	Deck
D05	Ducha externa	un	1	Deck
D06	Chuveirão / banheira externa (opcional)	un	1	Deck - opcional: banheira externa

BANHO (ACESSÓRIOS)

CÓD.	ITEM	UN.	QTD	AMBIENTE
B01	Acessórios do banho	cj	1	Banho
B02	Banqueta e bandeja da banheira	cj	1	Banho
B03	Balança e acessórios	cj	1	Banho

IMPACTOS NOS LOTES E PRÓXIMOS PASSOS

como a variante entra no master plan sem duplicar contratos

LOTE	CASULO	SENSORIAL: O QUE MUDA
1 · Deck e infra	igual	pontos de água / esgoto da cozinha passam para a parede do banho (mesma parede molhada: mais simples); circuito da cortina motorizada
2 · Estrutura	igual	talões para o trilho curvo da cortina e para a cadeira suspensa (arco A1); cantoneiras da cozinha em A5 / A6 em vez de A1 / A2
3 · Lonas e vidros	P3D/E, P4D/E em lona	T3D/E, T4D/E em cristal soldado; zíperes; tela mosquiteira; trilhos curvos de cortina; 3 Olhos a menos
4 · Mobílias	New Luxury	coleção Bali (dossel, tablado, rattan, futons, voile, juta) ou New Luxury; mesma marcenaria acoplada

PRÓXIMOS PASSOS

1.

Aprovar a variante como produto (Casulo Sensorial) ou como opção de configuração do Casulo.
2.

Balanço térmico e escolha entre PVC cristal e ETFE duplo por região (frio de montanha: ETFE).

⚠️ VALIDAÇÃO OBRIGATÓRIA — ENGENHEIRO/ARQUITETO
3.

Detalhar o dossel (fixação no tablado, carga da cadeira suspensa) e o trilho curvo da cortina.
4.

Gerar IN-01 a IN-06 da variante e os lotes 3 e 4 específicos.
5.

Render fotorrealista (imagem → vídeo) com a coleção Bali para o material comercial.