



ZION

HOTEL GROUP
INTERNATIONAL

ZION GLAMPING COLLECTION · CABIN DESIGN & ENGINEERING SYSTEM

PROJETO DE INTERIORES

ZION CASULO · MARCENARIA ACOPLADA · ZC-INT-001 · REV 00 — CONCEITO · 17/09/2026

Plano arquitetônico de interiores do Zion Casulo com o mobiliário fixo já acoplado à concha e à parede do banho: planta de layout cotada, paginação de pisos, elevações internas, detalhes da marcenaria e quadros de mobiliário, acabamentos e FF&E. A marcenaria acoplada (MA) é fabricada, montada e acabada em fábrica junto com a cabana; o mobiliário solto (MS) é o FF&E entregue montado.

Anexo do documento técnico ZG-TEC-001 (seção 25). Sem preços. Dimensões em metros; tolerância de fabricação ± 3 mm; conferência com o gabarito da seção da concha antes da produção.

MEMORIAL DE INTERIORES

conceito, regras de acoplamento, materiais e luz

O interior do Casulo é um único eixo: vestíbulo, estar, suíte e banho na cauda. A marcenaria acoplada faz a divisão dos ambientes sem paredes: a mini cozinha (geladeira, forno, cooktop de indução de 2 bocas, cuba e air fryer) e o armário baixo se encostam na curva da concha do lado esquerdo, a cabeceira estofada com criados suspensos se fixa à parede do banho, e a bancada em pedra ocupa o lado do banho da mesma parede. Tudo o que é fixo nasce na fábrica com a cabana; o que é solto (cama, chaise, poltrona, mesa lateral, luminárias, tapetes) é o FF&E Zion New Luxury.

REGRAS DE ACOPLAMENTO

1.

Fixação sempre à estrutura (arcos e trilhos de base) por cantoneiras galvanizadas; nunca à membrana nem ao forro.
2.

Fundos e laterais recortados com o gabarito da seção da concha, folga de 15 mm fechada com perfil de EPDM.
3.

Rodapé técnico removível de 150 mm em todo o perímetro: eletrodutos, PEX e caixas de passagem acessíveis sem desmontar móveis.
4.

Elétrica embutida na marcenaria (tomadas, USB, LED) com ponto de conexão no rodapé técnico.
5.

Peças de até 1,40 m para caber no contêiner e passar pela porta PV1 (1,00 x 2,40); montagem em campo só por nivelamento e fixação.
6.

Materiais naturais e reparáveis: carvalho em lâmina sobre MDF naval, ripado termotratado, quartzito, linho, latão escovado.

LUZ POR AMBIENTE

Estar: fita LED na prateleira da ilha e no rodapé técnico, luminária de piso e de mesa, cena "chegada" a 60 %. Suíte: retroiluminação da cabeceira, arandelas de leitura articuladas, cena "noite" a 10 %, tela da Espinha de Luz. Banho: espelho com LED perimetral, fita sob o gabinete suspenso, luz de vigília no rodapé. Tudo 2700 K, dimerizável, sem pendentes.


MATERIAIS

ELEMENTO	MATERIAL E ACABAMENTO
Marcenaria (MA)	carvalho natural em lâmina sobre MDF naval 18 mm · verniz PU fosco
Ripados	pinus termotratado 20 x 40 mm, fixação oculta, mesmo tom do carvalho
Pedras	quartzito 30 mm bordas retas polidas (ilha, armário, bancada, prateleira da banheira)
Estofados	linho natural cru (cabeceira), bouclé antimancha (chaise, poltrona)
Metais	latão escovado: misturadores, puxadores, arandelas, soleiras
Pisos	carvalho de engenharia 14 mm · porcelanato 60 x 120 areia clara · cumaru no deck
Têxteis	tapetes de lã tecidos à mão, cortinas de linho + blackout, enxoval 400 fios



ZION CASULO · PLANTA DE LAYOUT DE INTERIORES

Marcenaria acoplada (MA) e mobiliário solto (MS) · cotas de mobiliário e circulação · 1:50

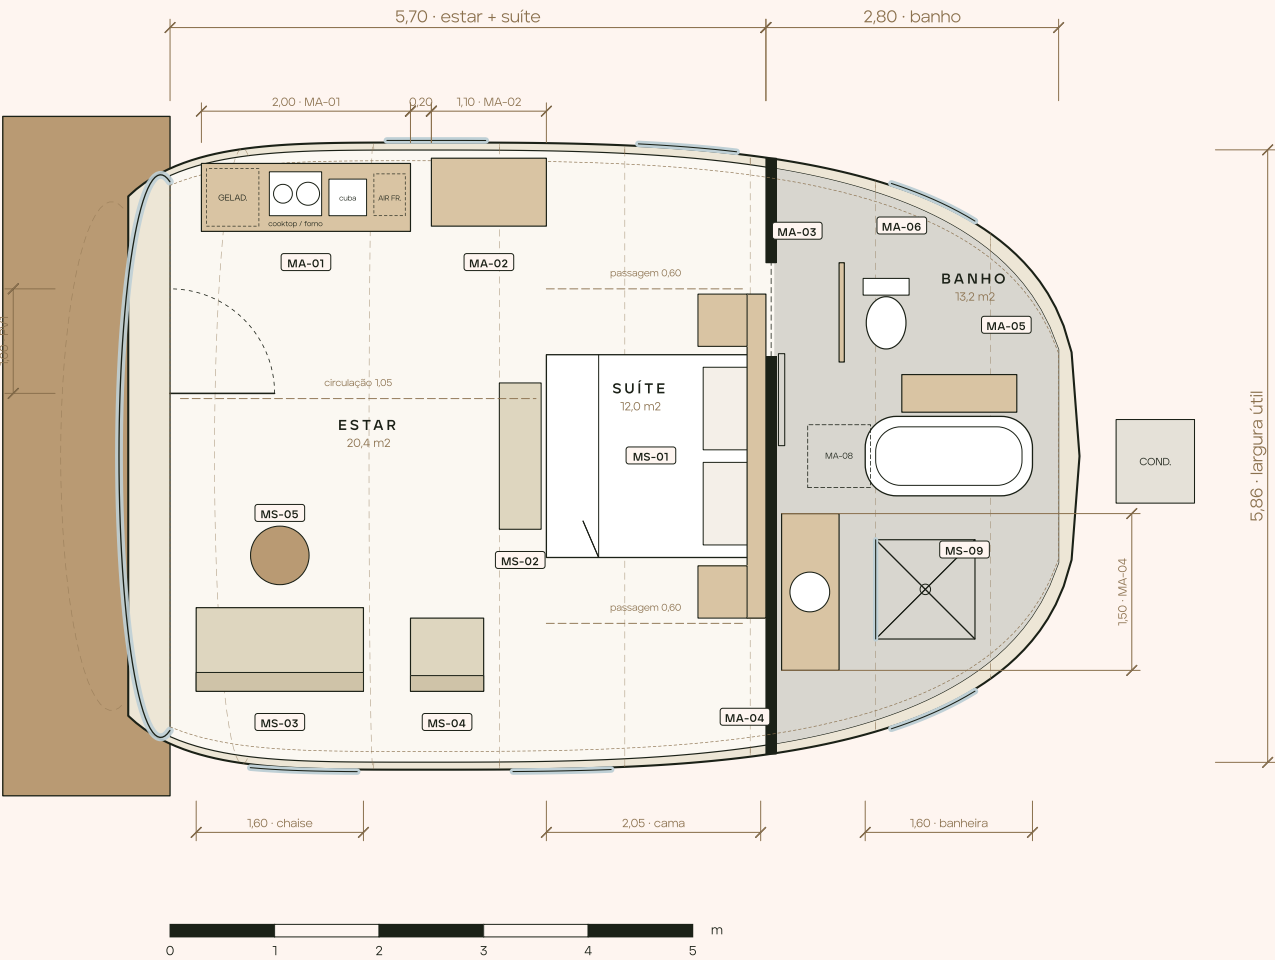

LEGENDA

- MA - marcenaria acoplada (fixa, fabricada com a cabana)
- MS - mobiliário solto (FF&E, entregue montado)
- MA-07 - rodapé técnico removível 150 mm

MARCENARIA ACOPLADA

- MA-01 Mini cozinha acoplada · Estar
- MA-02 Armário baixo / closet embutido · Estar / suite
- MA-03 Cabeceira acoplada com criados suspensos · Suíte
- MA-04 Bancada do banho · Banho
- MA-05 Prateleira e nicho da banheira · Banho
- MA-06 Divisória da bacia e painel ripado · Banho
- MA-07 Rodapé técnico removível · Todos
- MA-08 Tampa do ático técnico · Banho (forro)


MOBILIÁRIO SOLTO

- MS-01 Cama king box · 1,95 x 2,03 x 0,55
- MS-02 Banco aos pés da cama · 1,40 x 0,40 x 0,45
- MS-03 Chaise de contemplação · 1,60 x 0,80 x 0,45
- MS-04 Poltrona de leitura · 0,70 x 0,70 x 0,75
- MS-05 Mesa lateral · Ø0,56 x 0,45
- MS-06 Luminária de piso · de mesa —
- MS-07 Tapetes de lã · 2,00 x 3,00 · 1,60 x 2,30
- MS-08 Lareira ecológica · 0,60 x 0,30 x 0,35
- MS-09 Banqueta e bandeja da banheira · 0,45 x 0,30 x 0,45

 ZION ZION GLAMPING COLLECTION	PLANTA DE LAYOUT DE INTERIORES Marcenaria acoplada MA-01 a MA-08 · mobiliário solto MS-01 a MS-09	
	ESCALA 1:50 (A1) · cotas em metros PROJETO CONCEITUAL · ESTUDO PRELIMINAR	FOLHA IN-01 SET 2026

ZION CASULO · PAGINAÇÃO DE PISOS E QUADRO DE ACABAMENTOS

Sentido das réguas, transições, soleiras, ralo linear, tapetes · 1:50

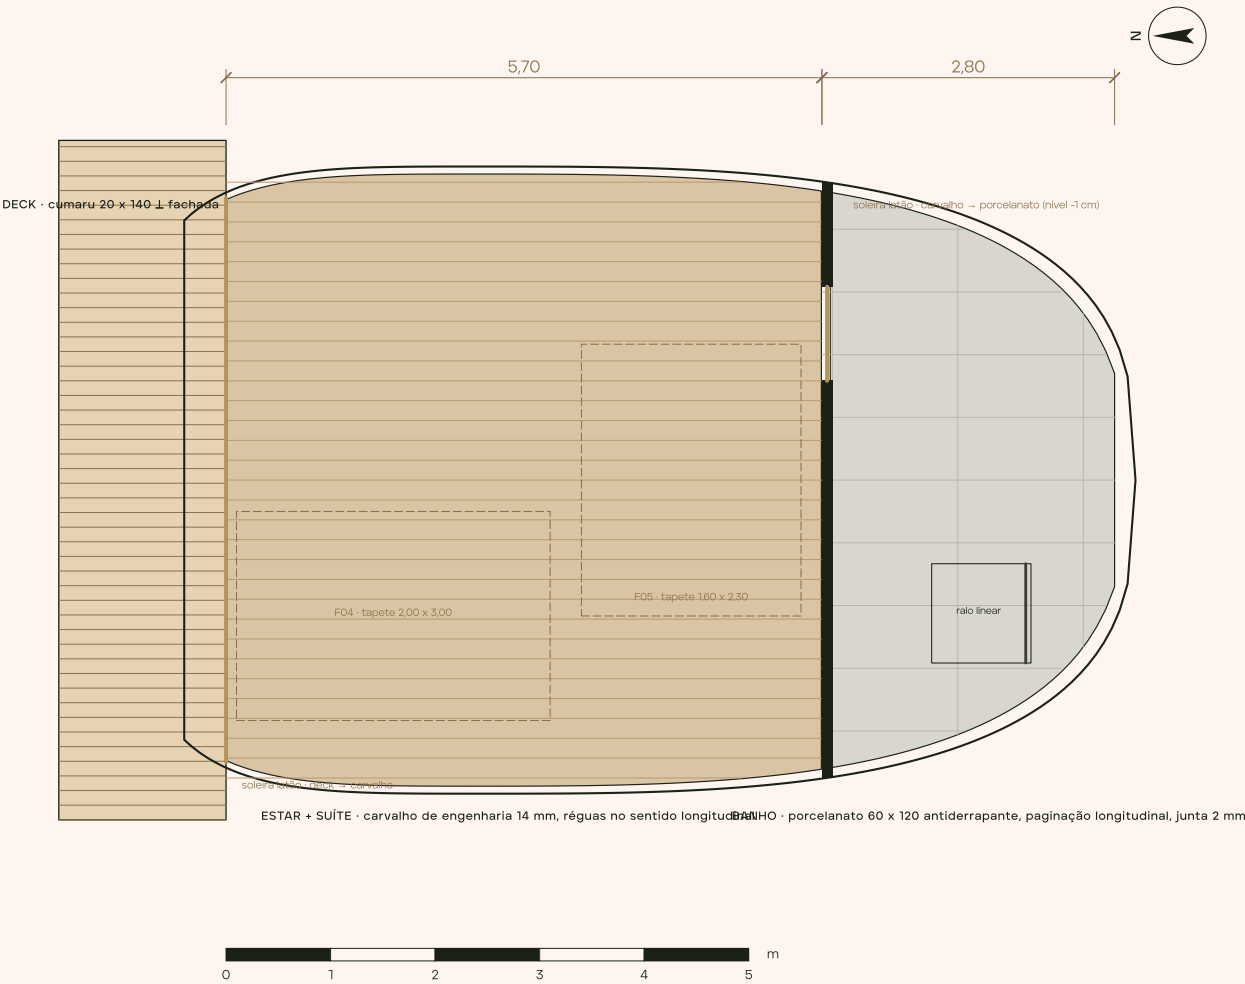

QUADRO DE ACABAMENTOS

AMBIENTE	PISO	RODAPÉ	PAREDES	FORRO
Vestibulo	cumaru 20 x 140 (deck)	—	membrana / vidro	membrana
Estar	carvalho de engenharia 14 mm, réguas no sentido x	ripado técnico 150 mm	forro tensionado Trevira CS creme · ripado junto ao piso · frontão em quartzito atrás do cooktop	tensionado creme, Espinha de Luz
Suite	carvalho de engenharia 14 mm	ripado técnico 150 mm	ripado termotratado na cabeceira	tensionado creme
Banho	porcelanato 60 x 120 antiderrapante, paginação longitudinal	porcelanato h 10 cm	porcelanato na zona molhada · ripado nas demais	forro naval pintado, 2,40 m
Deck	cumaru 20 x 140, réguas L à fachada	—	—	—

NOTAS

Carvalho flutuante sobre manta; junta de dilatação de 10 mm sob o rodapé técnico.

Porcelanato assentado com AC-III e rejunte epóxi sobre impermeabilização; calamento 1 % para o ralo linear.

Soleiras em latão escovado 40 x 8 mm; degrau de 1 cm entre carvalho e porcelanato.


Deck com clips ocultos inox e junta de 6 mm; óleo protetor.

Cores: piso carvalho natural fosco · porcelanato areia clara · rodapé ripado no tom do carvalho.


 ZION HOTEL GROUP INTERNATIONAL	PAGINAÇÃO DE PISOS E ACABAMENTOS Quadro de acabamentos por ambiente	
ZION CASULO ZION GLAMPING COLLECTION	ESCALA 1:50 (A1) · cotas em metros PROJETO CONCEITUAL · ESTUDO PRELIMINAR	FOLHA IN-02 SET 2026

ZION CASULO · ELEVAções INTERNAS A E B
A · parede da cabeceira (olhar +x) · B · lateral esquerda: mini cozinha, armário e Olhos (olhar +y) · 1:40

ELEVAção A · CABECEIRA · x = 6,60

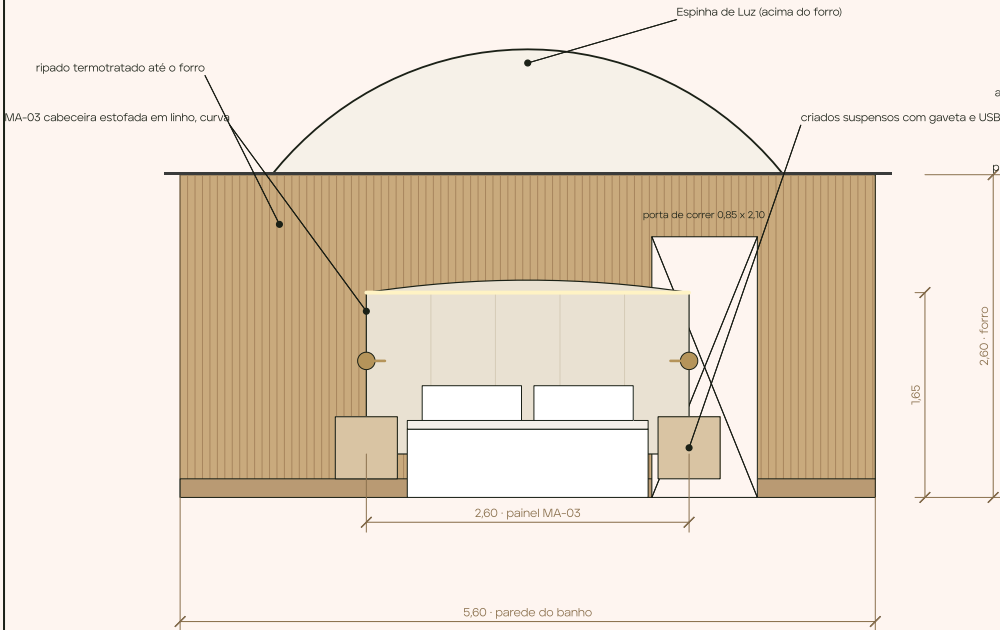

ELEVAção B · LATERAL ESQUERDA · y = +2,90

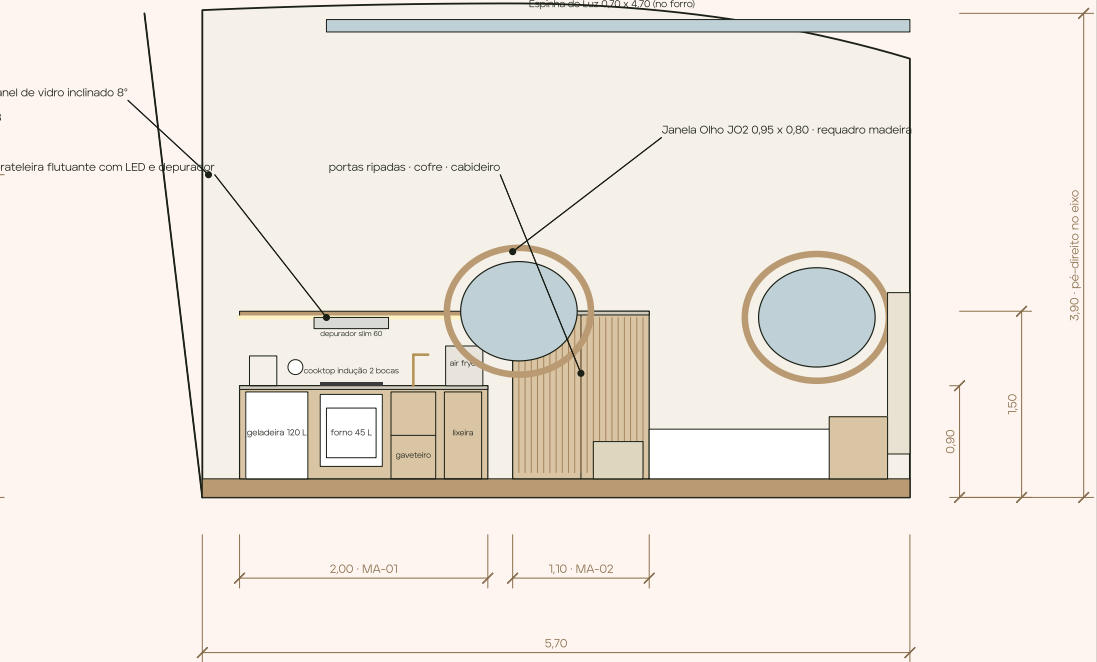


ZION HOTEL GROUP INTERNATIONAL	ELEVAções INTERNAS A E B Cabeceira acoplada MA-03 · mini cozinha MA-01 · armário MA-02	
ZION CASULO ZION GLAMPING COLLECTION	ESCALA 1:40 (A1) · cotas em metros PROJETO CONCEITUAL · ESTUDO PRELIMINAR	FOLHA IN-03 SET 2026


 ZION CASULO · ELEVAÇÕES INTERNAS C E D

C · banho, parede da bancada (olhar -x) · D · fachada de vidro vista de dentro (olhar -x) · 1:40

ELEVAÇÃO C · BANHO · x = 6,70

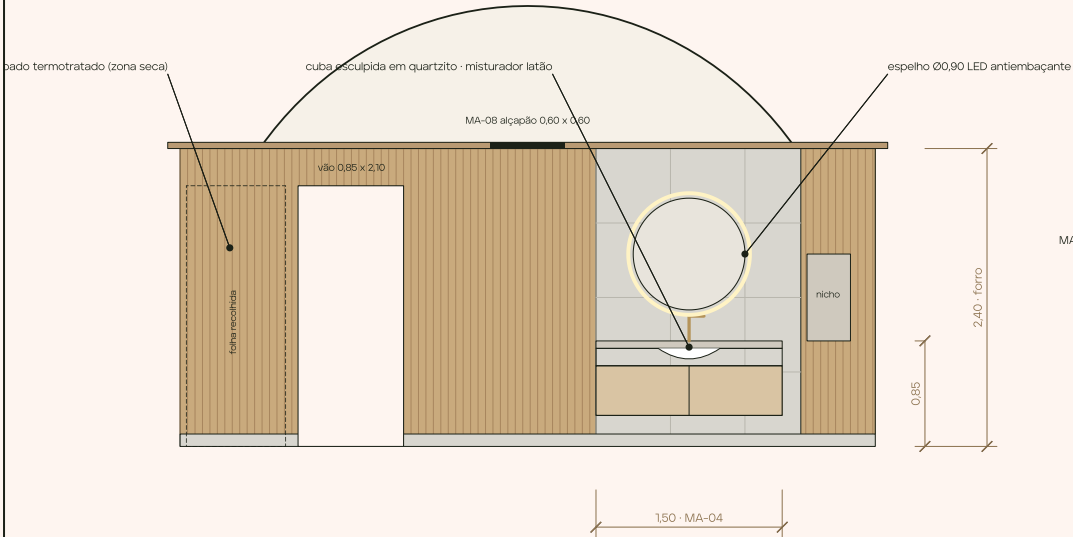


ELEVAÇÃO D · FACHADA INTERNA · x = 0,90

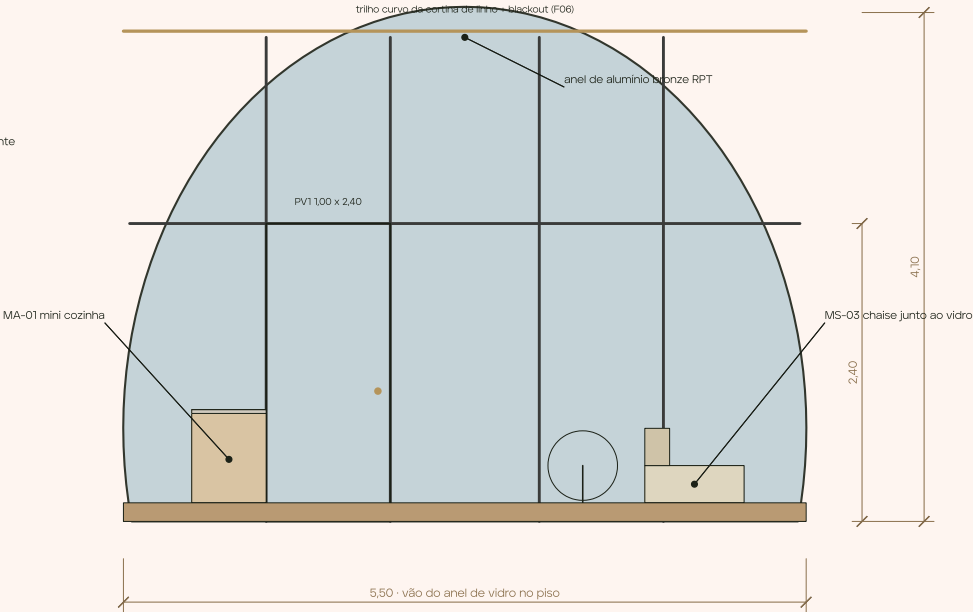


 ZION HOTEL GROUP INTERNATIONAL	ELEVAÇÕES INTERNAS C E D Bancada MA-04 · fachada, porta PV1, chaise e cortina	
ZION CASULO ZION GLAMPING COLLECTION	ESCALA 1:40 (A1) · cotas em metros PROJETO CONCEITUAL · ESTUDO PRELIMINAR	FOLHA IN-04 SET 2026

 ZION CASULO · DETALHES DA MARCENARIA ACOPLADA

MA-01 mini cozinha · MA-03 cabeceira e criado · MA-04 bancada do banho · MA-02 armário na curva · 1:20 e 1:10

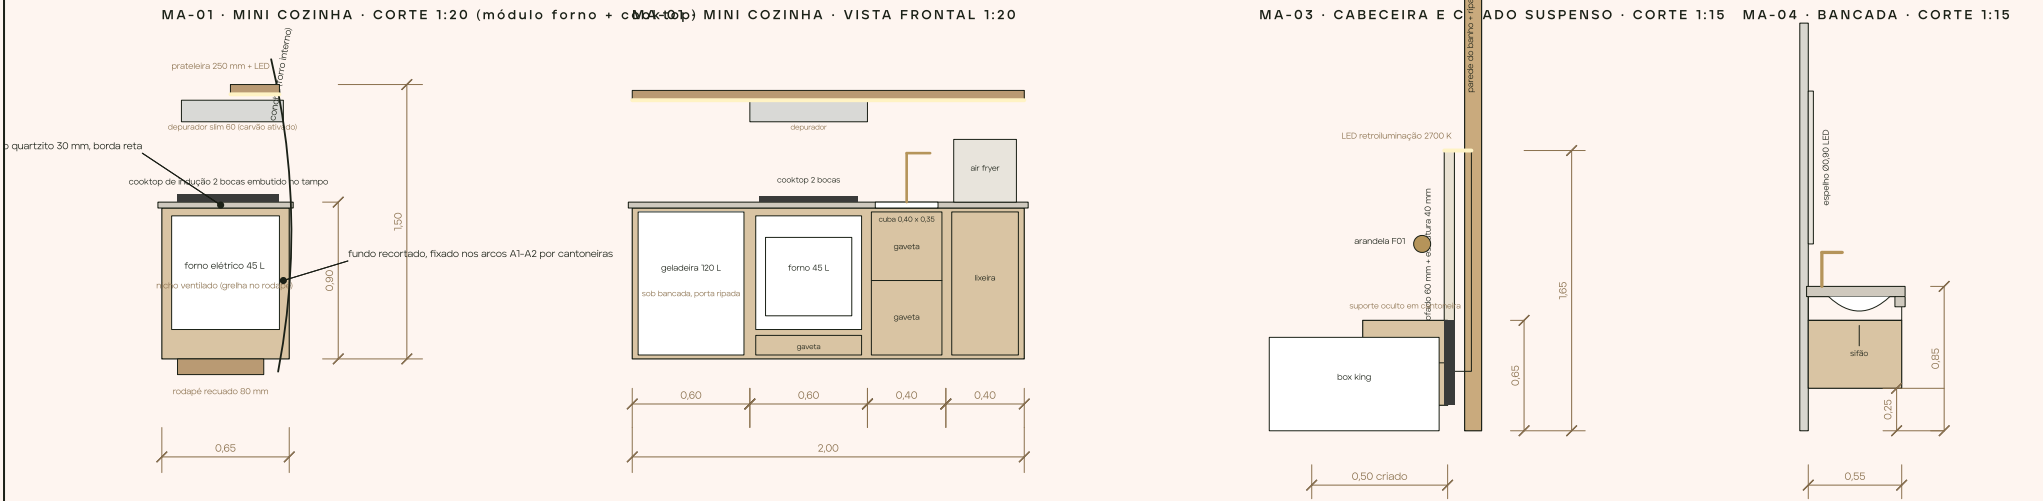

MA-02 · ARMÁRIO ACOPLADO À CURVA · CORTE 1:20

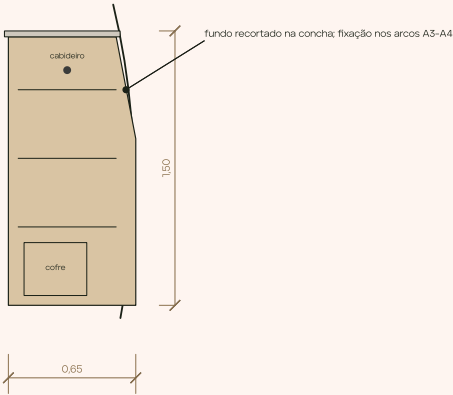

NOTAS DE MARCENARIA ACOPLADA

- Toda a marcenaria MA é fabricada em fábrica, montada e acabada antes do embarque; em campo só se nivela e se fixa.
- Fixação à estrutura: cantoneiras de aço galvanizado parafusadas aos arcos (nunca à membrana); fundos recortados com folga de 15 mm para a concha e fechados com perfil de EPDM.
- Madeira: carvalho natural em lâmina sobre MDF naval 18 mm; ripado termotratado 20 x 40; verniz PU fosco 2 demãos.
- Pedra: quartzito 30 mm, bordas retas polidas; cubas esculpidas com impermeabilização de fábrica.
- Ferragens: dobradiças e corredeiras com amortecimento; puxadores cava ou em latão escovado; fitas LED 2700 K IP20 (IP65 no banho) com perfil difusor.
- Elétrica embutida na marcenaria: cooktop (C13, 20 A) e forno (C14, 16 A) em circuitos dedicados, tomadas da mini cozinha (C5), USB nos criados; passagem pelo rodapé técnico MA-07; cuba com AF/AQ Ø20 e sifão Ø50.
- Tolerâncias: ± 3 mm nas dimensões; conferência com gabarito da seção da concha antes da fabricação (arcos A1 a A4).

 ZION HOTEL GROUP INTERNATIONAL	DETALHES DA MARCENARIA ACOPLADA	
	MA-01 mini cozinha · MA-02 · MA-03 · MA-04	
ZION CASULO ZION GLAMPING COLLECTION	ESCALA 1:20 / 1:10 (A1)	FOLHA IN-05
	PROJETO CONCEITUAL · ESTUDO PRELIMINAR	SET 2026

 ZION CASULO · QUADRO DE MOBILIÁRIO E MARCENARIA

Marcenaria acoplada (MA) com descrição, dimensões, materiais e FF&E relacionado · mobiliário solto (MS) · 1:50 na planta IN-01

MARCENARIA ACOPLADA

CÓD.	PEÇA	DIMENSÕES (M)	AMB.	FF&E	DESCRIÇÃO	MATERIAIS / ACABAMENTO
MA-01	Mini cozinha acoplada	2,00 x 0,65 x h 0,90	Estar	M18 · E13 · E14 · E15 · E16 · E17 · E02	Gabinete de 2,00 m acoplado à curva da concha (fundo recortado conforme a seção), em 4 módulos de 0,60 / 0,60 / 0,40 / 0,40; geladeira 120 L sob bancada · forno elétrico compacto 45 L sob o cooktop de indução 2 bocas · cuba 0,40 x 0,35 com torneira gourmet sobre gaveteiro · bancada de preparo com air fryer em nicho e lixeira embutida; tampo em quartzito 30 mm; prateleira flutuante 2,00 x 0,25 a 1,45 m com fita LED e depurador slim 60 cm (filtro de carvão) sob a prateleira; cafeteira e chaleira sobre o tampo	Carvalho natural (portas ripadas) · quartzito · latão escovado · inox
MA-02	Armário baixo / closet embutido	1,10 x 0,65 x h 1,50	Estar / suíte	M10 · E03	Armário de 1,10 m com 2 portas ripadas; cabideiro 0,80 m, 3 prateleiras; gaveta e cofre; tampo em pedra com bandeja; tampo posterior inclinado acompanhando a concha	Carvalho natural · ripado termotratado · quartzito
MA-03	Cabeceira acoplada com criados suspensos	0,18 x 3,10 x h 1,30	Suíte	M02 · M03 · M16 · F01	Painel curvo estofado em linho 2,60 x 1,30 m fixado à parede do banho; criados suspensos 0,60 x 0,50 a 0,15 m do piso (gaveta com toque), arandelas de leitura, USB e LED de retroiluminação; ripado termotratado da cabeceira até o forro (2,60 m)	Estofado linho · madeira laminada · ripado termotratado · latão
MA-04	Bancada do banho	0,55 x 1,50 x h 0,85	Banho	M12 · M13 · B01	Tampo em pedra 30 mm com cuba esculpida, sala 60 mm; gabinete ripado suspenso (base a 0,25 m) com 2 portas e nicho aberto; espelho Ø0,90 com LED perimetral e antiembaçante; nicho lateral em pedra	Quartzito · ripado termotratado · latão escovado
MA-05	Prateleira e nicho da banheira	1,10 x 0,36 x h 0,60	Banho	B02	Prateleira em pedra 1,10 x 0,36 m a 0,60 m; acoplada à curva da cauda sobre a banheira; nicho para velas e amenities; banqueta e bandeja	Quartzito · madeira
MA-06	Divisória da bacia e painel ripado	0,05 x 0,95 x h 1,20	Banho	M16	Painel ripado de 1,20 m que separa a bacia da circulação; com nicho de papel e apoio; painel ripado contínuo na face do banho da parede divisória	Ripado termotratado sobre placa cimentícia
MA-07	Rodapé técnico removível	8,50 m lineares x h 0,15	Todos	—	Rodapé de 150 mm em ripado ao longo de toda a concha, removível (fixação por cliques) para acesso a eletrodutos, PEX e caixas de passagem; admissão da câmara ventilada	Ripado termotratado · cliques inox
MA-08	Tampa do ático técnico	0,60 x 0,60	Banho (forro)	E11	Alçapão 0,60 x 0,60 no forro do banho (2,40 m) com escada retrátil: acesso a QDC, evaporadora e boiler	Compensado naval + ripado

MOBILIÁRIO SOLTO (FF&E)

CÓD.	PEÇA	DIMENSÕES (M)	AMB.	FF&E	POSIÇÃO
MS-01	Cama king box	1,93 x 2,03 x 0,55	Suíte	M01 · O01	pés para a fachada, cabeceira em MA-03
MS-02	Banco aos pés da cama	1,40 x 0,40 x 0,45	Suíte	M11	x 4,05
MS-03	Chaise de contemplação	1,60 x 0,80 x 0,45	Estar	M06	junto à fachada de vidro, lado direito
MS-04	Poltrona de leitura	0,70 x 0,70 x 0,75	Estar	M07	sob o Olho do estar (dir.)
MS-05	Mesa lateral	00,56 x 0,45	Estar	M08	entre a chaise e a poltrona
MS-06	Luminária de piso · de mesa	—	Estar	F02 · F03	ao lado da poltrona · sobre MA-02
MS-07	Tapetes de lã	2,00 x 3,00 · 1,60 x 2,30	Estar · suíte	F04 · F05	sob a chaise/poltrona · sob a cama
MS-08	Lareira ecológica	0,60 x 0,30 x 0,35	Estar	E08	sobre MA-02 (opcional)
MS-09	Banqueta e bandeja da banheira	0,45 x 0,30 x 0,45	Banho	B02	ao lado da banheira

Itens de FF&E não posicionados na planta (enxoval, amenities, papelaria, kit de segurança, luminárias de deck) constam da lista completa em ffe.py / Catálogo da Linha.

 **ZION** | HOTEL GROUP INTERNATIONAL

QUADRO DE MOBILIÁRIO E MARCENARIA
MA-01 a MA-08 · MS-01 a MS-09

ZION CASULO
ZION GLAMPING COLLECTION

ESCALA s/ escala (A1)
PROJETO CONCEITUAL · ESTUDO PRELIMINAR

FOLHA IN-06
SET 2026

QUADRO DE MARCENARIA ACOPLADA E MOBILIÁRIO SOLTO

MA fabricado com a cabana · MS entregue montado (FF&E)

CÓD.	PEÇA	DIMENSÕES (M)	AMB.	FF&E	DESCRIÇÃO	MATERIAIS
MA-01	Mini cozinha acoplada	2,00 x 0,65 x h 0,90	Estar	M18 · E13 · E14 · E15 · E16 · E17 · E02	Gabinete de 2,00 m acoplado à curva da concha (fundo recortado conforme a seção), em 4 módulos de 0,60 / 0,60 / 0,40 / 0,40: geladeira 120 L sob bancada · forno elétrico compacto 45 L sob o cooktop de indução 2 bocas · cuba 0,40 x 0,35 com torneira gourmet sobre gaveteiro · bancada de preparo com air fryer em nicho e lixeira embutida; tampo em quartzito 30 mm; prateleira flutuante 2,00 x 0,25 a 1,45 m com fita LED e depurador slim 60 cm (filtro de carvão) sob a prateleira; cafeteira e chaleira sobre o tampo	Carvalho natural (portas ripadas) · quartzito · latão escovado · inox
MA-02	Armário baixo / closet embutido	1,10 x 0,65 x h 1,50	Estar / suite	M10 · E03	Armário de 1,10 m com 2 portas ripadas, cabideiro 0,80 m, 3 prateleiras, gaveta e cofre; tampo em pedra com bandeja; tampo posterior inclinado acompanhando a concha	Carvalho natural · ripado termotratado · quartzito
MA-03	Cabeceira acoplada com criados suspensos	0,18 x 3,10 x h 1,30	Suite	M02 · M03 · M16 · F01	Painel curvo estofado em linho 2,60 x 1,30 m fixado à parede do banho, criados suspensos 0,60 x 0,50 a 0,15 m do piso (gaveta com toque), arandelas de leitura, USB e LED de retroiluminação; ripado termotratado da cabeceira até o forro (2,60 m)	Estofado linho · madeira laminada · ripado termotratado · latão
MA-04	Bancada do banho	0,55 x 1,50 x h 0,85	Banho	M12 · M13 · B01	Tampo em pedra 30 mm com cuba esculpida, saia 60 mm, gabinete ripado suspenso (base a 0,25 m) com 2 portas e nicho aberto; espelho Ø0,90 com LED perimetral e antiembaçante; nicho lateral em pedra	Quartzito · ripado termotratado · latão escovado
MA-05	Prateleira e nicho da banheira	1,10 x 0,36 x h 0,60	Banho	B02	Prateleira em pedra 1,10 x 0,36 m a 0,60 m, acoplada à curva da cauda sobre a banheira; nicho para velas e amenities; banqueta e bandeja	Quartzito · madeira
MA-06	Divisória da bacia e painel ripado	0,05 x 0,95 x h 1,20	Banho	M16	Painel ripado de 1,20 m que separa a bacia da circulação, com nicho de papel e apoio; painel ripado contínuo na face do banho da parede divisória	Ripado termotratado sobre placa cimentícia
MA-07	Rodapé técnico removível	8,50 m x h 0,15	Todos	—	Rodapé de 150 mm em ripado ao longo de toda a concha, removível (fixação por cliques) para acesso a eletrodutos, PEX e caixas de passagem; admissão da câmara ventilada	Ripado termotratado · cliques inox
MA-08	Tampa do ático técnico	0,60 x 0,60	Banho (forro)	E11	Alçapão 0,60 x 0,60 no forro do banho (2,40 m) com escada retrátil: acesso a QDC, evaporadora e boiler	Compensado naval + ripado

MOBILIÁRIO SOLTO

CÓD.	PEÇA	DIMENSÕES (M)	AMB.	FF&E	POSICÃO
MS-01	Cama king box	1,93 x 2,03 x 0,55	Suite	M01 · O01	pés para a fachada, cabeceira em MA-03
MS-02	Banco aos pés da cama	1,40 x 0,40 x 0,45	Suite	M11	x 4,05
MS-03	Chaise de contemplação	1,60 x 0,80 x 0,45	Estar	M06	junto à fachada de vidro, lado direito
MS-04	Poltrona de leitura	0,70 x 0,70 x 0,75	Estar	M07	sob o Olho do estar (dir.)
MS-05	Mesa lateral	Ø0,56 x 0,45	Estar	M08	entre a chaise e a poltrona
MS-06	Luminária de piso · de mesa	—	Estar	F02 · F03	ao lado da poltrona · sobre MA-02
MS-07	Tapetes de lã	2,00 x 3,00 · 1,60 x 2,30	Estar · suite	F04 · F05	sob a chaise/poltrona · sob a cama
MS-08	Lareira ecológica	0,60 x 0,30 x 0,35	Estar	E08	sobre MA-02 (opcional)
MS-09	Banqueta e bandeja da banheira	0,45 x 0,30 x 0,45	Banho	B02	ao lado da banheira

QUADRO DE ACABAMENTOS E LISTA DE FF&E DO CASULO

50 itens Zion New Luxury · sem preços

AMBIENTE	PISO	RODAPÉ	PAREDES	FORRO	MARCENARIA
Vestíbulo	cumaru 20 x 140 (deck)	—	membrana / vidro	membrana	—
Estar	carvalho de engenharia 14 mm, réguas no sentido x	ripado técnico 150 mm	forro tensionado Trevira CS creme · ripado junto ao piso · frontão em quartzito atrás do cooktop	tensionado creme, Espinha de Luz	MA-01 mini cozinha · MA-02
Suíte	carvalho de engenharia 14 mm	ripado técnico 150 mm	ripado termotratado na cabeceira	tensionado creme	MA-03
Banho	porcelanato 60 x 120 antiderrapante, paginação longitudinal	porcelanato h 10 cm	porcelanato na zona molhada · ripado nas demais	forro naval pintado, 2,40 m	MA-04 a MA-06
Deck	cumaru 20 x 140, réguas ⊥ à fachada	—	—	—	—

FF&E · TUDO O QUE VAI DENTRO

CÓD.	ITEM	ESPECIFICAÇÃO	AMBIENTE	QTD	UN.	OBS.
M01	Cama king box + colchão	Box 1,93 x 2,03 revestido em linho, colchão molas ensacadas 32 cm, pillow top	Suíte	1	un	
M02	Cabeceira estofada	Painel curvo em madeira laminada com estofado em linho, integrado à marcenaria	Suíte	1	un	cabeceira curva sob a Espinha de Luz
M03	Criado-mudo suspenso	Carvalho natural, gaveta com fecho toque, iluminação embutida	Suíte	2	un	
M11	Banco aos pés da cama	Banco 1,40 m em madeira e couro	Suíte	1	un	
M16	Ripado da cabeceira	Painel ripado termotratado com fitas LED (parede da cabeceira)	Suíte / banho	12	m2	parede da cabeceira
M06	Chaise de contemplação	Chaise 1,60 x 0,80 em madeira e corda náutica, almofada impermeável	Estar	1	un	junto à fachada de vidro
M07	Poltrona de leitura	Poltrona giratória em couro natural e madeira	Estar	1	un	
M08	Mesa de centro / lateral	Tampo em pedra (quartzito) sobre base de madeira torneada	Estar	1	un	mesa lateral Ø0,56
M18	Mini cozinha acoplada	Marcenaria sob medida 2,00 m acoplada à concha: tampo em quartzito, cuba, módulos para geladeira, forno, gaveteiro e lixeira, prateleira com LED (Casulo)	Estar	1	un	mini cozinha 2,00 m
M10	Closet / armário	Marcenaria em carvalho com portas ripadas, cabideiro, prateleiras e cofre	Estar	1	un	armário baixo embutido 1,10 m
M12	Bancada do banho	Tampo em pedra com cuba esculpida, gabinete ripado suspenso	Banho	1	un	bancada 1,50 m
M13	Espelho com iluminação	Espelho redondo Ø0,90 com LED perimetral e antiembaçante	Banho	1	un	
F01	Arandela de leitura	Arandela articulada em latão escovado, LED 2700 K dimerizável	Suíte	2	un	
F02	Luminária de piso	Luminária de piso em madeira e linho, 2700 K	Estar	1	un	
F03	Luminária de mesa	Abajur cerâmico artesanal, 2700 K	Estar	1	un	
F04	Tapete de lã	Tapete de lã tecido à mão 2,00 x 3,00	Estar	1	un	
F05	Tapete de lã (pequeno)	Tapete de lã 1,60 x 2,30	Suíte	1	un	
F06	Cortinas e blackout	Cortina de linho + blackout motorizado, por metro linear de fachada de vidro	Fachada	6,50	m	6,50 m de fachada de vidro
F07	Cortina da lanterna / óculo	Tela de sombreamento motorizada circular	Espinha de Luz	1	un	tela de sombreamento 0,70 x 4,70
F08	Arte e objetos	Curadoria Zion: peças de artesanato regional, cerâmica, vasos, livros	Geral	1	vb	
F10	Plantas e vasos	Plantas de interior em vasos de cerâmica	Geral	1	vb	
E16	Geladeira sob bancada	Refrigerador 120 L sob bancada com congelador, classe A, silencioso (< 40 dB), porta com painel ripado	Mini cozinha	1	un	sob bancada
E13	Cooktop de indução 2 bocas	Cooktop de indução 2 zonas, 30 x 52 cm, 3,5 kW, 220 V, embutido no tampo	Mini cozinha	1	un	circuito dedicado C13
E14	Forno elétrico compacto	Forno elétrico de embutir 45 L, 60 cm, 1,8 kW, porta de vidro duplo, 220 V	Mini cozinha	1	un	circuito dedicado C14
E15	Air fryer	Fritadeira sem óleo 5 L, 1,5 kW, em nicho ventilado sobre o tampo	Mini cozinha	1	un	
E17	Depurador de ar slim	Depurador 60 cm com filtro de carvão ativado, 2 velocidades, LED, recirculação	Mini cozinha	1	un	
E02	Cafeteira de cápsulas + chaleira	Cafeteira de cápsulas premium e chaleira elétrica de pescoço de ganço	Mini cozinha	1	cj	
E03	Cofre eletrônico	Cofre digital 20 L para notebook	Armário	1	un	
E04	Caixa de som / rádio	Sistema de som Bluetooth de mesa	Estar	1	un	
E06	Secador de cabelo	Secador profissional 2000 W com suporte	Banho	1	un	
E08	Aquecedor / lareira ecológica	Lareira a etanol de mesa ou de piso (inverno)	Estar	1	un	
E10	Fechadura eletrônica	Fechadura digital com cartão/senha na porta principal	Porta PV1	1	un	
E11	Termostato e automação de cenas	Central de automação (cenas de luz, cortinas, clima, som)	Ático técnico	1	un	
O01	Enxoval de cama	3 jogos: lençóis 400 fios algodão egípcio, edredom, duvet, protetor, 6 travesseiros	Suíte	1	cj	

O02	Enxoval de banho	3 jogos: toalhas de banho/rosto/piso 600 g/m2, roupões, chinelos	Banho	1	cj	
O03	Amenities	Dispensers de vidro (shampoo, condicionador, sabonete, hidratante) + kit de boas-vindas (estoque inicial)	Banho	1	cj	
O04	Louças, talheres e copos	Serviço para 4 (café da manhã e taças de vinho), bandeja, cesta	Mini cozinha	1	cj	
O09	Utensílios de cozinha	Jogo de panelas para indução, frigideira, tábua, facas, utensílios, escorredor, potes	Mini cozinha	1	cj	
O05	Manta, almofadas e decoração têxtil	Manta de lã, 6 almofadas, cortina de banho em linho	Geral	1	cj	
O06	Cabides, lixeiras, acessórios	Cabides de madeira, lixeiras, cesto de roupa, kit de costura, guarda-chuva	Geral	1	cj	
O07	Sinalização e papeleria Zion	Placas, diretório de serviços, QR de automação, cartões	Geral	1	cj	
O08	Kit de segurança	Extintor, detector de fumaça, lanterna, kit primeiros socorros	Geral	1	cj	
D01	Espreguiadeiras	Par de espreguiadeiras em madeira teca e corda náutica, almofadas outdoor	Deck	1	par	
D02	Mesa e cadeiras de deck	Mesa redonda Ø0,80 + 2 cadeiras em madeira e corda náutica	Deck	1	cj	
D04	Balizadores e lanternas de deck	Lanternas portáteis LED recarregáveis + tochas de citronela	Deck	1	cj	
D05	Ducha externa	Ducha de deck em aço inox com base de cumaru	Deck	1	un	
E07	Hidromassagem externa	Hot tub de 4 lugares, fibra, aquecimento a gás/elétrico, cobertura térmica	Deck	1	un	opcional: hot tub Ø1,90 no deck · opcional
B01	Acessórios do banho	Toalheiros aquecidos, ganchos, saboneteiras e porta-papel em latão escovado	Banho	1	cj	
B02	Banqueta e bandeja da banheira	Banqueta de teca e bandeja para banheira	Banho	1	cj	banheira 1,60
B03	Balança e acessórios	Balança digital, secador de toalhas, kit de manicure	Banho	1	cj	

PRÓXIMAS CABANAS

a mesma lógica de marcenaria acoplada aplicada às outras cinco unidades

UNIDADE	PROGRAMA DE MARCENARIA ACOPLADA PREVISTO
Safari (ZS)	cabeceira acoplada ao totem do mastro M2, Ilha do Café como peça central, closet em L, bancada dupla
Lodge 38 (ZL)	parede-corda ripada como cabeceira, closet e café nas faces opacas, bancada e banheira de sentar
Lodge 24 e 28	versões compactas: café/closet em uma face opaca, cabeceira na parede do banho
Cápsula (ZK)	marcenaria curva acoplada aos anéis: cabeceira na parede do banho, café e closet nas laterais, bancada no técnico

Cada unidade receberá o mesmo conjunto: planta de layout de interiores, paginação, elevações internas, detalhes de marcenaria e quadros (IN-01 a IN-06), com códigos ZS-INT, ZL-INT, ZL24-INT, ZL28-INT e ZK-INT.

REV	DATA	DESCRIÇÃO	AUTOR
00	17/09/2026	Conceito · emissão inicial do projeto de interiores do Casulo com marcenaria acoplada	Zion Cabin Design System