



ZION

HOTEL GROUP
INTERNATIONAL

ZION GLAMPING COLLECTION · ZION CASULO · LOTE 4 DE 4

LOTE 4 MOBÍLIAS

ZC-LOT4-001 · REV 00 — CONCEITO · 17/09/2026

ZION CASULO · Cabana biomórfica em casulo · 9,60 x 6,00 x 4,20 m · Bico em balanço 2,40 m. Marcenaria acoplada, mobiliário solto, equipamentos, enxoval e OS&E. Documento de contratação separado, pensado para fabricação no Brasil e montagem modular em sítios de montanha: peças transportáveis, ligações parafusadas, sem concreto e sem solda em campo.

48,0 m²

INTERNOS

29,9 m²

DECK

12 dias

MONTAGEM (4 + LÍDER)

4 lotes

DECK · FERRO · LONA E VIDRO · MOBÍLIA

Documento de contratação e fabricação. Nenhuma especificação que dependa de cálculo estrutural ou norma foi inventada: onde há dependência, o item está marcado

⚠️ VALIDAÇÃO OBRIGATÓRIA — ENGENHEIRO/ARQUITETO Sem preços: PREÇO A COTAR Projeto preliminar / executivo conceitual: não substitui ART, RRT, cálculo, projeto legal ou aprovação municipal.

ÍNDICE

CÓDIGO	SEÇÃO	PÁG.
ZC-LOT4-001	Escopo do lote 4	2
ZC-MOB-001	Marcenaria acoplada	3

ZC-MOB-002	Mobiliário solto	4
ZC-FFE-001	FF&E e equipamentos	5
ZC-MONT-L4	Sequência do lote 4	10
ZC-LOT4-RFQ	RFQ do lote 4	11

LOTE 4 · MOBÍLIAS · ESCOPO E INTERFACES

ZION CASULO · Cabana biomórfica em casulo · 9,60 x 6,00 x 4,20 m · Bico em balanço 2,40 m

O QUE ESTE LOTE INCLUI

Marcenaria acoplada (MA): peças fixas fabricadas em fábrica com gabaritos da estrutura, montadas e acabadas antes do embarque

Mobiliário solto (MS) e FF&E Zion New Luxury: cama, chaise, sofá, poltronas, mesas, luminárias, tapetes, cortinas, arte

Equipamentos: mini cozinha / café (cooktop de indução, forno, geladeira, air fryer, cafeteira), cofre, som, fechadura digital, automação, secador

Louças, metais e banheira (fornecimento; instalação no lote 1/3 conforme o manual)

Enxoval, amenities, OS&E, sinalização e kit de segurança

O QUE NÃO INCLUI (outros lotes)

Piso, deck e instalações: lote 1

Estrutura: lote 2

Lona, forro e vidros: lote 3

FORNECEDOR-TIPO

Marcenaria com CNC e experiência em peças curvas + fornecedores de FF&E (curadoria Zion) + instalador de equipamentos.

O QUE ESTE LOTE ENTREGA AOS SEGUINTES

À operação: unidade mobiliada, inventário fotografado, manual do hóspede e do operador

O QUE ESTE LOTE RECEBE DOS ANTERIORES

Do lote 2: talões / cantoneiras nos arcos para a marcenaria acoplada; gabarito da seção da concha

Do lote 3: forro fechado e envelope estanque; requadros dos Olhos

Do lote 1: pontos de água, esgoto, tomadas dedicadas (cooktop, forno), dutos

REGRAS DE MODULARIDADE (SÍTIOS DE MONTANHA)

REGRA	APLICAÇÃO
Transporte	Tudo o que chega ao sítio cabe num caminhão 3/4 (caçamba 4,8 x 2,2 m) e, do último ponto de estrada, numa pícape 4x4 ou carreta agrícola: nenhuma peça > 4,80 m; volumes ≤ 2,4 x 1,2 x 1,2 m; a Cápsula é a exceção (viaja inteira em prancha) e exige acesso de caminhão até 30 m do pouso.
Peso	Peça ≤ 60 kg = 2 pessoas; ≤ 120 kg = 4 pessoas ou tripé com talha 1 t; nada exige guindaste. Vidro ≤ 90 kg por pano (ventosas, 4 pessoas).
Sem concreto e sem solda em campo	Fundação em estacas helicoidais cravadas com motor hidráulico portátil (ou sapatas pré-moldadas onde há rocha); todas as ligações parafusadas classe 8.8 galvanizadas; galvanização a fogo em fábrica.
Kit numerado	Cada peça leva etiqueta com código do projeto (ex.: ZC-B03-C), peso e posição; cada estrado traz a lista de conteúdo; a montagem segue a sequência A → B → C → D → E das listas.
Ferramenta mínima	Torquímetros 20-250 N·m, chaves 19/24 mm, nível a laser, estação total ou trena a laser, tripé com talha, esticadores, puxador de keder, soprador térmico, parafusadeira. Gerador 5 kVA para o sítio.
Reversível	A unidade desmonta na ordem inversa e sai do sítio sem deixar fundação: estacas removidas, solo recomposto.
Clima de montanha	Vento: suspender içamentos e lona acima de 30 km/h; membrana e cabos tensionados com pré-tensão medida; drenagem para o terreno inclinado; isolamento e água quente dimensionados para 0 °C; cabeçotes ajustáveis absorvem declive até 15 % (ver DET-04).
Interfaces travadas	Cada lote entrega ao seguinte uma geometria conferida (planilha de as-built): fundação ± 30 mm → grelha ± 10 mm → estrutura ± 15 mm no topo → lona sem rugas → marcenaria com gabarito.

MARCENARIA ACOPLADA · MA-01 A MA-08

peças fixas fabricadas com a cabana; fundos recortados conforme a seção da concha (gabarito dos arcos A1 a A4); fixação por cantoneiras nos arcos, nunca na membrana

CÓD.	PEÇA	DIMENSÕES (M)	AMB.	FF&E	DESCRIÇÃO	MATERIAIS
MA-01	Mini cozinha acoplada	2,00 x 0,65 x h 0,90	Estar	M18 · E13 · E14 · E15 · E16 · E17 · E02	Gabinete de 2,00 m acoplado à curva da concha (fundo recortado conforme a seção), em 4 módulos de 0,60 / 0,60 / 0,40 / 0,40; geladeira 120 L sob bancada · forno elétrico compacto 45 L sob o cooktop de indução 2 bocas · cuba 0,40 x 0,35 com torneira gourmet sobre gaveteiro · bancada de preparo com air fryer em nicho e lixeira embutida; tampo em quartzito 30 mm; prateleira flutuante 2,00 x 0,25 a 1,45 m com fita LED e depurador slim 60 cm (filtro de carvão) sob a prateleira; cafeteira e chaleira sobre o tampo	Carvalho natural (portas ripadas) · quartzito · latão escovado · inox
MA-02	Armário baixo / closet embutido	1,10 x 0,65 x h 1,50	Estar / suite	M10 · E03	Armário de 1,10 m com 2 portas ripadas, cabideiro 0,80 m, 3 prateleiras, gaveta e cofre; tampo em pedra com bandeja; tampo posterior inclinado acompanhando a concha	Carvalho natural · ripado termotratado · quartzito
MA-03	Cabeceira acoplada com criados suspensos	0,18 x 3,10 x h 1,30	Suite	M02 · M03 · M16 · F01	Painel curvo estofado em linho 2,60 x 1,30 m fixado à parede do banho, criados suspensos 0,60 x 0,50 a 0,15 m do piso (gaveta com toque), arandelas de leitura, USB e LED de retroiluminação; ripado termotratado da cabeceira até o forro (2,60 m)	Estofado linho · madeira laminada · ripado termotratado · latão
MA-04	Bancada do banho	0,55 x 1,50 x h 0,85	Banho	M12 · M13 · B01	Tampo em pedra 30 mm com cuba esculpida, saia 60 mm, gabinete ripado suspenso (base a 0,25 m) com 2 portas e nicho aberto; espelho Ø0,90 com LED perimetral e antiembaçante; nicho lateral em pedra	Quartzito · ripado termotratado · latão escovado
MA-05	Prateleira e nicho da banheira	1,10 x 0,36 x h 0,60	Banho	B02	Prateleira em pedra 1,10 x 0,36 m a 0,60 m, acoplada à curva da cauda sobre a banheira; nicho para velas e amenities; banqueta e bandeja	Quartzito · madeira
MA-06	Divisória da bacia e painel ripado	0,05 x 0,95 x h 1,20	Banho	M16	Painel ripado de 1,20 m que separa a bacia da circulação, com nicho de papel e apoio; painel ripado contínuo na face do banho da parede divisória	Ripado termotratado sobre placa cimentícia
MA-07	Rodapé técnico removível	8,50 x — x h 0,15	Todos	—	Rodapé de 150 mm em ripado ao longo de toda a concha, removível (fixação por cliques) para acesso a eletrodutos, PEX e caixas de passagem; admissão da câmara ventilada	Ripado termotratado · cliques inox
MA-08	Tampa do ático técnico	0,60 x 0,60 x h 0,00	Banho (forro)	E11	Alçapão 0,60 x 0,60 no forro do banho (2,40 m) com escada retrátil: acesso a QDC, evaporadora e boiler	Compensado naval + ripado

MOBILIÁRIO SOLTO · MS-01 A MS-09

entregue montado; passa pela porta PV1 (1,00 x 2,40): módulos ≤ 0,95 m de largura

CÓD.	PEÇA	DIMENSÕES (M)	AMB.	FF&E	POSIÇÃO
MS-01	Cama king box	1,93 x 2,03 x 0,55	Suíte	M01 · O01	pés para a fachada, cabeceira em MA-03
MS-02	Banco aos pés da cama	1,40 x 0,40 x 0,45	Suíte	M11	x 4,05
MS-03	Chaise de contemplação	1,60 x 0,80 x 0,45	Estar	M06	junto à fachada de vidro, lado direito
MS-04	Poltrona de leitura	0,70 x 0,70 x 0,75	Estar	M07	sob o Olho do estar (dir.)
MS-05	Mesa lateral	Ø0,56 x 0,45	Estar	M08	entre a chaise e a poltrona
MS-06	Luminária de piso · de mesa	—	Estar	F02 · F03	ao lado da poltrona · sobre MA-02
MS-07	Tapetes de lã	2,00 x 3,00 · 1,60 x 2,30	Estar · suíte	F04 · F05	sob a chaise/poltrona · sob a cama
MS-08	Lareira ecológica	0,60 x 0,30 x 0,35	Estar	E08	sobre MA-02 (opcional)
MS-09	Banqueta e bandeja da banheira	0,45 x 0,30 x 0,45	Banho	B02	ao lado da banheira

FF&E, EQUIPAMENTOS, ENXOVAL E OS&E

50 itens · quantidades por unidade · Zion New Luxury · sem preços (PREÇO A COTAR)

MOBILIÁRIO

CÓD.	ITEM	ESPECIFICAÇÃO	UN.	QTD	AMBIENTE
M01	Cama king box + colchão	Box 1,93 x 2,03 revestido em linho, colchão molas ensacadas 32 cm, pillow top	un	1	Suíte
M02	Cabeceira estofada	Painel curvo em madeira laminada com estofado em linho, integrado à marcenaria	un	1	Suíte · cabeceira curva sob a Espinha de Luz
M03	Criado-mudo suspenso	Carvalho natural, gaveta com fecho toque, iluminação embutida	un	2	Suíte
M11	Banco aos pés da cama	Banco 1,40 m em madeira e couro	un	1	Suíte
M16	Ripado da cabeceira	Painel ripado termotratado com fitas LED (parede da cabeceira)	m2	12	Suíte / banho · parede da cabeceira
M06	Chaise de contemplação	Chaise 1,60 x 0,80 em madeira e corda náutica, almofada impermeável	un	1	Estar · junto à fachada de vidro
M07	Poltrona de leitura	Poltrona giratória em couro natural e madeira	un	1	Estar
M08	Mesa de centro / lateral	Tampo em pedra (quartzito) sobre base de madeira torneada	un	1	Estar · mesa lateral Ø0,56
M18	Mini cozinha acoplada	Marcenaria sob medida 2,00 m acoplada à concha: tampo em quartzito, cuba, módulos para geladeira, forno, gaveteiro e lixeira, prateleira com LED (Casulo)	un	1	Estar · mini cozinha 2,00 m
M10	Closet / armário	Marcenaria em carvalho com portas ripadas, cabideiro, prateleiras e cofre	un	1	Estar · armário baixo embutido 1,10 m
M12	Bancada do banho	Tampo em pedra com cuba esculpida, gabinete ripado suspenso	un	1	Banho · bancada 1,50 m
M13	Espelho com iluminação	Espelho redondo Ø0,90 com LED perimetral e antiembaçante	un	1	Banho

LUMINÁRIAS E DECORAÇÃO

CÓD.	ITEM	ESPECIFICAÇÃO	UN.	QTD	AMBIENTE
F01	Arandela de leitura	Arandela articulada em latão escovado, LED 2700 K dimerizável	un	2	Suíte
F02	Luminária de piso	Luminária de piso em madeira e linho, 2700 K	un	1	Estar
F03	Luminária de mesa	Abajur cerâmico artesanal, 2700 K	un	1	Estar
F04	Tapete de lã	Tapete de lã tecido à mão 2,00 x 3,00	un	1	Estar
F05	Tapete de lã (pequeno)	Tapete de lã 1,60 x 2,30	un	1	Suíte
F06	Cortinas e blackout	Cortina de linho + blackout motorizado, por metro linear de fachada de vidro	m	6,5	Fachada · 6,50 m de fachada de vidro
F07	Cortina da lanterna / óculo	Tela de sombreamento motorizada circular	un	1	Espinha de Luz · tela de sombreamento 0,70 x 4,70
F08	Arte e objetos	Curadoria Zion: peças de artesanato regional, cerâmica, vasos, livros	vb	1	Geral
F10	Plantas e vasos	Plantas de interior em vasos de cerâmica	vb	1	Geral

EQUIPAMENTOS

CÓD.	ITEM	ESPECIFICAÇÃO	UN.	QTD	AMBIENTE
E16	Geladeira sob bancada	Refrigerador 120 L sob bancada com congelador, classe A, silencioso (< 40 dB), porta com painel ripado	un	1	Mini cozinha · sob bancada
E13	Cooktop de indução 2 bocas	Cooktop de indução 2 zonas, 30 x 52 cm, 3,5 kW, 220 V, embutido no tampo	un	1	Mini cozinha · circuito dedicado C13
E14	Forno elétrico compacto	Forno elétrico de embutir 45 L, 60 cm, 1,8 kW, porta de vidro duplo, 220 V	un	1	Mini cozinha · circuito dedicado C14

E15	Air fryer	Fritadeira sem óleo 5 L, 1,5 kW, em nicho ventilado sobre o tampo	un	1	Mini cozinha
E17	Depurador de ar slim	Depurador 60 cm com filtro de carvão ativado, 2 velocidades, LED, recirculação	un	1	Mini cozinha
E02	Cafeteira de cápsulas + chaleira	Cafeteira de cápsulas premium e chaleira elétrica de pescoço de gancho	cj	1	Mini cozinha
E03	Cofre eletrônico	Cofre digital 20 L para notebook	un	1	Armário
E04	Caixa de som / rádio	Sistema de som Bluetooth de mesa	un	1	Estar
E06	Secador de cabelo	Secador profissional 2000 W com suporte	un	1	Banho
E08	Aquecedor / lareira ecológica	Lareira a etanol de mesa ou de piso (inverno)	un	1	Estar
E10	Fechadura eletrônica	Fechadura digital com cartão/senha na porta principal	un	1	Porta PV1
E11	Termostato e automação de cenas	Central de automação (cenas de luz, cortinas, clima, som)	un	1	Ático técnico
E07	Hidromassagem externa	Hot tub de 4 lugares, fibra, aquecimento a gás/elétrico, cobertura térmica	un	1	Deck · opcional: hot tub Ø1,90 no deck

ENXOVAL E OS&E

CÓD.	ITEM	ESPECIFICAÇÃO	UN.	QTD	AMBIENTE
O01	Enxoval de cama	3 jogos: lençóis 400 fios algodão egípcio, edredom, duvet, protetor, 6 travesseiros	cj	1	Suíte
O02	Enxoval de banho	3 jogos: toalhas de banho/rosto/piso 600 g/m2, roupões, chinelos	cj	1	Banho
O03	Amenities	Dispensers de vidro (shampoo, condicionador, sabonete, hidratante) + kit de boas-vindas (estoque inicial)	cj	1	Banho
O04	Louças, talheres e copos	Serviço para 4 (café da manhã e taças de vinho), bandeja, cesta	cj	1	Mini cozinha
O09	Utensílios de cozinha	Jogo de panelas para indução, frigideira, tábua, facas, utensílios, escorredor, potes	cj	1	Mini cozinha
O05	Manta, almofadas e decoração têxtil	Manta de lã, 6 almofadas, cortina de banho em linho	cj	1	Geral
O06	Cabides, lixeiras, acessórios	Cabides de madeira, lixeiras, cesto de roupa, kit de costura, guarda-chuva	cj	1	Geral
O07	Sinalização e papeleria Zion	Placas, diretório de serviços, QR de automação, cartões	cj	1	Geral
O08	Kit de segurança	Extintor, detector de fumaça, lanterna, kit primeiros socorros	cj	1	Geral

DECK E EXTERIOR


CÓD.	ITEM	ESPECIFICAÇÃO	UN.	QTD	AMBIENTE
D01	Espreguiçadeiras	Par de espreguiçadeiras em madeira teca e corda náutica, almofadas outdoor	par	1	Deck
D02	Mesa e cadeiras de deck	Mesa redonda Ø0,80 + 2 cadeiras em madeira e corda náutica	cj	1	Deck
D04	Balizadores e lanternas de deck	Lanternas portáteis LED recarregáveis + tochas de citronela	cj	1	Deck
D05	Ducha externa	Ducha de deck em aço inox com base de cumaru	un	1	Deck

BANHO (ACESSÓRIOS)

CÓD.	ITEM	ESPECIFICAÇÃO	UN.	QTD	AMBIENTE
B01	Acessórios do banho	Toalheiros aquecidos, ganchos, saboneteiras e porta-papel em latão escovado	cj	1	Banho
B02	Banqueta e bandeja da banheira	Banqueta de teca e bandeja para banheira	cj	1	Banho · banheira 1,60
B03	Balança e acessórios	Balança digital, secador de toalhas, kit de manicure	cj	1	Banho

ZION CASULO · PLANTA DE LAYOUT DE INTERIORES

Marcenaria acoplada (MA) e mobiliário solto (MS) · cotas de mobiliário e circulação · 1:50

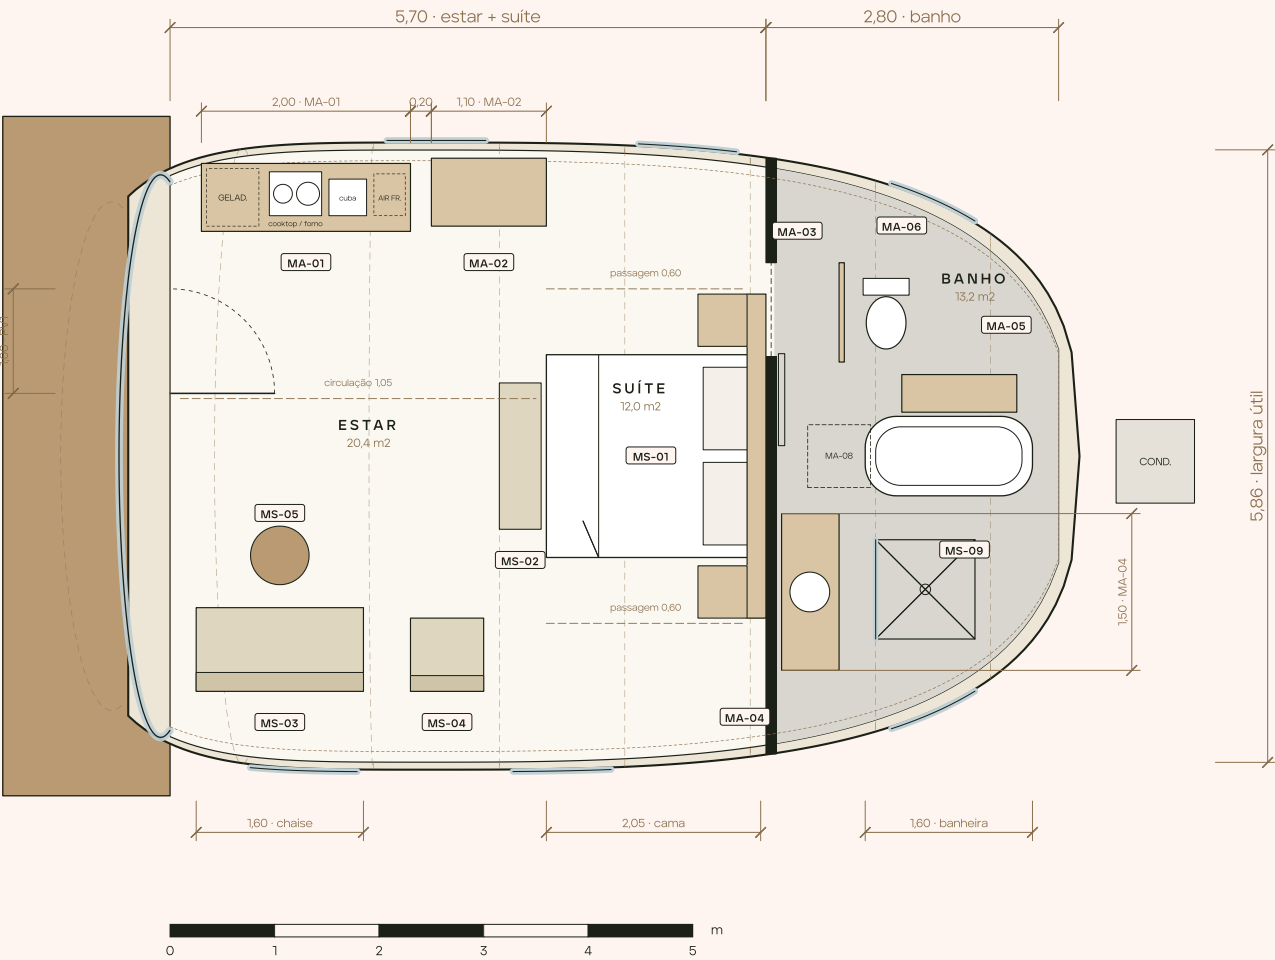

LEGENDA

- MA · marcenaria acoplada (fixa, fabricada com a cabana)
- MS · mobiliário solto (FF&E, entregue montado)
- MA-07 · rodapé técnico removível 150 mm

MARcenARIA ACOPLADA

- MA-01 Mini cozinha acoplada · Estar
- MA-02 Armário baixo / closet embutido · Estar / suíte
- MA-03 Cabeceira acoplada com criados suspensos · Suíte
- MA-04 Bancada do banho · Banho
- MA-05 Prateleira e nicho da banheira · Banho
- MA-06 Divisória da bacia e painel ripado · Banho
- MA-07 Rodapé técnico removível · Todos
- MA-08 Tampa do ático técnico · Banho (forro)


MOBILIÁRIO SOLTO

- MS-01 Cama king box · 1,95 x 2,03 x 0,55
- MS-02 Banco aos pés da cama · 1,40 x 0,40 x 0,45
- MS-03 Chaise de contemplação · 1,60 x 0,80 x 0,45
- MS-04 Poltrona de leitura · 0,70 x 0,70 x 0,75
- MS-05 Mesa lateral · Ø0,56 x 0,45
- MS-06 Luminária de piso · de mesa —
- MS-07 Tapetes de lã · 2,00 x 3,00 · 1,60 x 2,30
- MS-08 Lareira ecológica · 0,60 x 0,30 x 0,35
- MS-09 Banqueta e bandeja da banheira · 0,45 x 0,30 x 0,45


 ZION HOTEL GROUP INTERNATIONAL	PLANTA DE LAYOUT DE INTERIORES Marcenaria acoplada MA-01 a MA-08 · mobiliário solto MS-01 a MS-09	
	ZION CASULO ZION GLAMPING COLLECTION	ESCALA 1:50 (A1) · cotas em metros FOLHA IN-01 PROJETO CONCEITUAL · ESTUDO PRELIMINAR SET 2026

ZION CASULO · ELEVAÇÕES INTERNAS A E B
A · parede da cabeceira (olhar +x) · B · lateral esquerda: mini cozinha, armário e Olhos (olhar +y) · 1:40

ELEVAÇÃO A · CABECEIRA · x = 6,60

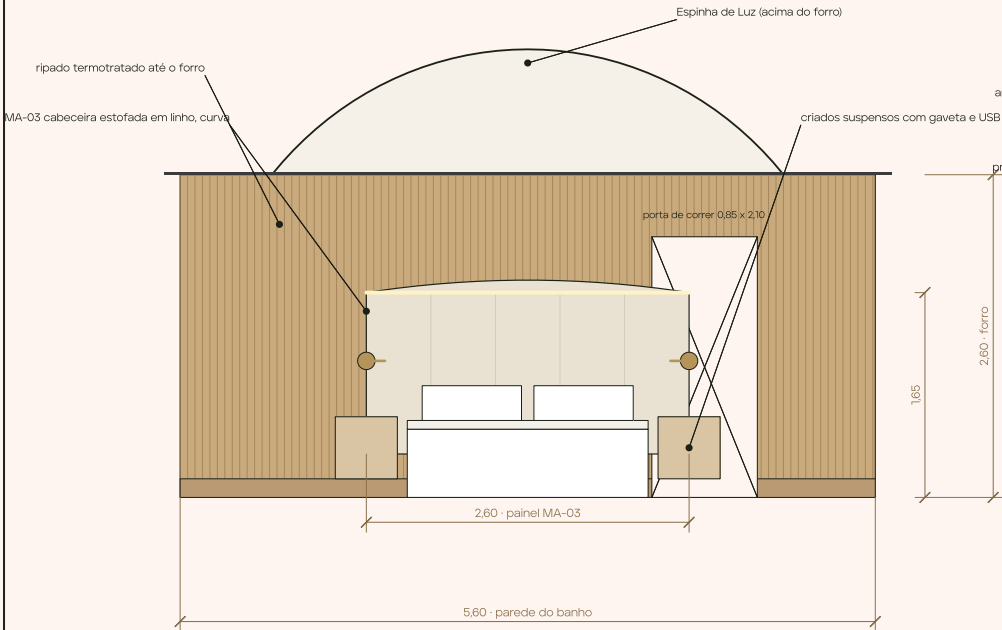


ELEVAÇÃO B · LATERAL ESQUERDA · y = +2,90

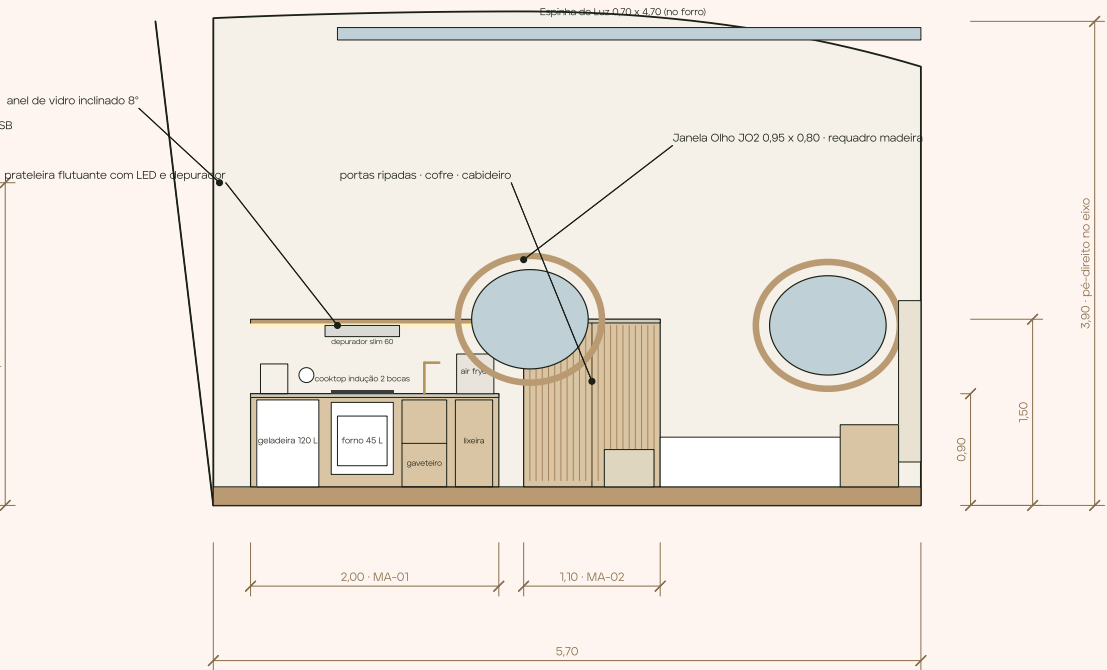


 ZION HOTEL GROUP INTERNATIONAL	ELEVAÇÕES INTERNAS A E B Cabeceira acoplada MA-03 · mini cozinha MA-01 · armário MA-02
ZION CASULO ZION GLAMPING COLLECTION	ESCALA 1:40 (A1) · cotas em metros FOLHA IN-03 PROJETO CONCEITUAL · ESTUDO PRELIMINAR SET 2026

ZION CASULO · DETALHES DA MARCENARIA ACOPLADA

MA-01 mini cozinha · MA-03 cabeceira e criado · MA-04 bancada do banho · MA-02 armário na curva · 1:20 e 1:10

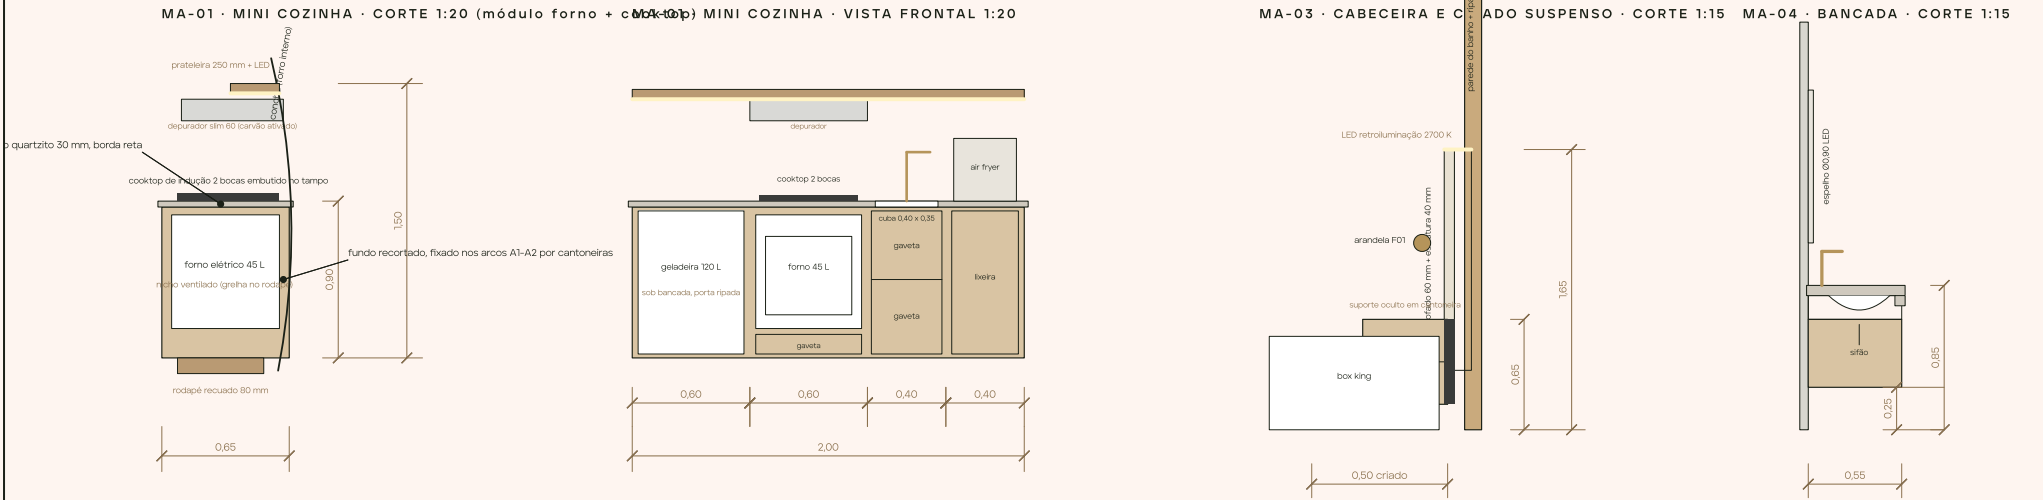

MA-02 · ARMÁRIO ACOPLADO À CURVA · CORTE 1:20

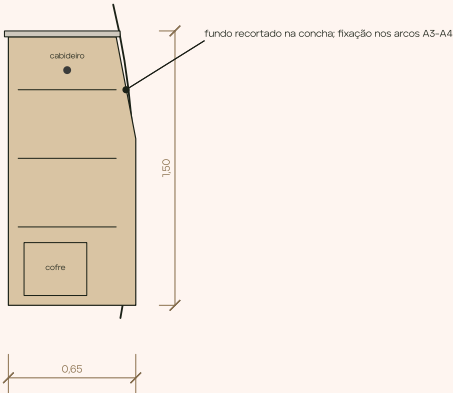

- NOTAS DE MARCENARIA ACOPLADA**
- Toda a marcenaria MA é fabricada em fábrica, montada e acabada antes do embarque; em campo só se nivela e se fixa.
 - Fixação à estrutura: cantoneiras de aço galvanizado parafusadas aos arcos (nunca à membrana); fundos recortados com folga de 15 mm para a concha e fechados com perfil de EPDM.
 - Madeira: carvalho natural em lâmina sobre MDF naval 18 mm; ripado termotratado 20 x 40; verniz PU fosco 2 demãos.
 - Pedra: quartzito 30 mm, bordas retas polidas; cubas esculpidas com impermeabilização de fábrica.
 - Ferragens: dobradiças e corredeiras com amortecimento; puxadores cava ou em latão escovado; fitas LED 2700 K IP20 (IP65 no banho) com perfil difusor.
 - Elétrica embutida na marcenaria: cooktop (C13, 20 A) e forno (C14, 16 A) em circuitos dedicados, tomadas da mini cozinha (C5), USB nos criados; passagem pelo rodapé técnico MA-07; cuba com AF/AQ Ø20 e sifão Ø50.
 - Tolerâncias: ± 3 mm nas dimensões; conferência com gabarito da seção da concha antes da fabricação (arcos A1 a A4).

ZIONHOTEL GROUPINTERNATIONAL ZION CASULO ZION GLAMPING COLLECTION	DETALHES DA MARCENARIA ACOPLADA MA-01 mini cozinha · MA-02 · MA-03 · MA-04	
	ESCALA 1:20 / 1:10 (A1) PROJETO CONCEITUAL · ESTUDO PRELIMINAR	FOLHA IN-05 SET 2026

ZION CASULO · QUADRO DE MOBILIÁRIO E MARCENARIA

Marcenaria acoplada (MA) com descrição, dimensões, materiais e FF&E relacionado · mobiliário solto (MS) · 1:50 na planta IN-01

MARCENARIA ACOPLADA

CÓD.	PEÇA	DIMENSÕES (M)	AMB.	FF&E	DESCRIÇÃO	MATERIAIS / ACABAMENTO
MA-01	Mini cozinha acoplada	2,00 x 0,65 x h 0,90	Estar	M18 · E13 · E14 · E16 · E18 · E17 · E02	Gabinete de 2,00 m acoplado à curva da concha (fundo recortado conforme a seção), em 4 módulos de 0,60 / 0,60 / 0,40 / 0,40; geladeira 120 L sob bancada · forno elétrico compacto 45 L sob o cooktop de indução 2 bocas · cuba 0,40 x 0,35 com torneira gourmet sobre gaveteiro · bancada de preparo com air fryer em nicho e lixeira embutida; tampo em quartzito 30 mm; prateleira flutuante 2,00 x 0,25 a 1,45 m com fita LED e depurador slim 60 cm (filtro de carvão) sob a prateleira; cafeteira e chaleira sobre o tampo	Carvalho natural (portas ripadas) · quartzito · latão escovado · inox
MA-02	Armário baixo / closet embutido	1,10 x 0,65 x h 1,50	Estar / suíte	M10 · E03	Armário de 1,10 m com 2 portas ripadas; cabideiro 0,80 m; 3 prateleiras; gaveta e cofre; tampo em pedra com bandeja; tampo posterior inclinado acompanhando a concha	Carvalho natural · ripado termotratado · quartzito
MA-03	Cabeceira acoplada com criados suspensos	0,18 x 3,10 x h 1,30	Suíte	M02 · M03 · M16 · F01	Palmei curvo estofado em linho 2,60 x 1,30 m fixado à parede do banho; criados suspensos 0,60 x 0,50 a 0,15 m do piso (gaveta com toque), arandelas de leitura, USB e LED de retroiluminação; ripado termotratado da cabeceira até o forro (2,60 m)	Estofado linho · madeira laminada · ripado termotratado · latão
MA-04	Bancada do banho	0,55 x 1,50 x h 0,85	Banho	M12 · M13 · B01	Tampo em pedra 30 mm com cuba esculpida, sala 60 mm; gabinete ripado suspenso (base a 0,25 m) com 2 portas e nicho aberto; espelho Ø0,90 com LED perimetral e antiembaçante; nicho lateral em pedra	Quartzito · ripado termotratado · latão escovado
MA-05	Prateleira e nicho da banheira	1,10 x 0,36 x h 0,60	Banho	B02	Prateleira em pedra 1,10 x 0,36 m a 0,60 m; acoplada à curva da cauda sobre a banheira; nicho para velas e amenities; banqueta e bandeja	Quartzito · madeira
MA-06	Divisória da bacia e painel ripado	0,05 x 0,95 x h 1,20	Banho	M16	Painel ripado de 1,20 m que separa a bacia da circulação; com nicho de papel e apoio; painel ripado contínuo na face do banho da parede divisória	Ripado termotratado sobre placa cimentícia
MA-07	Rodapé técnico removível	8,50 m lineares x h 0,15	Todos	—	Rodapé de 160 mm em ripado ao longo de toda a concha, removível (fixação por cliques) para acesso a eletrodutos, PEX e caixas de passagem; admissão da câmara ventilada	Ripado termotratado · cliques inox
MA-08	Tampa do ático técnico	0,60 x 0,60	Banho (forro)	E11	Alçapão 0,60 x 0,60 no forro do banho (2,40 m) com escada retrátil: acesso a QDC, evaporadora e boiler	Compensado naval + ripado

MOBILIÁRIO SOLTO (FF&E)

CÓD.	PEÇA	DIMENSÕES (M)	AMB.	FF&E	POSIÇÃO
MS-01	Cama king box	1,93 x 2,03 x 0,55	Suíte	M01 · O01	pés para a fachada, cabeceira em MA-03
MS-02	Banco aos pés da cama	1,40 x 0,40 x 0,45	Suíte	M11	x 4,05
MS-03	Chaise de contemplação	1,60 x 0,80 x 0,45	Estar	M06	junto à fachada de vidro, lado direito
MS-04	Poltrona de leitura	0,70 x 0,70 x 0,75	Estar	M07	sob o Olho do estar (dir.)
MS-05	Mesa lateral	Ø0,56 x 0,45	Estar	M08	entre a chaise e a poltrona
MS-06	Luminária de piso · de mesa	—	Estar	F02 · F03	ao lado da poltrona · sobre MA-02
MS-07	Tapetes de lã	2,00 x 3,00 · 1,60 x 2,30	Estar · suíte	F04 · F05	sob a chaise/poltrona · sob a cama
MS-08	Lareira ecológica	0,60 x 0,30 x 0,35	Estar	E08	sobre MA-02 (opcional)
MS-09	Banqueta e bandeja da banheira	0,45 x 0,30 x 0,45	Banho	B02	ao lado da banheira

Itens de FF&E não posicionados na planta (enxoval, amenities, papelaria, kit de segurança, luminárias de deck) constam da lista completa em ffe.py / Catálogo da Linha.

ZIONHOTEL GROUPINTERNATIONAL

ZION CASULOZION GLAMPING COLLECTION

QUADRO DE MOBILIÁRIO E MARCENARIA

MA-01 a MA-08 · MS-01 a MS-09

ESCALA s/ escala (A1)FOLHA IN-06

PROJETO CONCEITUAL · ESTUDO PRELIMINARSET 2026

SEQUÊNCIA · BANHO, MÓVEIS, ACABAMENTOS E ENTREGA

etapas do manual que pertencem a este lote

ETAPA · EQUIPE · TEMPO	FERRAMENTAS E EQUIPAMENTOS	RISCOS	CHECKLIST
14 Montagem do banheiro Encanador + montador + acabamento · 1 dia	Nível, furadeira, pistola de silicone	Banheira pesada (Casulo: entra pela porta antes da marcenaria)	☐ Louças fixadas e vedadas ☐ Bancada nivelada ☐ Box e porta de correr regulados ☐ Rejuntas e silicones concluídos
15 Montagem dos móveis Marceneiro + auxiliar · 1,5 dia	Parafusadeira, nível, calços	Marcenaria embutida na curva: usar os gabaritos de fábrica	☐ Console café, armário baixo, criados fixados ☐ Cama montada; cabeceira nivelada ☐ Portas e gavetas reguladas
16 Acabamentos Equipe de acabamento (2) · 1 dia	Espátulas, lixas, aspirador, panos	Riscos em vidros e piso durante a limpeza grossa	☐ Rodapés e perfis de LED instalados ☐ Painéis ripados fixados ☐ Selantes e arremates conferidos ☐ Limpeza fina e enxoval
17 Testes finais e entrega Líder + engenheiro + operador do glamping · 4 h	Termômetro IV, tensiômetro, testador elétrico, câmera	Entregar sem registro fotográfico e sem as-built	☐ Climatização em carga por 2 h (delta de 8 °C) ☐ Pré-tensão da membrana medida e registrada ☐ Teste de chuva (mangueira) na concha / cobertura e esquadrias ☐ Manual do operador e as-built entregues; garantia iniciada

RFQ · PEDIDO DE COTAÇÃO DO LOTE 4

ZION CASULO · o que a Zion envia, o que o fornecedor devolve, critérios de aceite · PREÇO A COTAR

A ZION ENVIA

1.

Este documento (MA, MS, FF&E)
2.

Pranchas de interiores IN-01 a IN-06 (Casulo) ou programa de mobiliário e planta humanizada
3.

Gabarito da seção da concha / paredes (lote 2) para as peças acopladas
4.

Paleta de materiais e acabamentos Zion

O FORNECEDOR DEVOLVE

1.

Cotação por peça de marcenaria (com ferragens e acabamento) e por item de FF&E
2.

Prazo, amostras de lâmina, pedra e tecidos
3.

Plano de embalagem: módulos $\leq 0,95 \times 2,10$ m e ≤ 60 kg
4.

Garantia e assistência

CRITÉRIOS DE ACEITE E GARANTIA

Marcenaria: ± 3 mm; portas e gavetas reguladas; acabamento PU fosco sem marcas

FF&E conforme especificação; inventário fotografado na entrega

Equipamentos testados e com nota fiscal em nome da operação

Garantia: marcenaria 3 anos · FF&E conforme fabricante

CONDIÇÕES GERAIS

Cotação por item e total, com prazo de fabricação e validade; impostos destacados; frete até o ponto de transbordo indicado.

Amostras / protótipo de nó antes da série (quando indicado); inspeção da Zion em fábrica antes da expedição.

Etiquetagem e embalagem conforme o pacote de transporte deste lote; lista de volumes assinada.

Sem alteração de material ou bitola sem aprovação escrita da Zion e do engenheiro responsável (ART).

Preços permanecem em documento interno da Zion; este documento circula sem preços.