

# LOTE 3

## LONAS, REVESTIMENTOS E VIDROS

ZS-LOT3-001 · REV 00 — CONCEITO · 17/09/2026

ZION SAFARI · Cabana escultural de dois cumes · 9,50 x 5,40 m · cobertura 12,90 x 7,40 · cumes 5,80 / 4,60 m. Lona externa com padrões de corte, forro interno, isolamento, fixação nos ferros, esquadrias e vidros. Documento de contratação separado, pensado para fabricação no Brasil e montagem modular em sítios de montanha: peças transportáveis, ligações parafusadas, sem concreto e sem solda em campo.

48,4 m<sup>2</sup>

INTERNOS

28,0 m<sup>2</sup>

DECK

15 dias

MONTAGEM (4 + LÍDER)

4 lotes

DECK · FERRO · LONA E VIDRO · MOBÍLIA

Documento de contratação e fabricação. Nenhuma especificação que dependa de cálculo estrutural ou norma foi inventada: onde há dependência, o item está marcado

 **VALIDAÇÃO OBRIGATÓRIA — ENGENHEIRO/ARQUITETO** Sem preços: **PREÇO A COTAR** Projeto preliminar / executivo conceitual: não substitui ART, RRT, cálculo, projeto legal ou aprovação municipal.

ÍNDICE

| CÓDIGO      | SEÇÃO             | PÁG. |
|-------------|-------------------|------|
| ZS-LOT3-001 | Escopo do lote 3  | 2    |
| ZS-LON-001  | Quadro de painéis | 3    |

|             |                     |    |
|-------------|---------------------|----|
| ZS-MAT-L3   | Materiais do lote 3 | 4  |
| ZS-ESQ-001  | Vidros e esquadrias | 22 |
| ZS-MONT-L3  | Sequência do lote 3 | 23 |
| ZS-LOT3-RFQ | RFQ do lote 3       | 24 |

LOTE 3 · LONAS, REVESTIMENTOS E VIDROS · ESCOPO E INTERFACES

ZION SAFARI · Cabana escultural de dois cumes · 9,50 x 5,40 m · cobertura 12,90 x 7,40 · cumes 5,80 / 4,60 m

O QUE ESTE LOTE INCLUI

|   |
|---|
| Lona externa (membrana PVDF tipo II) confeccionada por painéis conforme os padrões de corte deste lote, com keder, bolsas e reforços |
| Forro interno tensionado (Trevira CS) por painéis, com harpão                                                                        |
| Isolamento (lã de PET / PIR), manta refletiva, barreira de vapor e câmara ventilada                                                  |
| Perfis de fixação que não viajam com a estrutura: keder, harpão, clamps, cabos de borda, esticadores                                 |
| Esquadrias e vidros: fachadas, portas, Olhos / óculo / lanterna / Visor, claraboias, com contramarcos e selantes                     |
| Instalação da lona e dos vidros por equipe especializada (instaladores de membrana + vidraceiro)                                     |

O QUE NÃO INCLUI (outros lotes)

|                                                     |
|-----------------------------------------------------|
| Estrutura e perfis que viajam soldados nela: lote 2 |
| Fundação, piso e instalações: lote 1                |
| Marcenaria e FF&E: lote 4                           |

FORNECEDOR-TIPO

Confeccionista de membranas tensionadas (corte CNC, solda HF, form-finding) + vidraceiro com vidro insulado / laminado + instaladores de membrana.

O QUE ESTE LOTE ENTREGA AOS SEGUINTES

|                                                                                         |
|-----------------------------------------------------------------------------------------|
| Ao lote 4: envelope fechado e estanque (teste de água) antes da marcenaria e do enxoval |
| Ao lote 1: descidas de água da calha ligadas aos tubos de queda                         |

O QUE ESTE LOTE RECEBE DOS ANTERIORES

|   |
|---|
| Do lote 2: geometria conferida e liberada (relatório de esquadro), perfis keder / clamps instalados |
| Do projeto: padrões DXF + XLSX, mapa de painéis LN-01, fixações LN-90, quadro de esquadrias         |

REGRAS DE MODULARIDADE (SÍTIOS DE MONTANHA)

| REGRA                             | APLICAÇÃO   |
|-----------------------------------|---|
| Transporte                        | Tudo o que chega ao sítio cabe num caminhão 3/4 (caçamba 4,8 x 2,2 m) e, do último ponto de estrada, numa pícape 4x4 ou carreta agrícola: nenhuma peça > 4,80 m; volumes ≤ 2,4 x 1,2 x 1,2 m; a Cápsula é a exceção (viaja inteira em prancha) e exige acesso de caminhão até 30 m do pouso. |
| Peso                              | Peça ≤ 60 kg = 2 pessoas; ≤ 120 kg = 4 pessoas ou tripé com talha 1 t; nada exige guindaste. Vidro ≤ 90 kg por pano (ventosas, 4 pessoas).   |
| Sem concreto e sem solda em campo | Fundação em estacas helicoidais cravadas com motor hidráulico portátil (ou sapatas pré-moldadas onde há rocha); todas as ligações parafusadas classe 8.8 galvanizadas; galvanização a fogo em fábrica.                                                                                       |
| Kit numerado                      | Cada peça leva etiqueta com código do projeto (ex.: ZC-B03-C), peso e posição; cada estrado traz a lista de conteúdo; a montagem segue a sequência A → B → C → D → E das listas.   |
| Ferramenta mínima                 | Torquímetros 20-250 N·m, chaves 19/24 mm, nível a laser, estação total ou trena a laser, tripé com talha, esticadores, puxador de keder, soprador térmico, parafusadeira. Gerador 5 kVA para o sítio.                                                                                        |
| Reversível                        | A unidade desmonta na ordem inversa e sai do sítio sem deixar fundação: estacas removidas, solo recomposto.   |
| Clima de montanha                 | Vento: suspender içamentos e lona acima de 30 km/h; membrana e cabos tensionados com pré-tensão medida; drenagem para o terreno inclinado; isolamento e água quente dimensionados para 0 °C; cabeçotes ajustáveis absorvem declive até 15 % (ver DET-04).                                    |
| Interfaces travadas               | Cada lote entrega ao seguinte uma geometria conferida (planilha de as-built): fundação ± 30 mm → grelha ± 10 mm → estrutura ± 15 mm no topo → lona sem rugas → marcenaria com gabarito.   |

QUADRO DE PAINÉIS · PADRÕES DE CORTE

6 padrões externos = 114,6 m2 · 4 internos = 67,1 m2 (forma final; acrescentar 12 a 15 % de sobras, bolsas e emendas) · geometria em <modelo>/lona/ (SVG, DXF, XLSX)

| CÓD. | QTD | GRUPO                        | PAINEL                                                                        | CAIXA (M)    | M2    | M2 TOTAL | BORDAS                  | RECORTES |
|------|-----|------------------------------|-------------------------------------------------------------------------------|--------------|-------|----------|-------------------------|----------|
| S1   | 1   | Lona Externa                 | Faixa S1 · y -3,70 a -2,47 · de x -2,40 (frente) a x 10,50 (fundos)           | 1,38 x 13,05 | 17,06 | 17,1     | BOLSA DE CABO, SOLDA HF | 0        |
| S2   | 1   | Lona Externa                 | Faixa S2 · y -2,47 a -1,23 · de x -2,40 (frente) a x 10,50 (fundos)           | 1,98 x 13,38 | 18,05 | 18       | BOLSA DE CABO, SOLDA HF | 0        |
| S3   | 1   | Lona Externa                 | Faixa S3 · y -1,23 a 0,00 · de x -2,40 (frente) a x 10,50 (fundos)            | 4,15 x 13,76 | 20,32 | 20,3     | BOLSA DE CABO, SOLDA HF | 1        |
| S4   | 1   | Lona Externa                 | Faixa S4 · y 0,00 a 1,23 · de x -2,40 (frente) a x 10,50 (fundos)             | 3,11 x 14,66 | 19,45 | 19,4     | BOLSA DE CABO, SOLDA HF | 1        |
| S5   | 1   | Lona Externa                 | Faixa S5 · y 1,23 a 2,47 · de x -2,40 (frente) a x 10,50 (fundos)             | 3,51 x 13,61 | 22,33 | 22,3     | BOLSA DE CABO, SOLDA HF | 1        |
| S6   | 1   | Lona Externa                 | Faixa S6 · y 2,47 a 3,70 · de x -2,40 (frente) a x 10,50 (fundos)             | 1,43 x 13,07 | 17,36 | 17,4     | BOLSA DE CABO, SOLDA HF | 0        |
| F1   | 1   | Forro / Revestimento Interno | Forro F1 · y -2,70 a -1,35 · sobre o corpo (x 0 a 9,5), 0,30 m sob a membrana | 1,73 x 9,79  | 14,31 | 14,3     | HARPÃO                  | 0        |
| F2   | 1   | Forro / Revestimento Interno | Forro F2 · y -1,35 a 0,00 · sobre o corpo (x 0 a 9,5), 0,30 m sob a membrana  | 3,58 x 10,56 | 17,41 | 17,4     | HARPÃO                  | 1        |
| F3   | 1   | Forro / Revestimento Interno | Forro F3 · y 0,00 a 1,35 · sobre o corpo (x 0 a 9,5), 0,30 m sob a membrana   | 3,26 x 11,15 | 16,64 | 16,6     | HARPÃO                  | 2        |
| F4   | 1   | Forro / Revestimento Interno | Forro F4 · y 1,35 a 2,70 · sobre o corpo (x 0 a 9,5), 0,30 m sob a membrana   | 2,69 x 10,35 | 18,76 | 18,8     | HARPÃO                  | 1        |

Como o padrão foi obtido: a superfície entre duas costuras (arcos, caibros, anéis ou linhas de emenda) é planificada por triangulação sequencial; o resultado é a geometria "de forma final", sem compensação. O confeccionista aplica a compensação do tecido (ensaio biaxial), as sobras de keder / bolsa e define a padronagem de rolos (largura 2,50 a 3,00 m). Painéis maiores que o rolo levam emenda HF longitudinal.

# MATERIAIS DO ENVELOPE, ISOLAMENTO E PERFIS

quantidades estimadas · sem preços

## Alumínio e perfis

| ITEM                                                 | UN. | QTD | KG | PREÇO         |
|------------------------------------------------------|-----|-----|----|---------------|
| Perfil de borda arredondado do beiral + calha oculta | un  | 1   | 48 | PREÇO A COTAR |
| Perfil de clamp dos anéis de cume                    | un  | 2   | 7  | PREÇO A COTAR |
| Trilho do forro tensionado + cabos de suspensão      | un  | 1   | 28 | PREÇO A COTAR |
| Esquadria do óculo (ruptura térmica)                 | un  | 1   | 12 | PREÇO A COTAR |

## Envelope: membrana, forro, painéis

| ITEM                                                        | UN. | QTD | KG  | PREÇO         |
|-------------------------------------------------------------|-----|-----|-----|---------------|
| Membrana PVDF 1050 g/m2 (+15% emendas/bolsas)               | m2  | 135 | 141 | PREÇO A COTAR |
| Lã de PET 50 mm + manta refletiva (forro sobre o corpo)     | m2  | 54  | 81  | PREÇO A COTAR |
| Forro tensionado Trevira CS (segue os cumes)                | m2  | 58  | 17  | PREÇO A COTAR |
| Painéis SIP 100 mm (OSB/PIR/OSB) estruturais                | m2  | 36  | 792 | PREÇO A COTAR |
| Placa cimentícia externa 10 mm + membrana hidrófuga         | m2  | 36  | 504 | PREÇO A COTAR |
| Ripado de madeira termotratada 40 x 40 mm                   | m2  | 36  | 288 | PREÇO A COTAR |
| Acabamento interno das paredes (painel de madeira / tecido) | m2  | 30  | 210 | PREÇO A COTAR |

## ESPECIFICAÇÃO DA LONA

|                |   |
|----------------|---|
| LONA EXTERNA   | PVDF tipo II 1050 g/m2 (poliéster HT 1100 dtex, PVC + laca PVDF bifacial), cor creme Zion, resistência ≥ 4.200 / 4.000 N/5 cm, classe B / M2, garantia 10 anos; opção: PTFE-vidro 800 g/m2 (30 anos, custo maior) |
| FORRO          | Trevira CS 210 g/m2 (ou lona translúcida 350 g/m2 sob claraboias), harpão de PVC soldado   |
| ISOLAMENTO     | lã de PET 50 mm 25 kg/m3 entre terças / caibros + manta refletiva com face para a câmara; PIR 60 mm na Cápsula   |
| KEDER E PERFIS | cordão keder Ø10 / Ø13 PVC; perfil duplo keder alu 6060-T5; barras de clamp 40 x 6; harpão 40 x 20; presilhas inox 304                                                                                            |
| COSTURAS       | solda de alta frequência 40 mm; nenhuma costura com linha na face externa; reforços de 150 mm em recortes e cantos                                                                                                |
| CABOS          | inox 316 7 x 19 Ø8 / Ø10 / Ø12 com terminais prensados, esticadores M12 a M20, manilhas   |

 **ZION SAFARI · MAPA DOS PAINÉIS DE LONA E REVESTIMENTO**

6 padrões externos · 4 padrões internos · costuras sobre a estrutura · códigos usados nas pranchas LN e no DXF


TIPOS DE BORDA (ver LN-90)

-  BOLSA DE CABO · cabo inox Ø12 com esticador, chapa de canto
-  SOLDA HF · emenda de fábrica, sobreposição 40 mm
-  HARPÃO · perfil de alumínio 40 x 20 nos arcos / terças / cabos

QUADRO DE PAINÉIS

| Cód. | Qtd | Caixa (m)    | Área m2 | Grupo        |
|------|-----|--------------|---------|--------------|
| S1   | 1   | 1,38 x 13,05 | 17,06   | Lona Externa |
| S2   | 1   | 1,98 x 13,38 | 18,05   | Lona Externa |
| S3   | 1   | 4,15 x 13,76 | 20,32   | Lona Externa |
| S4   | 1   | 3,11 x 14,66 | 19,45   | Lona Externa |
| S5   | 1   | 3,51 x 13,61 | 22,33   | Lona Externa |
| S6   | 1   | 1,43 x 13,07 | 17,36   | Lona Externa |
| F1   | 1   | 1,73 x 9,79  | 14,31   | Forro        |
| F2   | 1   | 3,58 x 10,56 | 17,41   | Forro        |
| F3   | 1   | 3,26 x 11,15 | 16,64   | Forro        |
| F4   | 1   | 2,69 x 10,35 | 18,76   | Forro        |

Total lona externa: 114,6 m2 de forma final (+ 12 a 15 % de sobras, bolsas e emendas)  
Total forro / revestimento interno: 67,1 m2 de forma final (+ 12 a 15 % de sobras, bolsas e emendas)

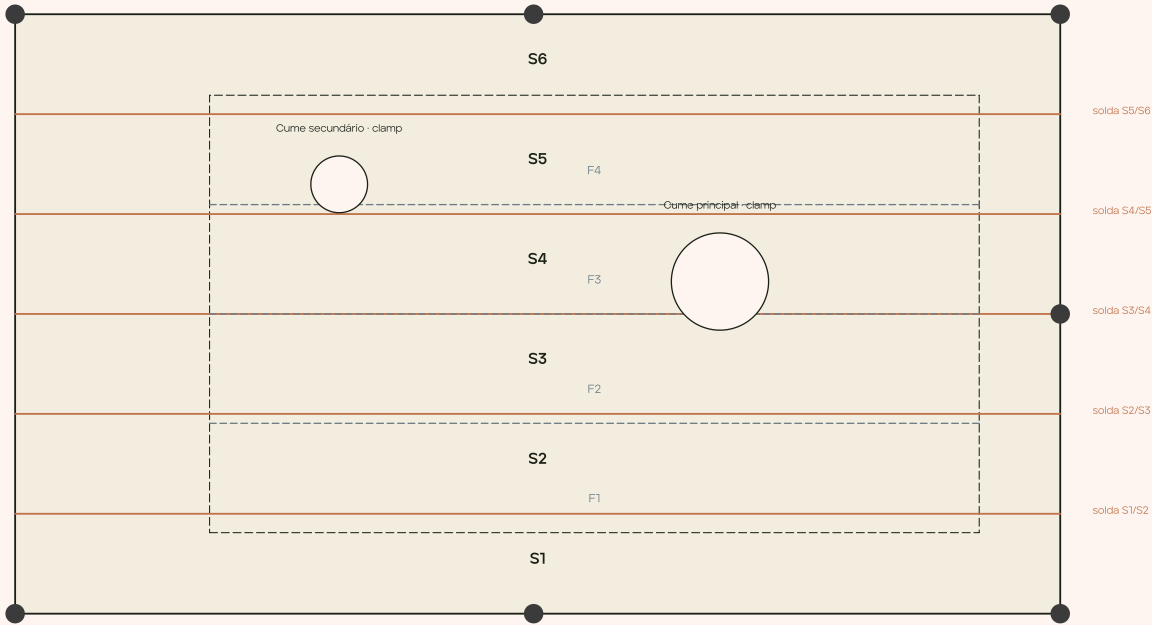

Planta da cobertura · 6 faixas longitudinais soldadas (HF) · perímetro em bolsa de cabo Ø12 com chapas de canto nos 7 postes · forro em 4 faixas sobre o corpo

|   |                                                                                     |                                |
|---|-------------------------------------------------------------------------------------|--------------------------------|
|  <b>ZION</b>   HOTEL GROUP INTERNATIONAL | <b>MAPA DOS PAINÉIS DE LONA</b><br>Costuras sobre a estrutura · códigos dos padrões |                                |
| <b>ZION SAFARI</b><br>ZION GLAMPING COLLECTION                                                                                | ESCALA s/ escala<br>PROJETO CONCEITUAL · ESTUDO PRELIMINAR                          | <b>FOLHA LN-01</b><br>SET 2026 |

ZION SAFARI · PADRÃO DE CORTE S1

Faixa S1 · y -3.70 a -2.47 · de x -2.40 (frente) a x 10.50 (fundos) · LONA EXTERNA · geometria de forma final (sem compensação) · metros

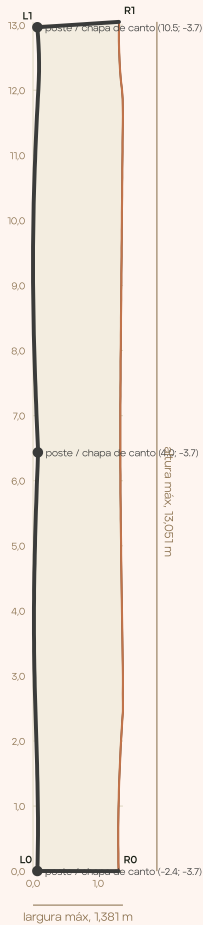


TABELA DE ESTAÇÕES (ao longo da borda L, a cada 0,50 m)

| s (m)  | xL    | yL     | xR    | yR     | largura |
|--------|-------|--------|-------|--------|---------|
| 0,000  | 0,066 | 0,001  | 1,314 | 0,000  | 1,249   |
| 0,500  | 0,075 | 0,501  | 1,309 | 0,500  | 1,234   |
| 1,000  | 0,074 | 1,001  | 1,315 | 1,002  | 1,240   |
| 1,500  | 0,065 | 1,501  | 1,329 | 1,506  | 1,264   |
| 2,000  | 0,051 | 2,001  | 1,352 | 2,013  | 1,301   |
| 2,500  | 0,036 | 2,501  | 1,381 | 2,521  | 1,345   |
| 3,000  | 0,023 | 3,000  | 1,381 | 3,021  | 1,358   |
| 3,500  | 0,016 | 3,500  | 1,373 | 3,521  | 1,358   |
| 4,000  | 0,015 | 4,000  | 1,366 | 4,020  | 1,351   |
| 4,500  | 0,019 | 4,500  | 1,359 | 4,519  | 1,340   |
| 5,000  | 0,029 | 5,000  | 1,352 | 5,017  | 1,323   |
| 5,500  | 0,044 | 5,500  | 1,347 | 5,514  | 1,303   |
| 6,000  | 0,061 | 6,000  | 1,343 | 6,008  | 1,281   |
| 6,500  | 0,075 | 6,499  | 1,341 | 6,503  | 1,266   |
| 7,000  | 0,054 | 6,999  | 1,341 | 6,996  | 1,287   |
| 7,500  | 0,035 | 7,499  | 1,344 | 7,491  | 1,309   |
| 8,000  | 0,019 | 7,998  | 1,347 | 7,988  | 1,328   |
| 8,500  | 0,008 | 8,498  | 1,352 | 8,487  | 1,344   |
| 9,000  | 0,001 | 8,998  | 1,356 | 8,986  | 1,355   |
| 9,500  | 0,000 | 9,498  | 1,361 | 9,486  | 1,360   |
| 10,000 | 0,006 | 9,998  | 1,365 | 9,986  | 1,360   |
| 10,500 | 0,017 | 10,498 | 1,369 | 10,485 | 1,353   |
| 11,000 | 0,034 | 10,998 | 1,374 | 10,984 | 1,341   |
| 11,500 | 0,055 | 11,497 | 1,379 | 11,482 | 1,324   |
| 12,000 | 0,081 | 11,997 | 1,368 | 11,985 | 1,287   |
| 12,500 | 0,091 | 12,496 | 1,325 | 12,538 | 1,235   |
| 12,972 | 0,066 | 12,968 | 1,321 | 13,051 | 1,258   |

DADOS DO PAINEL

QUANTIDADE  
1 (códigos: S1)

ÁREA DE FORMA FINAL  
17,06 m2

COMPRIMENTO L / R  
12,97 / 13,06 m

CAIXA (LARG. X ALT.)  
1,38 x 13,05 m

MATERIAL  
PVDf tipo II 1050 g/m2, creme Zion; faixas soldadas em fábrica (HF 40 mm) numa peça única de = 105 m2 (fardo = 120 kg)

BORDAS E RECORTES

- BOLSA DE CABO · cabo inox Ø12 com esticador, chapa de canto
- SOLDA HF · emenda de fábrica, sobreposição 40 mm

|                                                            |   |
|------------------------------------------------------------|---|
| <div>ZION</div> <div>HOTEL GROUP<br/>INTERNATIONAL</div>   | <div>PADRÃO DE CORTE S1</div> <div>Lona Externa</div>                                                                        |
| <div>ZION SAFARI</div> <div>ZION GLAMPING COLLECTION</div> | <div>ESCALA ver malha (m)</div> <div>PROJETO CONCEITUAL · ESTUDO PRELIMINAR</div> <div>FOLHA LN-11</div> <div>SET 2026</div> |

NOTAS

- Padrão = geometria de forma final da superfície entre as costuras; o confeccionista aplica a compensação do tecido (ensaio biaxial típico 0,5 a 1,5 % no urdume e 2 a 4 % na trama) e as sobras de bolsa/veder.
- Origem (O: 0) no canto inferior esquerdo da caixa; eixo x horizontal, y vertical; L0 → L1 é a borda esquerda (costura de referência), R0 → R1 a direita; estações medidas ao longo de L.
- Marcar em cada painel: código, modelo, orientação (L/R, base), linhas de presilha e centros dos recortes; etiqueta de tecido cosida no verso.
- Form-finding obrigatório: a superfície de dois cumes é anticiclística entre os cumes; os padrões aqui são geométricos (forma-alvo) e devem ser ajustados pelo confeccionista com compensação biaxial.

ZION SAFARI · PADRÃO DE CORTE S2

Faixa S2 · y -2.47 a -1.23 · de x -2.40 (frente) a x 10.50 (fundos) · LONA EXTERNA · geometria de forma final (sem compensação) · metros

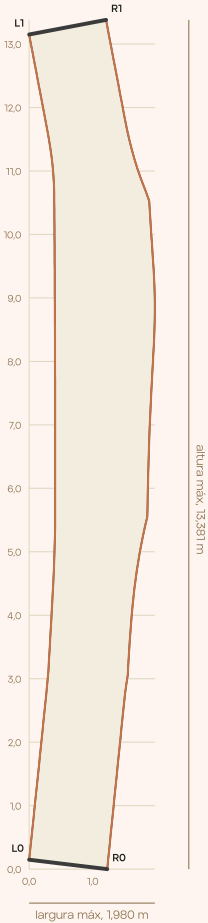


TABELA DE ESTAÇÕES (ao longo da borda L, a cada 0,50 m)

| s (m)  | xL    | yL     | xR    | yR     | largura |
|--------|-------|--------|-------|--------|---------|
| 0,000  | 0,000 | 0,149  | 1,230 | 0,000  | 1,239   |
| 0,500  | 0,052 | 0,646  | 1,281 | 0,502  | 1,237   |
| 1,000  | 0,104 | 1,143  | 1,331 | 1,003  | 1,235   |
| 1,500  | 0,155 | 1,641  | 1,382 | 1,505  | 1,234   |
| 2,000  | 0,206 | 2,138  | 1,433 | 2,008  | 1,234   |
| 2,500  | 0,257 | 2,635  | 1,484 | 2,511  | 1,233   |
| 3,000  | 0,304 | 3,133  | 1,535 | 3,063  | 1,251   |
| 3,500  | 0,332 | 3,632  | 1,583 | 3,562  | 1,253   |
| 4,000  | 0,360 | 4,132  | 1,621 | 4,064  | 1,263   |
| 4,500  | 0,385 | 4,631  | 1,678 | 4,575  | 1,294   |
| 5,000  | 0,404 | 5,131  | 1,763 | 5,100  | 1,360   |
| 5,500  | 0,410 | 5,630  | 1,863 | 5,632  | 1,453   |
| 6,000  | 0,410 | 6,130  | 1,874 | 6,132  | 1,464   |
| 6,500  | 0,410 | 6,630  | 1,888 | 6,632  | 1,478   |
| 7,000  | 0,409 | 7,130  | 1,906 | 7,133  | 1,497   |
| 7,500  | 0,409 | 7,630  | 1,931 | 7,635  | 1,522   |
| 8,000  | 0,408 | 8,130  | 1,958 | 8,136  | 1,550   |
| 8,500  | 0,406 | 8,630  | 1,978 | 8,637  | 1,572   |
| 9,000  | 0,404 | 9,130  | 1,975 | 9,137  | 1,571   |
| 9,500  | 0,401 | 9,630  | 1,949 | 9,638  | 1,547   |
| 10,000 | 0,398 | 10,130 | 1,915 | 10,140 | 1,517   |
| 10,500 | 0,395 | 10,630 | 1,844 | 10,661 | 1,450   |
| 11,000 | 0,364 | 11,129 | 1,631 | 11,289 | 1,277   |
| 11,500 | 0,289 | 11,623 | 1,503 | 11,845 | 1,235   |
| 12,000 | 0,197 | 12,115 | 1,408 | 12,345 | 1,233   |
| 12,500 | 0,103 | 12,606 | 1,315 | 12,836 | 1,233   |
| 13,000 | 0,010 | 13,097 | 1,222 | 13,327 | 1,233   |
| 13,055 | 0,000 | 13,151 | 1,212 | 13,381 | 1,233   |

DADOS DO PAINEL

- QUANTIDADE  
1 (códigos: S2)
- ÁREA DE FORMA FINAL  
18,05 m2
- COMPRIMENTO L / R  
13,06 / 13,51 m
- CAIXA (LARG. X ALT.)  
1,98 x 13,38 m
- MATERIAL  
PVDF tipo II 1050 g/m2, creme Zion; faixas soldadas em fábrica (HF 40 mm) numa peça única de = 105 m2 (fardo = 120 kg).
- BORDAS E RECORTES
- SOLDA HF · emenda de fábrica, sobreposição 40 mm
  - BOLSA DE CABO · cabo inox Ø12 com esticador, chapa de canto

|                                                            |   |
|------------------------------------------------------------|---|
| <div>ZION</div> <div>HOTEL GROUP<br/>INTERNATIONAL</div>   | <div>PADRÃO DE CORTE S2</div> <div>Lona Externa</div>                                                                        |
| <div>ZION SAFARI</div> <div>ZION GLAMPING COLLECTION</div> | <div>ESCALA ver malha (m)</div> <div>PROJETO CONCEITUAL · ESTUDO PRELIMINAR</div> <div>FOLHA LN-12</div> <div>SET 2026</div> |

- NOTAS
- Padrão = geometria de forma final da superfície entre as costuras; o confeccionista aplica a compensação do tecido (ensaio biaxial típico 0,5 a 1,5 % no urdume e 2 a 4 % na trama) e as sobras de bolsa/keder.
  - Origem (O: 0) no canto inferior esquerdo da caixa; eixo x horizontal, y vertical; L0 → L1 é a borda esquerda (costura de referência), R0 → R1 a direita; estações medidas ao longo de L.
  - Marcar em cada painel: código, modelo, orientação (L/R, base), linhas de presilha e centros dos recortes; etiqueta de tecido cosida no verso.
  - Form-finding obrigatório: a superfície de dois cumes é anticiclástica entre os cumes; os padrões aqui são geométricos (forma-alvo) e devem ser ajustados pelo confeccionista com compensação biaxial.

ZION SAFARI · PADRÃO DE CORTE S3

Faixa S3 · y -1.23 a 0.00 · de x -2.40 (frente) a x 10.50 (fundos) · LONA EXTERNA · geometria de forma final (sem compensação) · metros

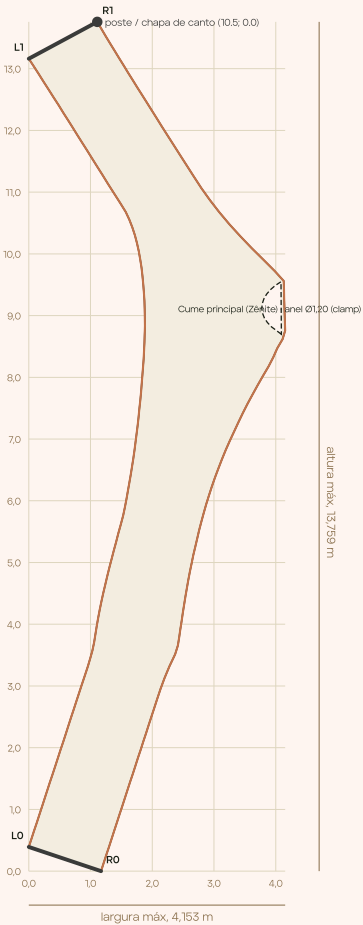


TABELA DE ESTAÇÕES (ao longo da borda L, a cada 0,50 m)

| s (m)  | xL    | yL     | xR    | yR     | largura |
|--------|-------|--------|-------|--------|---------|
| 0,000  | 0,000 | 0,391  | 1,170 | 0,000  | 1,234   |
| 0,500  | 0,155 | 0,866  | 1,326 | 0,477  | 1,234   |
| 1,000  | 0,311 | 1,342  | 1,482 | 0,954  | 1,234   |
| 1,500  | 0,466 | 1,817  | 1,637 | 1,431  | 1,233   |
| 2,000  | 0,621 | 2,292  | 1,793 | 1,908  | 1,233   |
| 2,500  | 0,776 | 2,768  | 1,949 | 2,385  | 1,233   |
| 3,000  | 0,931 | 3,243  | 2,108 | 2,872  | 1,234   |
| 3,500  | 1,081 | 3,725  | 2,376 | 3,355  | 1,329   |
| 4,000  | 1,146 | 4,218  | 2,472 | 4,035  | 1,339   |
| 4,500  | 1,253 | 4,706  | 2,549 | 4,518  | 1,309   |
| 5,000  | 1,376 | 5,191  | 2,637 | 4,987  | 1,277   |
| 5,500  | 1,506 | 5,674  | 2,741 | 5,446  | 1,256   |
| 6,000  | 1,606 | 6,163  | 2,878 | 5,954  | 1,289   |
| 6,500  | 1,688 | 6,657  | 3,059 | 6,492  | 1,380   |
| 7,000  | 1,754 | 7,152  | 3,289 | 7,045  | 1,539   |
| 7,500  | 1,807 | 7,649  | 3,561 | 7,602  | 1,754   |
| 8,000  | 1,849 | 8,148  | 3,875 | 8,164  | 2,026   |
| 8,500  | 1,877 | 8,647  | 4,136 | 8,702  | 2,260   |
| 9,000  | 1,876 | 9,147  | 4,139 | 9,203  | 2,264   |
| 9,500  | 1,841 | 9,645  | 3,976 | 9,731  | 2,137   |
| 10,000 | 1,760 | 10,139 | 3,295 | 10,429 | 1,962   |
| 10,500 | 1,602 | 10,612 | 2,740 | 11,149 | 1,259   |
| 11,000 | 1,344 | 11,040 | 2,408 | 11,667 | 1,235   |
| 11,500 | 1,077 | 11,462 | 2,127 | 12,109 | 1,234   |
| 12,000 | 0,811 | 11,886 | 1,857 | 12,540 | 1,233   |
| 12,500 | 0,545 | 12,309 | 1,595 | 12,958 | 1,234   |
| 13,000 | 0,277 | 12,731 | 1,354 | 13,349 | 1,242   |
| 13,500 | 0,007 | 13,152 | 1,114 | 13,748 | 1,258   |

DADOS DO PAINEL

- QUANTIDADE  
1 (códigos: S3)
- ÁREA DE FORMA FINAL  
20,32 m2
- COMPRIMENTO L / R  
13,51 / 15,30 m
- CAIXA (LARG. X ALT.)  
4,15 x 13,76 m
- MATERIAL  
PVDF tipo II 1050 g/m2, creme Zion; faixas soldadas em fábrica (HF 40 mm) numa peça única de = 105 m2 (fardo = 120 kg).
- BORDAS E RECORTES
- SOLDA HF · emenda de fábrica, sobreposição 40 mm
  - BOLSA DE CABO · cabo inox Ø12 com esticador, chapa de canto
  - RECORTE com anel de reforço soldado (150 mm) e clamp / requadro

NOTAS

- Padrão = geometria de forma final da superfície entre as costuras; o confeccionista aplica a compensação do tecido (ensaio biaxial típico 0,5 a 1,5 % no urdume e 2 a 4 % na trama) e as sobras de bolsa/veder.
- Origem (O: 0) no canto inferior esquerdo da caixa; eixo x horizontal, y vertical: L0 → L1 é a borda esquerda (costura de referência), R0 → R1 a direita; estações medidas ao longo de L.
- Marcar em cada painel: código, modelo, orientação (L/R, base), linhas de presilha e centros dos recortes; etiqueta de tecido cosida no verso.
- Form-finding obrigatório: a superfície de dois cumes é anticlástica entre os cumes; os padrões aqui são geométricos (forma-alvo) e devem ser ajustados pelo confeccionista com compensação biaxial.

|                                                            |   |
|------------------------------------------------------------|---|
| <div>ZION</div> <div>HOTEL GROUP<br/>INTERNATIONAL</div>   | <div>PADRÃO DE CORTE S3</div> <div>Lona Externa</div>                                                                        |
| <div>ZION SAFARI</div> <div>ZION GLAMPING COLLECTION</div> | <div>ESCALA ver malha (m)</div> <div>PROJETO CONCEITUAL · ESTUDO PRELIMINAR</div> <div>FOLHA LN-13</div> <div>SET 2026</div> |

ZION SAFARI · PADRÃO DE CORTE S4

Faixa S4 · y 0.00 a 1.23 · de x -2.40 (frente) a x 10.50 (fundos) · LONA EXTERNA · geometria de forma final (sem compensação) · metros

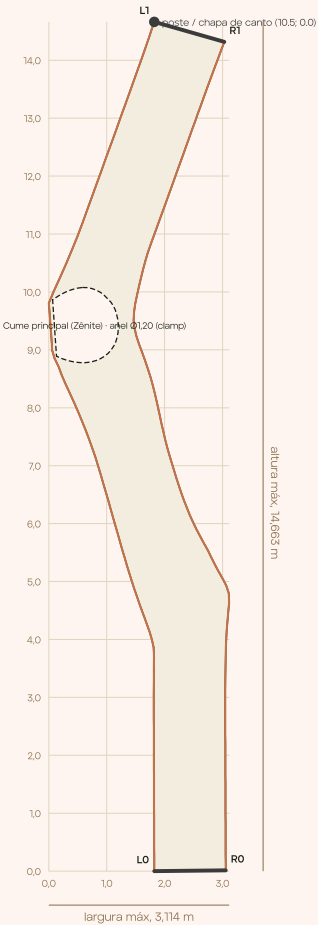


TABELA DE ESTAÇÕES (ao longo da borda L, a cada 0,50 m)

| s (m)  | xL    | yL     | xR    | yR     | largura |
|--------|-------|--------|-------|--------|---------|
| 0,000  | 1,821 | 0,000  | 3,055 | 0,013  | 1,234   |
| 0,500  | 1,819 | 0,500  | 3,053 | 0,511  | 1,234   |
| 1,000  | 1,818 | 1,000  | 3,051 | 1,009  | 1,234   |
| 1,500  | 1,816 | 1,500  | 3,050 | 1,508  | 1,233   |
| 2,000  | 1,815 | 2,000  | 3,048 | 2,006  | 1,233   |
| 2,500  | 1,813 | 2,500  | 3,047 | 2,504  | 1,233   |
| 3,000  | 1,813 | 3,000  | 3,046 | 3,026  | 1,234   |
| 3,500  | 1,815 | 3,500  | 3,053 | 3,607  | 1,242   |
| 4,500  | 1,818 | 4,469  | 3,019 | 5,016  | 1,504   |
| 5,000  | 1,454 | 4,942  | 2,781 | 5,467  | 1,427   |
| 5,500  | 1,307 | 5,419  | 2,543 | 5,916  | 1,332   |
| 6,000  | 1,169 | 5,900  | 2,352 | 6,355  | 1,267   |
| 6,500  | 1,031 | 6,381  | 2,203 | 6,786  | 1,240   |
| 7,000  | 0,892 | 6,861  | 2,073 | 7,218  | 1,234   |
| 7,500  | 0,739 | 7,337  | 1,971 | 7,615  | 1,264   |
| 8,000  | 0,559 | 7,803  | 1,884 | 8,010  | 1,341   |
| 8,500  | 0,358 | 8,261  | 1,791 | 8,399  | 1,440   |
| 9,000  | 0,163 | 8,721  | 1,659 | 8,823  | 1,500   |
| 9,500  | 0,045 | 9,201  | 1,496 | 9,308  | 1,455   |
| 10,000 | 0,008 | 9,699  | 1,499 | 9,827  | 1,496   |
| 10,500 | 0,156 | 10,167 | 1,583 | 10,203 | 1,427   |
| 11,000 | 0,358 | 10,625 | 1,651 | 10,478 | 1,302   |
| 12,000 | 0,715 | 11,558 | 1,890 | 11,180 | 1,235   |
| 12,500 | 0,885 | 12,028 | 2,053 | 11,630 | 1,234   |
| 13,000 | 1,055 | 12,499 | 2,219 | 12,089 | 1,233   |
| 13,500 | 1,224 | 12,969 | 2,386 | 12,554 | 1,233   |
| 14,000 | 1,393 | 13,440 | 2,554 | 13,024 | 1,233   |
| 14,500 | 1,562 | 13,911 | 2,732 | 13,514 | 1,235   |
| 15,000 | 1,726 | 14,383 | 2,920 | 14,021 | 1,247   |
| 15,295 | 1,821 | 14,663 | 3,031 | 14,317 | 1,258   |

DADOS DO PAINEL

QUANTIDADE  
1 (códigos: S4)

ÁREA DE FORMA FINAL  
19,45 m2

COMPRIMENTO L / R  
15,30 / 14,87 m

CAIXA (LARG. X ALT.)  
3,11 x 14,66 m

MATERIAL  
PVDF tipo II 1050 g/m2, creme Zion; faixas soldadas em fábrica (HF 40 mm) numa peça única de = 105 m2 (fardo = 120 kg).

BORDAS E RECORTES

- SOLDA HF - emenda de fábrica, sobreposição 40 mm
- BOLSA DE CABO - cabo inox Ø12 com esticador, chapa de canto
- RECORTE com anel de reforço soldado (150 mm) e clamp / requadro

|                                                            |   |
|------------------------------------------------------------|---|
| <div>ZION</div> <div>HOTEL GROUP<br/>INTERNATIONAL</div>   | <div>PADRÃO DE CORTE S4</div> <div>Lona Externa</div>                                                                        |
| <div>ZION SAFARI</div> <div>ZION GLAMPING COLLECTION</div> | <div>ESCALA ver malha (m)</div> <div>PROJETO CONCEITUAL · ESTUDO PRELIMINAR</div> <div>FOLHA LN-14</div> <div>SET 2026</div> |

NOTAS

- Padrão = geometria de forma final da superfície entre as costuras; o confeccionista aplica a compensação do tecido (ensaio biaxial típico 0,5 a 1,5 % no urdume e 2 a 4 % na trama) e as sobras de bolsa/keder.
- Origem (O: 0) no canto inferior esquerdo da caixa; eixo x horizontal, y vertical; L0 → L1 é a borda esquerda (costura de referência), R0 → R1 a direita; estações medidas ao longo de L.
- Marcar em cada painel: código, modelo, orientação (L/R, base), linhas de presilha e centros dos recortes; etiqueta de tecido cosida no verso.
- Form-finding obrigatório: a superfície de dois cumes é anticlástica entre os cumes; os padrões aqui são geométricos (forma-alvo) e devem ser ajustados pelo confeccionista com compensação biaxial.

ZION SAFARI · PADRÃO DE CORTE S5

Faixa S5 · y 1.23 a 2.47 · de x -2.40 (frente) a x 10.50 (fundos) · LONA EXTERNA · geometria de forma final (sem compensação) · metros

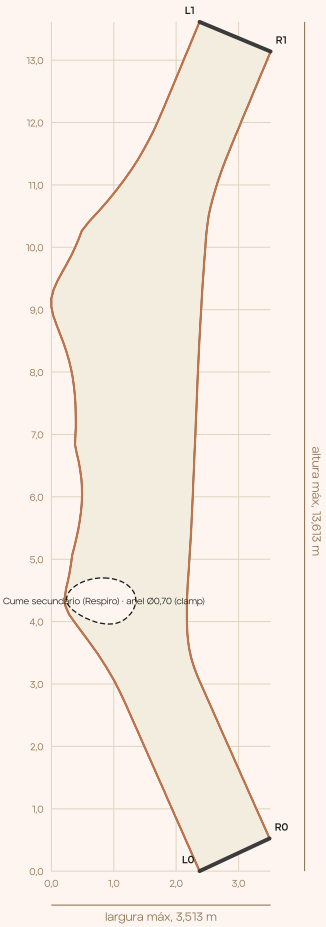


TABELA DE ESTAÇÕES (ao longo da borda L, a cada 0,50 m)

| s (m)  | xL    | yL     | xR    | yR     | largura |
|--------|-------|--------|-------|--------|---------|
| 0,000  | 2,375 | 0,000  | 3,498 | 0,523  | 1,239   |
| 0,500  | 2,173 | 0,457  | 3,296 | 0,976  | 1,237   |
| 1,000  | 1,971 | 0,914  | 3,094 | 1,429  | 1,235   |
| 1,500  | 1,768 | 1,372  | 2,892 | 1,881  | 1,234   |
| 2,000  | 1,566 | 1,829  | 2,692 | 2,334  | 1,234   |
| 2,500  | 1,364 | 2,286  | 2,491 | 2,785  | 1,233   |
| 3,000  | 1,160 | 2,743  | 2,314 | 3,198  | 1,240   |
| 3,500  | 0,930 | 3,186  | 2,225 | 3,494  | 1,331   |
| 4,000  | 0,656 | 3,605  | 2,187 | 3,745  | 1,537   |
| 4,500  | 0,360 | 4,007  | 2,173 | 4,002  | 1,813   |
| 5,000  | 0,227 | 4,489  | 2,177 | 4,421  | 1,951   |
| 5,500  | 0,319 | 4,960  | 2,207 | 4,909  | 1,888   |
| 6,000  | 0,424 | 5,448  | 2,236 | 5,393  | 1,812   |
| 6,500  | 0,488 | 5,944  | 2,260 | 5,887  | 1,773   |
| 7,000  | 0,460 | 6,442  | 2,281 | 6,381  | 1,822   |
| 8,000  | 0,398 | 7,433  | 2,322 | 7,359  | 1,936   |
| 8,500  | 0,338 | 7,930  | 2,343 | 7,850  | 2,006   |
| 9,000  | 0,272 | 8,414  | 2,363 | 8,314  | 2,153   |
| 9,500  | 0,039 | 8,882  | 2,387 | 8,753  | 2,352   |
| 10,000 | 0,057 | 9,369  | 2,414 | 9,234  | 2,361   |
| 10,500 | 0,288 | 9,812  | 2,443 | 9,670  | 2,160   |
| 11,000 | 0,490 | 10,269 | 2,476 | 10,121 | 1,992   |
| 11,500 | 0,818 | 10,646 | 2,511 | 10,434 | 1,706   |
| 12,000 | 1,133 | 11,034 | 2,576 | 10,739 | 1,473   |
| 12,500 | 1,411 | 11,449 | 2,675 | 11,072 | 1,318   |
| 13,000 | 1,647 | 11,890 | 2,811 | 11,446 | 1,246   |
| 13,500 | 1,847 | 12,348 | 2,986 | 11,874 | 1,233   |
| 14,000 | 2,040 | 12,809 | 3,178 | 12,334 | 1,233   |
| 14,500 | 2,232 | 13,271 | 3,370 | 12,796 | 1,233   |
| 14,871 | 2,375 | 13,613 | 3,513 | 13,139 | 1,233   |

DADOS DO PAINEL

- QUANTIDADE  
1 (códigos: S5)
- ÁREA DE FORMA FINAL  
22,33 m2
- COMPRIMENTO L / R  
14,87 / 13,08 m
- CAIXA (LARG. X ALT.)  
3,51 x 13,61 m
- MATERIAL  
PVDF tipo II 1050 g/m2, creme Zion; faixas soldadas em fábrica (HF 40 mm) numa peça única de = 105 m2 (fardo = 120 kg).
- BORDAS E RECORTES**
- SOLDA HF · emenda de fábrica, sobreposição 40 mm
  - BOLSA DE CABO · cabo inox Ø12 com esticador, chapa de canto
  - RECORTE com anel de reforço soldado (150 mm) e clamp / requadro

NOTAS

- Padrão = geometria de forma final da superfície entre as costuras; o confeccionista aplica a compensação do tecido (ensaio biaxial típico 0,5 a 1,5 % no urdume e 2 a 4 % na trama) e as sobras de bolsa/veder.
- Origem (O: 0) no canto inferior esquerdo da caixa; eixo x horizontal, y vertical; L0 → L1 é a borda esquerda (costura de referência), R0 → R1 a direita; estações medidas ao longo de L.
- Marcar em cada painel: código, modelo, orientação (L/R, base), linhas de presilha e centros dos recortes; etiqueta de tecido cosida no verso.
- Form-finding obrigatório: a superfície de dois cumes é anticlástica entre os cumes; os padrões aqui são geométricos (forma-alvo) e devem ser ajustados pelo confeccionista com compensação biaxial.

|                                                |                                                                |                                |
|------------------------------------------------|----------------------------------------------------------------|--------------------------------|
| <div>ZIONHOTEL GROUPINTERNATIONAL</div>        | <b>PADRÃO DE CORTE S5</b><br>Lona Externa                      |                                |
| <b>ZION SAFARI</b><br>ZION GLAMPING COLLECTION | ESCALA ver malha (m)<br>PROJETO CONCEITUAL · ESTUDO PRELIMINAR | <b>FOLHA LN-15</b><br>SET 2026 |

ZION SAFARI · PADRÃO DE CORTE S6

Faixa S6 · y 2,47 a 3,70 · de x -2,40 (frente) a x 10,50 (fundos) · LONA EXTERNA · geometria de forma final (sem compensação) · metros

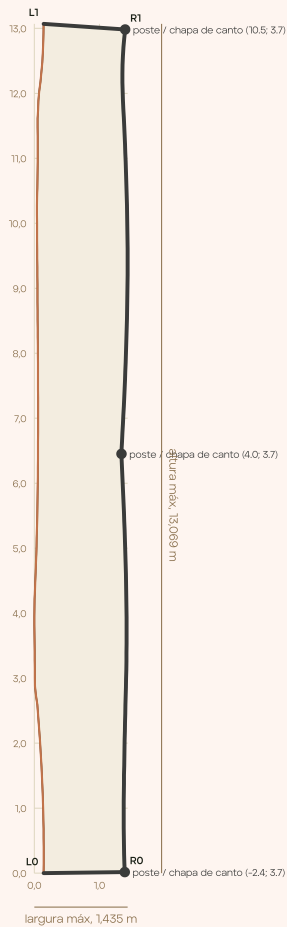


TABELA DE ESTAÇÕES (ao longo da borda L, a cada 0,50 m)

| s (m)  | xL    | yL     | xR    | yR     | largura |
|--------|-------|--------|-------|--------|---------|
| 0,000  | 0,142 | 0,000  | 1,390 | 0,017  | 1,249   |
| 0,500  | 0,143 | 0,500  | 1,377 | 0,517  | 1,234   |
| 1,000  | 0,134 | 1,000  | 1,375 | 1,015  | 1,240   |
| 1,500  | 0,116 | 1,500  | 1,380 | 1,510  | 1,264   |
| 2,000  | 0,089 | 1,999  | 1,389 | 2,003  | 1,300   |
| 2,500  | 0,053 | 2,497  | 1,399 | 2,494  | 1,347   |
| 3,000  | 0,008 | 2,995  | 1,411 | 2,976  | 1,403   |
| 3,500  | 0,004 | 3,495  | 1,418 | 3,475  | 1,414   |
| 4,000  | 0,000 | 3,995  | 1,418 | 3,975  | 1,418   |
| 4,500  | 0,014 | 4,494  | 1,411 | 4,475  | 1,397   |
| 5,000  | 0,032 | 4,994  | 1,398 | 4,977  | 1,366   |
| 5,500  | 0,044 | 5,494  | 1,381 | 5,479  | 1,337   |
| 6,000  | 0,052 | 5,994  | 1,360 | 5,984  | 1,308   |
| 6,500  | 0,056 | 6,494  | 1,341 | 6,489  | 1,285   |
| 7,000  | 0,057 | 6,994  | 1,367 | 6,996  | 1,309   |
| 7,500  | 0,057 | 7,494  | 1,390 | 7,500  | 1,334   |
| 8,000  | 0,054 | 7,994  | 1,410 | 8,003  | 1,356   |
| 8,500  | 0,051 | 8,494  | 1,424 | 8,504  | 1,375   |
| 9,000  | 0,047 | 8,994  | 1,432 | 9,005  | 1,385   |
| 9,500  | 0,044 | 9,494  | 1,434 | 9,505  | 1,390   |
| 10,000 | 0,041 | 9,994  | 1,430 | 10,005 | 1,389   |
| 10,500 | 0,045 | 10,494 | 1,419 | 10,504 | 1,374   |
| 11,000 | 0,052 | 10,994 | 1,403 | 11,004 | 1,351   |
| 11,500 | 0,050 | 11,494 | 1,382 | 11,506 | 1,331   |
| 12,000 | 0,070 | 11,993 | 1,359 | 12,001 | 1,289   |
| 12,500 | 0,122 | 12,490 | 1,358 | 12,451 | 1,236   |
| 13,000 | 0,141 | 12,990 | 1,389 | 12,909 | 1,251   |
| 13,079 | 0,142 | 13,069 | 1,397 | 12,982 | 1,258   |

DADOS DO PAINEL

- QUANTIDADE  
1 (códigos: S6)
- ÁREA DE FORMA FINAL  
17,36 m2
- COMPRIMENTO L / R  
13,08 / 12,97 m
- CAIXA (LARG. X ALT.)  
1,43 x 13,07 m
- MATERIAL  
PVDF tipo II 1050 g/m2, creme Zion; faixas soldadas em fábrica (HF 40 mm) numa peça única de = 105 m2 (fardo = 120 kg).
- BORDAS E RECORTES
- SOLDA HF · emenda de fábrica, sobreposição 40 mm
  - BOLSA DE CABO · cabo inox Ø12 com esticador, chapa de canto

- NOTAS
- Padrão = geometria de forma final da superfície entre as costuras; o confeccionista aplica a compensação do tecido (ensaio biaxial típico 0,5 a 1,5 % no urdume e 2 a 4 % na trama) e as sobras de bolsa/veder.
  - Origem (O: 0) no canto inferior esquerdo da caixa; eixo x horizontal, y vertical; L0 → L1 é a borda esquerda (costura de referência), R0 → R1 a direita; estações medidas ao longo de L.
  - Marcar em cada painel: código, modelo, orientação (L/R, base), linhas de presilha e centros dos recortes; etiqueta de tecido cosida no verso.
  - Form-finding obrigatório: a superfície de dois cumes é anticiclástica entre os cumes; os padrões aqui são geométricos (forma-alvo) e devem ser ajustados pelo confeccionista com compensação biaxial.

|                                                            |   |
|------------------------------------------------------------|---|
| <div>ZION</div> <div>HOTEL GROUP<br/>INTERNATIONAL</div>   | <div>PADRÃO DE CORTE S6</div> <div>Lona Externa</div>                                                                        |
| <div>ZION SAFARI</div> <div>ZION GLAMPING COLLECTION</div> | <div>ESCALA ver malha (m)</div> <div>PROJETO CONCEITUAL · ESTUDO PRELIMINAR</div> <div>FOLHA LN-16</div> <div>SET 2026</div> |

ZION SAFARI · PADRÃO DE CORTE F1

Forro F1 · y -2.70 a -1.35 · sobre o corpo (x 0 a 9.5), 0,30 m sob a membrana · FORRO / REVESTIMENTO INTERNO · geometria de forma final (sem compensação) · metros

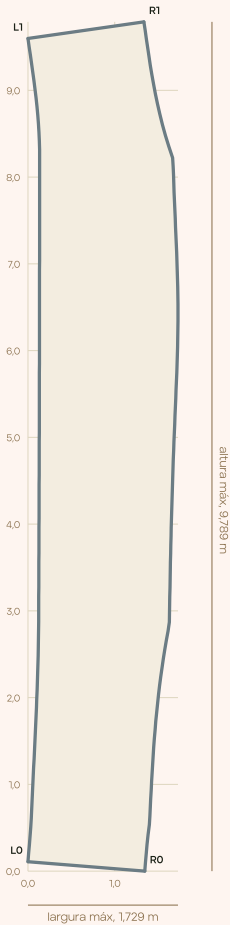


TABELA DE ESTAÇÕES (ao longo da borda L, a cada 0,50 m)

| s (m) | xL    | yL    | xR    | yR    | largura |
|-------|-------|-------|-------|-------|---------|
| 0,000 | 0,000 | 0,108 | 1,346 | 0,000 | 1,350   |
| 0,500 | 0,037 | 0,607 | 1,399 | 0,542 | 1,363   |
| 1,000 | 0,061 | 1,106 | 1,425 | 1,041 | 1,366   |
| 1,500 | 0,085 | 1,606 | 1,458 | 1,543 | 1,375   |
| 2,000 | 0,106 | 2,105 | 1,507 | 2,056 | 1,403   |
| 2,500 | 0,120 | 2,605 | 1,582 | 2,583 | 1,462   |
| 3,000 | 0,124 | 3,105 | 1,633 | 3,099 | 1,510   |
| 3,500 | 0,126 | 3,605 | 1,643 | 3,600 | 1,517   |
| 4,000 | 0,127 | 4,105 | 1,655 | 4,100 | 1,528   |
| 4,500 | 0,129 | 4,605 | 1,670 | 4,601 | 1,541   |
| 5,000 | 0,130 | 5,105 | 1,689 | 5,102 | 1,558   |
| 5,500 | 0,131 | 5,605 | 1,709 | 5,603 | 1,578   |
| 6,000 | 0,132 | 6,105 | 1,725 | 6,103 | 1,593   |
| 6,500 | 0,133 | 6,605 | 1,727 | 6,603 | 1,595   |
| 7,000 | 0,133 | 7,105 | 1,715 | 7,104 | 1,581   |
| 7,500 | 0,134 | 7,605 | 1,693 | 7,605 | 1,560   |
| 8,000 | 0,133 | 8,105 | 1,674 | 8,106 | 1,541   |
| 8,500 | 0,121 | 8,605 | 1,522 | 8,715 | 1,405   |
| 9,000 | 0,069 | 9,102 | 1,411 | 9,282 | 1,354   |
| 9,500 | 0,000 | 9,597 | 1,336 | 9,789 | 1,350   |

DADOS DO PAINEL

QUANTIDADE  
1 (códigos: F1)  
ÁREA DE FORMA FINAL  
14,31 m2  
COMPRIMENTO L / R  
9,50 / 9,85 m  
CAIXA (LARG. X ALT.)  
1,73 x 9,79 m  
MATERIAL  
Trevira CS 210 g/m2 tensionado, creme; harpão nos trilhos suspensos por cabos Ø4

BORDAS E RECORTES

HARPÃO · perfil de alumínio 40 x 20 nos arcos / terças / cabos

- NOTAS**
- Padrão = geometria de forma final da superfície entre as costuras; o confeccionista aplica a compensação do tecido (ensaio biaxial típico 0,5 a 1,5 % no urdume e 2 a 4 % na trama) e as sobras de bolsa/veder.
  - Origem (O: 0) no canto inferior esquerdo da caixa; eixo x horizontal, y vertical; L0 → L1 é a borda esquerda (costura de referência), R0 → R1 a direita; estações medidas ao longo de L.
  - Marcar em cada painel: código, modelo, orientação (L/R, base), linhas de presilha e centros dos recortes; etiqueta de tecido cosida no verso.

|                                                |                                                                |                                |
|------------------------------------------------|----------------------------------------------------------------|--------------------------------|
| <div>ZIONHOTEL GROUP INTERNATIONAL</div>       | <b>PADRÃO DE CORTE F1</b><br>Forro / Revestimento Interno      |                                |
| <b>ZION SAFARI</b><br>ZION GLAMPING COLLECTION | ESCALA ver malha (m)<br>PROJETO CONCEITUAL · ESTUDO PRELIMINAR | <b>FOLHA LN-17</b><br>SET 2026 |

ZION SAFARI · PADRÃO DE CORTE F2

Forro F2 · y -1.35 a 0.00 · sobre o corpo (x 0 a 9.5), 0,30 m sob a membrana · FORRO / REVESTIMENTO INTERNO · geometria de forma final (sem compensação) · metros

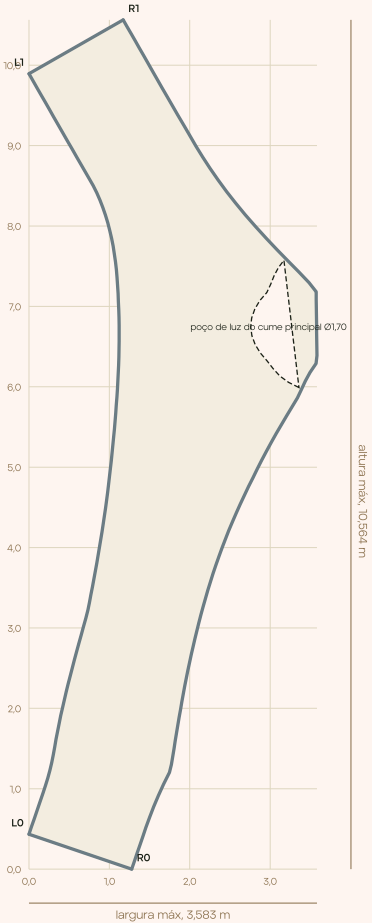


TABELA DE ESTAÇÕES (ao longo da borda L, a cada 0,50 m)

| s (m) | xL    | yL    | xR    | yR     | largura |
|-------|-------|-------|-------|--------|---------|
| 0,000 | 0,000 | 0,434 | 1,278 | 0,000  | 1,350   |
| 0,500 | 0,161 | 0,907 | 1,442 | 0,481  | 1,350   |
| 1,000 | 0,296 | 1,388 | 1,723 | 1,152  | 1,446   |
| 1,500 | 0,389 | 1,879 | 1,831 | 1,662  | 1,458   |
| 2,000 | 0,504 | 2,366 | 1,913 | 2,142  | 1,426   |
| 2,500 | 0,632 | 2,849 | 2,005 | 2,608  | 1,394   |
| 3,000 | 0,755 | 3,334 | 2,117 | 3,081  | 1,385   |
| 3,500 | 0,846 | 3,825 | 2,264 | 3,596  | 1,436   |
| 4,000 | 0,927 | 4,319 | 2,454 | 4,131  | 1,538   |
| 4,500 | 0,994 | 4,814 | 2,693 | 4,680  | 1,705   |
| 5,000 | 1,047 | 5,311 | 2,973 | 5,234  | 1,928   |
| 5,500 | 1,089 | 5,810 | 3,296 | 5,791  | 2,207   |
| 6,000 | 1,116 | 6,309 | 3,576 | 6,331  | 2,460   |
| 6,500 | 1,120 | 6,809 | 3,576 | 6,831  | 2,456   |
| 7,000 | 1,099 | 7,308 | 3,420 | 7,362  | 2,321   |
| 7,500 | 1,036 | 7,804 | 2,750 | 8,072  | 1,735   |
| 8,000 | 0,898 | 8,284 | 2,200 | 8,797  | 1,400   |
| 8,500 | 0,669 | 8,727 | 1,858 | 9,369  | 1,351   |
| 9,000 | 0,420 | 9,161 | 1,596 | 9,823  | 1,350   |
| 9,500 | 0,171 | 9,595 | 1,344 | 10,263 | 1,350   |
| 9,846 | 0,000 | 9,895 | 1,172 | 10,564 | 1,350   |

DADOS DO PAINEL

QUANTIDADE  
1 (códigos: F2)  
ÁREA DE FORMA FINAL  
17,41m2  
COMPRIMENTO L / R  
9,85 / 11,81m  
CAIXA (LARG. X ALT.)  
3,58 x 10,56 m  
MATERIAL  
Trevira CS 210 g/m2 tensionado, creme; harpão nos trilhos suspensos por cabos Ø4

BORDAS E RECORTES

HARPÃO - perfil de alumínio 40 x 20 nos arcos / terças / cabos  
RECORTE com anel de reforço soldado (150 mm) e clamp / requadro

|                                                |                                                                |                                |
|------------------------------------------------|----------------------------------------------------------------|--------------------------------|
| <div>ZIONHOTEL GROUP INTERNATIONAL</div>       | <b>PADRÃO DE CORTE F2</b><br>Forro / Revestimento Interno      |                                |
| <b>ZION SAFARI</b><br>ZION GLAMPING COLLECTION | ESCALA ver malha (m)<br>PROJETO CONCEITUAL · ESTUDO PRELIMINAR | <b>FOLHA LN-18</b><br>SET 2026 |

ZION SAFARI · PADRÃO DE CORTE F3

Forro F3 · y 0.00 a 1.35 · sobre o corpo (x 0 a 9.5), 0,30 m sob a membrana · FORRO / REVESTIMENTO INTERNO · geometria de forma final (sem compensação) · metros

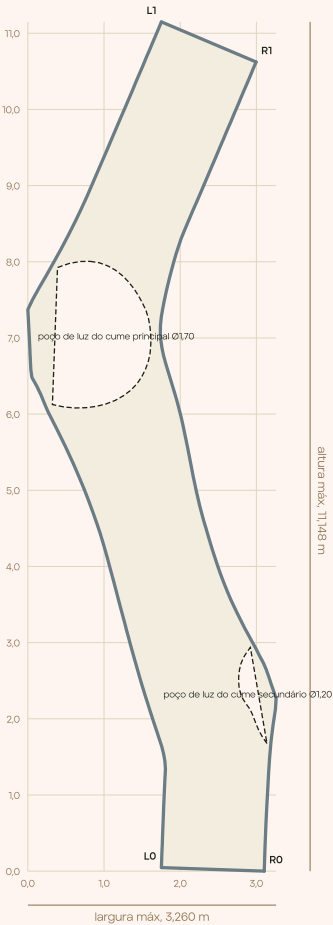


TABELA DE ESTAÇÕES (ao longo da borda L, a cada 0,50 m)

| s (m)  | xL    | yL     | xR    | yR     | largura |
|--------|-------|--------|-------|--------|---------|
| 0,000  | 1,754 | 0,047  | 3,103 | 0,000  | 1,350   |
| 0,500  | 1,772 | 0,547  | 3,122 | 0,521  | 1,351   |
| 1,000  | 1,793 | 1,046  | 3,151 | 1,111  | 1,360   |
| 1,500  | 1,781 | 1,544  | 3,222 | 1,936  | 1,493   |
| 2,000  | 1,632 | 2,021  | 3,159 | 2,560  | 1,620   |
| 2,500  | 1,482 | 2,498  | 2,939 | 3,023  | 1,548   |
| 3,000  | 1,346 | 2,979  | 2,704 | 3,481  | 1,448   |
| 3,500  | 1,217 | 3,462  | 2,520 | 3,926  | 1,384   |
| 4,000  | 1,088 | 3,946  | 2,380 | 4,361  | 1,357   |
| 4,500  | 0,952 | 4,426  | 2,262 | 4,778  | 1,356   |
| 5,000  | 0,785 | 4,898  | 2,172 | 5,179  | 1,415   |
| 5,500  | 0,592 | 5,359  | 2,095 | 5,575  | 1,518   |
| 6,000  | 0,377 | 5,810  | 2,011 | 5,962  | 1,641   |
| 6,500  | 0,167 | 6,264  | 1,899 | 6,373  | 1,736   |
| 7,000  | 0,033 | 6,735  | 1,770 | 6,826  | 1,740   |
| 7,500  | 0,007 | 7,234  | 1,762 | 7,332  | 1,757   |
| 8,000  | 0,169 | 7,692  | 1,842 | 7,770  | 1,673   |
| 8,500  | 0,414 | 8,128  | 1,910 | 7,975  | 1,503   |
| 9,000  | 0,644 | 8,572  | 1,989 | 8,232  | 1,387   |
| 9,500  | 0,850 | 9,027  | 2,116 | 8,551  | 1,352   |
| 10,000 | 1,048 | 9,486  | 2,301 | 8,984  | 1,351   |
| 10,500 | 1,244 | 9,946  | 2,491 | 9,429  | 1,350   |
| 11,000 | 1,439 | 10,406 | 2,684 | 9,882  | 1,350   |
| 11,500 | 1,635 | 10,867 | 2,878 | 10,340 | 1,350   |
| 11,806 | 1,754 | 11,148 | 2,997 | 10,622 | 1,350   |

DADOS DO PAINEL

QUANTIDADE  
1 (códigos: F3)  
ÁREA DE FORMA FINAL  
16,64 m2  
COMPRIMENTO L / R  
11,81 / 11,12 m  
CAIXA (LARG. X ALT.)  
3,26 x 11,16 m  
MATERIAL  
Trevira CS 210 g/m2 tensionado, creme; harpão nos trilhos suspensos por cabos Ø4

BORDAS E RECORTES

HARPÃO - perfil de alumínio 40 x 20 nos arcos / terças / cabos  
RECORTE com anel de reforço soldado (150 mm) e clamp / requadro

- NOTAS
- Padrão = geometria de forma final da superfície entre as costuras; o confeccionista aplica a compensação do tecido (ensaio biaxial típico 0,5 a 1,5 % no urdume e 2 a 4 % na trama) e as sobras de bolsa/veder.
  - Origem (0, 0) no canto inferior esquerdo da caixa; eixo x horizontal, y vertical; L0 → L1 é a borda esquerda (costura de referência), R0 → R1 a direita; estações medidas ao longo de L.
  - Marcar em cada painel: código, modelo, orientação (L/R, base), linhas de presilha e centros dos recortes; etiqueta de tecido cosida no verso.

|                                                          |                                                                |                                |
|----------------------------------------------------------|----------------------------------------------------------------|--------------------------------|
| <div>ZION</div> <div>HOTEL GROUP<br/>INTERNATIONAL</div> | <b>PADRÃO DE CORTE F3</b><br>Forro / Revestimento Interno      |                                |
| <b>ZION SAFARI</b><br>ZION GLAMPING COLLECTION           | ESCALA ver malha (m)<br>PROJETO CONCEITUAL · ESTUDO PRELIMINAR | <b>FOLHA LN-19</b><br>SET 2026 |

ZION SAFARI · PADRÃO DE CORTE F4

Forro F4 · y 1.35 a 2.70 · sobre o corpo (x 0 a 9.5), 0,30 m sob a membrana · FORRO / REVESTIMENTO INTERNO · geometria de forma final (sem compensação) · metros

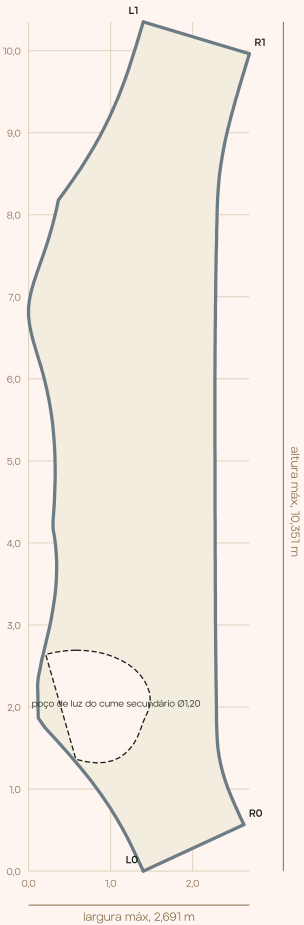


TABELA DE ESTAÇÕES (ao longo da borda L, a cada 0,50 m)

| s (m)  | xL    | yL     | xR    | yR    | largura |
|--------|-------|--------|-------|-------|---------|
| 0,000  | 1,398 | 0,000  | 2,623 | 0,567 | 1,350   |
| 0,500  | 1,181 | 0,450  | 2,446 | 0,969 | 1,367   |
| 1,000  | 0,922 | 0,878  | 2,350 | 1,264 | 1,479   |
| 1,500  | 0,621 | 1,276  | 2,307 | 1,506 | 1,702   |
| 2,000  | 0,289 | 1,651  | 2,293 | 1,731 | 2,005   |
| 2,500  | 0,114 | 2,090  | 2,287 | 2,118 | 2,174   |
| 3,000  | 0,163 | 2,586  | 2,281 | 2,609 | 2,119   |
| 3,500  | 0,275 | 3,073  | 2,278 | 3,085 | 2,003   |
| 4,000  | 0,340 | 3,568  | 2,275 | 3,576 | 1,936   |
| 4,500  | 0,316 | 4,067  | 2,274 | 4,073 | 1,958   |
| 5,000  | 0,317 | 4,565  | 2,272 | 4,569 | 1,956   |
| 5,500  | 0,321 | 5,064  | 2,271 | 5,069 | 1,951   |
| 6,000  | 0,279 | 5,562  | 2,271 | 5,565 | 1,992   |
| 6,500  | 0,178 | 6,052  | 2,271 | 6,046 | 2,093   |
| 7,000  | 0,039 | 6,532  | 2,274 | 6,512 | 2,235   |
| 7,500  | 0,024 | 7,027  | 2,279 | 7,003 | 2,255   |
| 8,000  | 0,176 | 7,503  | 2,286 | 7,466 | 2,110   |
| 8,500  | 0,319 | 7,962  | 2,296 | 7,934 | 1,978   |
| 9,000  | 0,537 | 8,420  | 2,311 | 8,310 | 1,777   |
| 9,500  | 0,805 | 8,842  | 2,346 | 8,630 | 1,556   |
| 10,000 | 1,031 | 9,288  | 2,414 | 8,984 | 1,416   |
| 10,500 | 1,212 | 9,754  | 2,519 | 9,386 | 1,358   |
| 11,000 | 1,362 | 10,231 | 2,655 | 9,842 | 1,350   |
| 11,125 | 1,398 | 10,351 | 2,691 | 9,961 | 1,350   |

DADOS DO PAINEL

QUANTIDADE  
1 (códigos: F4)  
ÁREA DE FORMA FINAL  
18,76 m2  
COMPRIMENTO L / R  
11,12 / 9,50 m  
CAIXA (LARG. X ALT.)  
2,69 x 10,35 m  
MATERIAL  
Trevira CS 210 g/m2 tensionado, creme; harpão nos trilhos suspensos por cabos  
04

BORDAS E RECORTES


HARPÃO - perfil de alumínio 40 x 20 nos arcos / terças / cabos  
RECORTE com anel de reforço soldado (150 mm) e clamp / requadro

|                                                |                                                                |                                |
|------------------------------------------------|----------------------------------------------------------------|--------------------------------|
| <div>ZIONHOTEL GROUPINTERNATIONAL</div>        | <b>PADRÃO DE CORTE F4</b><br>Forro / Revestimento Interno      |                                |
| <b>ZION SAFARI</b><br>ZION GLAMPING COLLECTION | ESCALA ver malha (m)<br>PROJETO CONCEITUAL · ESTUDO PRELIMINAR | <b>FOLHA LN-20</b><br>SET 2026 |


ZION SAFARI · FIXAÇÃO DA LONA NOS FERROS

Detalhes esquemáticos 1:5 · keder, bolsa de base, bolsa de tubo, clamp de anel, harpão do forro, bolsa de cabo · sequência de tensionamento


1 · KEDER DUPLO NO ARCO / CAIBRO

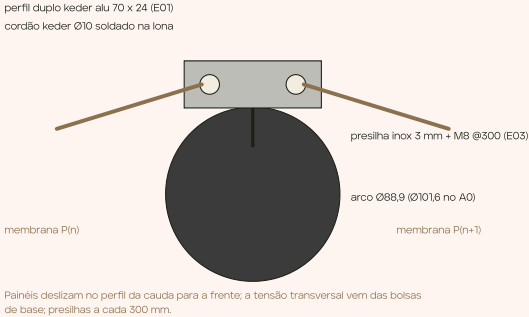


2 · BOLSA DE BASE NO TRILHO

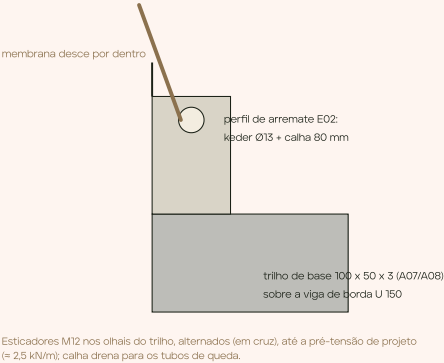


3 · BOLSA DE TUBO (BICO E CAUDA)

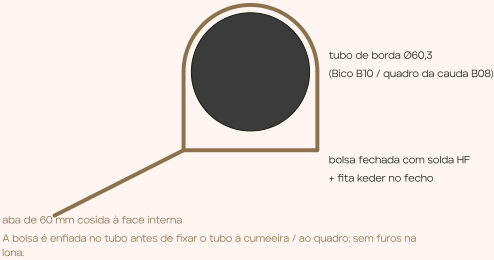

4 · CLAMP DE ANEL (CUME, LANTERNA, OLHOS, ESPINHA)

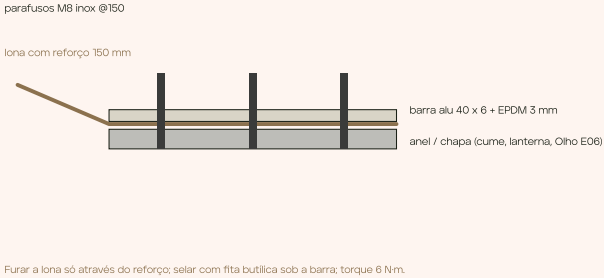

5 · HARPÃO DO FORRO INTERNO

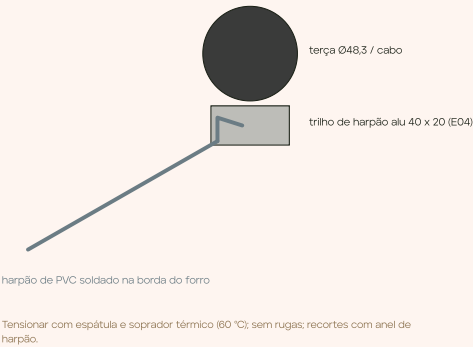

6 · BOLSA DE CABO DE BORDA



Safari: peça única içada pelos anéis dos cumes e presa nos clamps (4); perímetro em bolsa de cabo Ø12 (6) com chapas de canto nos 7 postes; forro F1 a F4 em harpão (5) nos trilhos suspensos.

SEQUÊNCIA: 1 conferir geometria da estrutura (topo dos arcos ± 15 mm) · 2 desenrolar e posicionar sem arrastar (proteger arestas) · 3 enfiar keder / cabos / bolsas sem tensão · 4 fechar clamps e anéis · 5 tensionar em cruz, em 3 passes (30 %, 70 %, 100 %) · 6 medir pré-tensão e flechas, registrar · 7 teste de água · vento > 30 km/h suspende.

|                                                            |   |
|------------------------------------------------------------|---|
| <div>ZION</div> <div>HOTEL GROUP<br/>INTERNATIONAL</div>   | <div>FIXAÇÃO DA LONA NOS FERROS</div> <div>Keder · bolsas · clamps · harpão · cabos</div>                                        |
| <div>ZION SAFARI</div> <div>ZION GLAMPING COLLECTION</div> | <div>ESCALA 1:5 (esquemático)</div> <div>PROJETO CONCEITUAL · ESTUDO PRELIMINAR</div> <div>FOLHA LN-90</div> <div>SET 2026</div> |




COBERTURA SAFARI: CUME E BEIRAL

Seção vertical pelo mastro principal M1 e anel do Zênite; seção pelo anel de beiral sobre pilar.

ZION GLAMPING COLLECTION  
ZION SAFARI | DET-02

SEÇÃO A - ANEL DO ZÊNITE Ø1200 COM ÓCULO DE VIDRO

escala 1:10 (1 mm = 0,34 px)

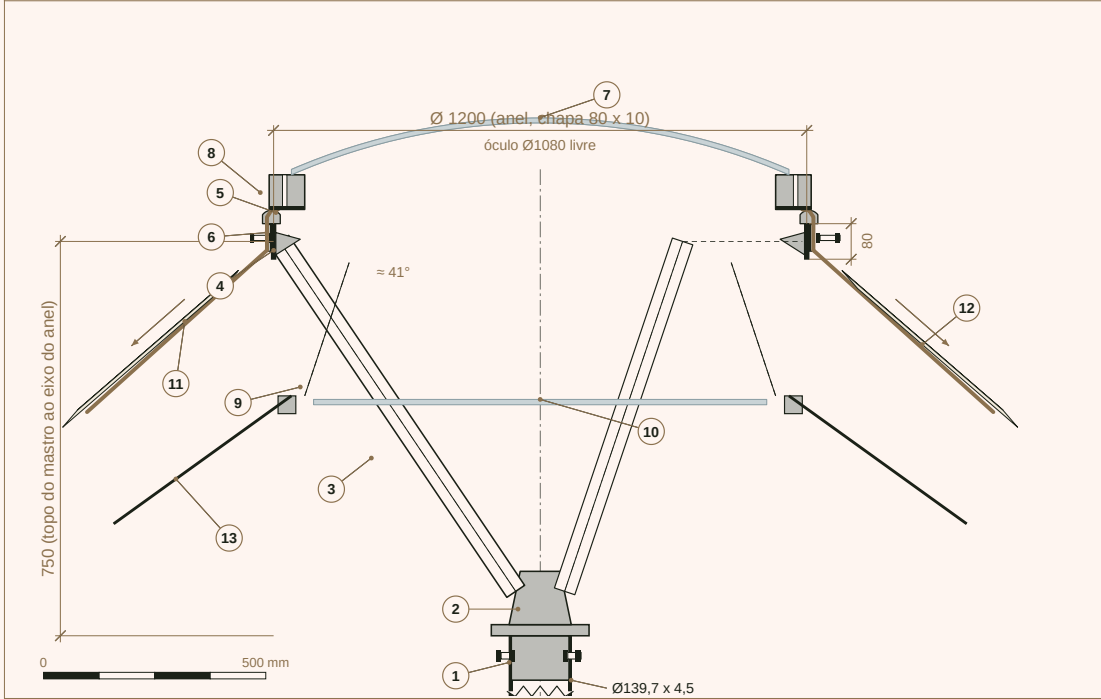

LEGENDA

- 1

Mastro M1 Ø139,7 x 4,5 mm, 5,05 m (topo em z = 5,05)
- 2

Capitel usinado: bujão Ø130 x 100 + flange Ø220 x 25, 2 x M12 radiais
- 3

Braço da coroa Ø48,3 x 3,0 mm, L = 0,95 m (3 a 120°)
- 4

Anel do cume: chapa curvada 80 x 10 mm, Ø1200, gusset ao braço
- 5

Perfil arredondado de alumínio no topo do anel (R 25)
- 6

Chapa-anel de alumínio 60 x 8, M8 @ 150 + gaxeta EPDM
- 7

Cúpula de vidro laminado 6+6 mm curvo (R 1400), low-e
- 8

Moldura da cúpula: alumínio com ruptura térmica, gaxeta EPDM
- 9

Anel do forro Ø1100 em alumínio 40 x 40, pendurado nos braços
- 10

Segundo vidro plano laminado 6+6 mm (câmara de ar entre vidros)
- 11

Membrana PVDF deixando o anel com ≈ 41°, pré-tensão 2,5 kN/m
- 12

Escoamento da chuva ao beiral e às bordas em catenária
- 13

Isolamento (manta + lâ PET 50 mm) e forro paralelos à membrana
- 14

Anel de beiral: tubo retangular 150 x 100 x 4,0 mm (viga-anel)
- 15

Pilar Ø101,6 x 4,0 mm embutido no painel, chapa de topo 150 x 150 x 8
- 16


Perfil de borda arredondado (alumínio R 40) + fascia 2 mm
- 17

Calha oculta de alumínio 80 x 60 mm, saída Ø50 ao pilar
- 18

Trilho keder da aba em balanço (membrana até os postes externos)

SEÇÃO B - ANEL DE BEIRAL SOBRE PILAR

escala 1:8 (1 mm = 0,5 px)

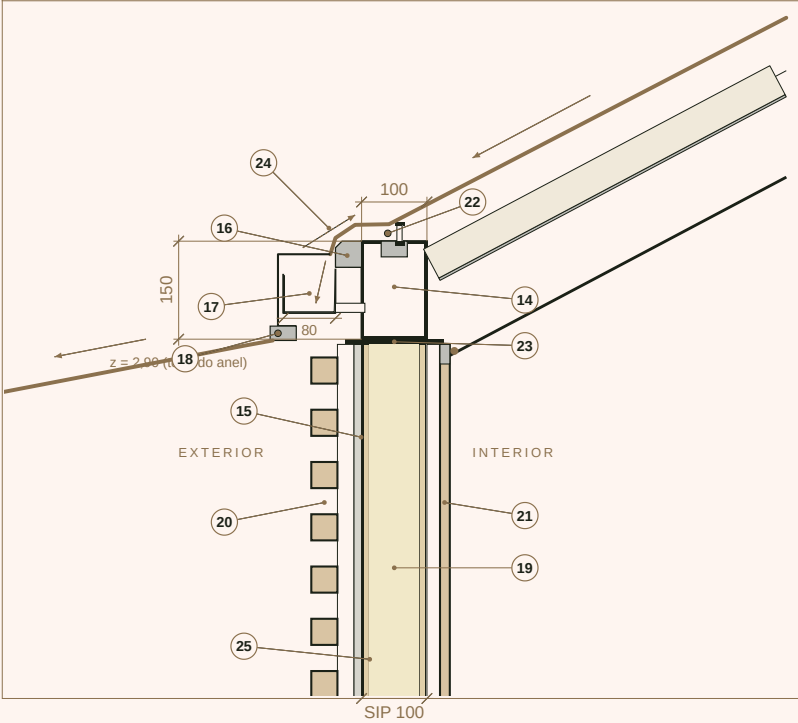

- 19

Painel SIP 100 mm (OSB 12 / PIR 76 / OSB 12)
- 20

Placa cimentícia 12 + câmara 25 + ripado termotratado 40 x 40
- 21

Acabamento interno: painel madeira/tecido 15 mm sobre ripas 20
- 22

Trilho keder da membrana principal sobre o anel (alumínio 40 x 24)
- 23

Chapa de topo do pilar soldada ao anel de beiral
- 24

Entrada de ar da câmara ventilada pela fresta alta (tela anti-inseto)
- 25

Tubo de queda Ø75 mm dentro do pilar (2 pilares)

|   |                                      |          |
|---|--------------------------------------|----------|
|  <div><div>ZION GLAMPING COLLECTION</div><div>COBERTURA SAFARI: CUME E BEIRAL</div><div>ZION SAFARI</div></div> | ESCALA<br>1:10 (cume) / 1:8 (beiral) |          |
|   | FOLHA                                | DATA     |
|   | DET-02                               | SET 2026 |



# ZION SAFARI · CAMADAS CONSTRUTIVAS

Pilha explodida das 13 camadas, da fundacao ao acabamento interno · isometrica · sem escala

CAMADA 13  
**ACABAMENTO INTERNO**  
Mobiliário fixo, divisórias e revestimentos

CAMADA 12  
**INSTALACOES HIDRAULICAS**  
PEX Ø25 agua fria e quente, esgoto Ø100 por gravidade


CAMADA 11  
**INSTALACOES ELETRICAS**  
Quadro no atico, circuitos embutidos e iluminacao indireta

CAMADA 10  
**MEMBRANA INTERNA**  
Forro tensionado acustico define a superficie interna

CAMADA 09  
**BARREIRA DE CONDENSACAO**  
Filme de controle de vapor protege o isolamento da umidade

CAMADA 08  
**ISOLAMENTO TERMICO**  
La PET 50 mm + manta refletiva controlam ganho e perda de calor

CAMADA 07  
**CAMARA DE VENTILACAO**

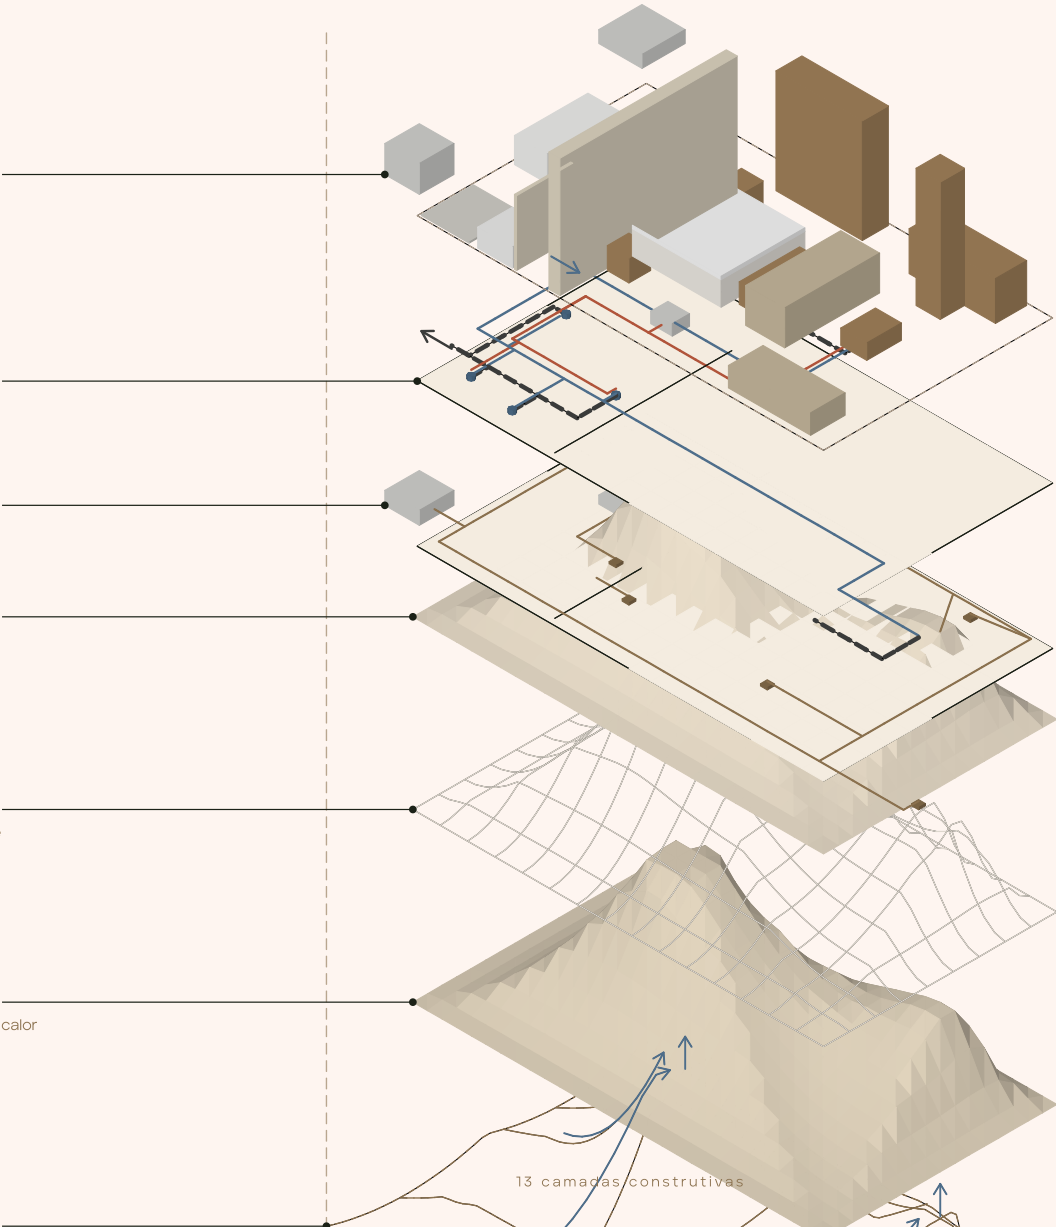


**ESQUADRIAS**

(a) Janela Olho do Casulo; (b) fachada de vidro inclinada 8° do Casulo; (c) fachada frontal do Safari; (d) fresta no painel SIP.

ZION GLAMPING COLLECTION  
COMUM | DET-05


**(A) JANELA OLHO 1600 X 950: SEÇÃO VERTICAL E ELEVÇÃO**

1:10 (1 mm = 0,22 px) / 1:40

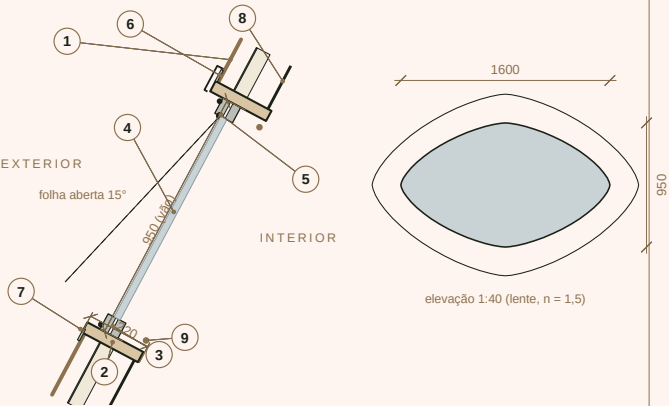


**(B) FACHADA DE VIDRO CASULO INCLINADA 8°: ELEVÇÃO E DETALHES**

1:60 / 1:5

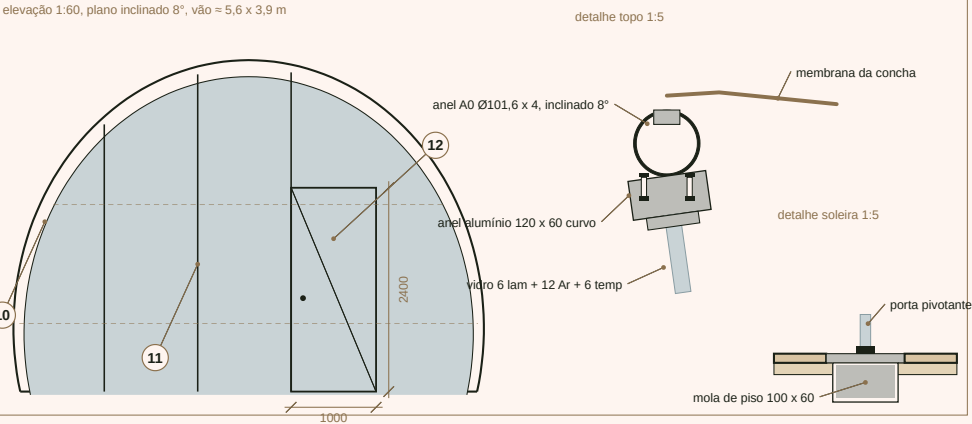

**(C) FACHADA FRONTAL SAFARI 5400 X 2750: 2 FIXAS + 2 DE CORRER**

1:50 / 1:5

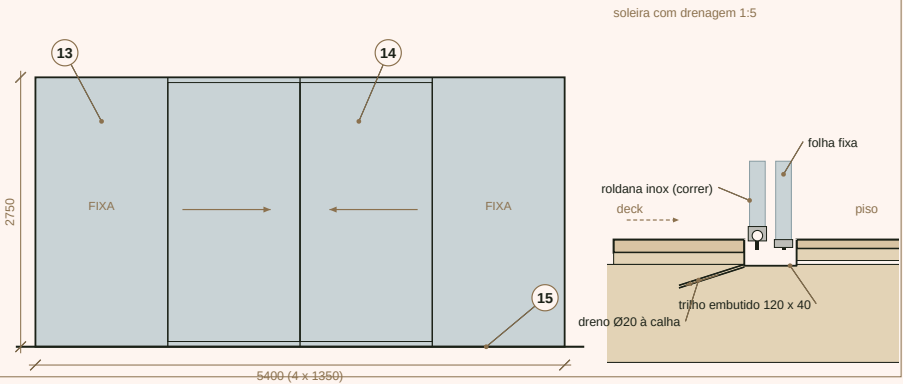


- 1 Envelope: membrana + câmara 60 + manta + lâ PET 50 + forro
- 2 Requadro em madeira laminada 220 x 40 (anel da lente)
- 3 Marco de alumínio com ruptura térmica 60 x 70, bronze
- 4 Vidro duplo 6 lam + 12 Ar + 6 temp, low-e (U 1,6)
- 5 Basculante de projeção: dobradiça superior + braços de fricção
- 6 Grampo de alumínio da membrana + gaxeta EPDM + pingadeira
- 7 Peitoril inclinado 5% com friso pingadeira; canal de condensação

- 8 Forro tensionado fechando no requadro
- 9 Fita LED 2700 K oculta no requadro
- 10 Anel A0 Ø101,6 x 4,0 a 8° com anel de alumínio 120 x 60 curvo
- 11 Montantes de alumínio 60 x 120 RPT; travessas a 0,8 e 2,2 m
- 12 Porta pivotante de vidro 1000 x 2400 com mola de piso
- 13 Folha fixa 1350 x 2750 (vidro duplo)
- 14 Folha de correr 1350 x 2750, roldanas inox, fecho multiponto

- 15 Trilho embutido nivelado com deck e piso; dreno à calha
- 16 Marco de alumínio RPT 60 x 60 fixado ao requadro de madeira
- 17 Vidro duplo 6 + 12 + 6 (fresta fixa, 300 mm de altura)
- 18 Rufo de verga: alumínio 1,5 mm atrás da cimentícia, pingadeira
- 19 Rufo de peitoril inclinado, aba vertical 120 mm
- 20 Câmara ventilada 25 mm com tela anti-inseto
- 21 Requadro de madeira 40 mm selando o núcleo PIR (selante + tarucel)

**(D) FRESTA DE VIDRO NO PAINEL SIP 100 COM RUFOS**

1:5 (1 mm = 0,5 px)

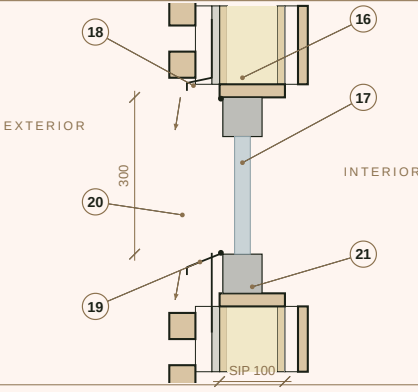

ZION GLAMPING COLLECTION  
**ESQUADRIAS**  
COMUM


ESCALA  
1:10 / 1:5 / 1:60

FOLHA  
**DET-05**

DATA  
SET 2026

 ZION SAFARI · QUADRO DE ESQUADRIAS

Vistas externas em 1:50 · dimensões em metros (largura x altura) · vidro insulado 6 lam + 12 Ar + 6 temp low-e · alumínio bronze com ruptura térmica

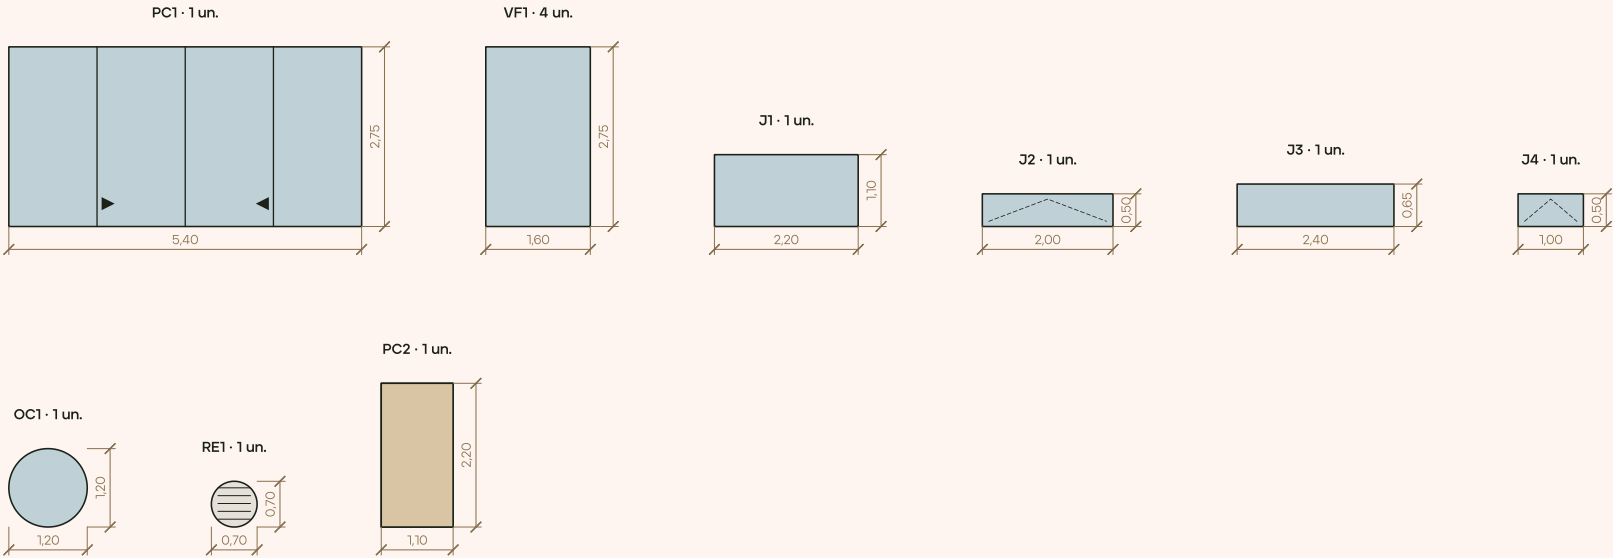


| CÓD. | ESQUADRIA                                 | L X H (M)   | QTD | ESPECIFICAÇÃO                                                                                  | LOCALIZAÇÃO                          |
|------|-------------------------------------------|-------------|-----|------------------------------------------------------------------------------------------------|--------------------------------------|
| PC1  | Fachada de correr (2 fixas + 2 de correr) | 5,40 x 2,75 | 1   | 4 folhas 1,35 x 2,75; vidro insulado low-e; trilho embutido no piso com dreno                  | Fachada frontal, x 0                 |
| VF1  | Vidro lateral fixo                        | 1,60 x 2,75 | 4   | Painéis fixos de vidro insulado; montantes de alumínio RPT bronze                              | Lateral direita, x 0 a 6,40          |
| J1   | Janela do café (fixa)                     | 2,20 x 1,10 | 1   | Vidro insulado; peitoril 1,10                                                                  | Lateral esquerda, x 0,50 a 2,70      |
| J2   | Fresta alta do closet (basculante)        | 2,00 x 0,50 | 1   | Vidro insulado; peitoril 1,90; motorizada                                                      | Lateral esquerda, x 3,90 a 5,90      |
| J3   | Fresta da banheiro (fixa)                 | 2,40 x 0,65 | 1   | Vidro insulado jateado; peitoril 1,50                                                          | Fundos, y -0,80 a +1,60              |
| J4   | Janela alta do chuveiro (basculante)      | 1,00 x 0,50 | 1   | Vidro insulado jateado; peitoril 1,90                                                          | Lateral direita, x 8,30 a 9,30       |
| OC1  | Óculo do Zênite                           | 1,20 x 1,20 | 1   | Cúpula de vidro laminado curvo Ø1,20 sobre anel; vidro interno plano; esquadria RPT calandrada | Cume principal, sobre a cama         |
| RE1  | Chaminé do Respiro                        | 0,70 x 0,70 | 1   | Tubo de alumínio Ø700 com veneziana motorizada e tela                                          | Cume secundário, sobre o café        |
| PC2  | Porta de correr do banho                  | 1,10 x 2,20 | 1   | Folha de madeira laminada, trilho superior                                                     | Parede da cabeceira, y +1,50 a +2,60 |

|   |                                                            |
|---|------------------------------------------------------------|
|  ZION SAFARI<br>HOTEL GROUP INTERNATIONAL | <b>QUADRO DE ESQUADRIAS</b><br>9 tipos · 12 unidades       |
| ZION SAFARI<br>ZION GLAMPING COLLECTION                                                                                        | ESCALA 1:50 (A1)<br>PROJETO CONCEITUAL · ESTUDO PRELIMINAR |
|   | FOLHA PA-09<br>SET 2026                                    |

# ZION SAFARI · PLANTA DE COBERTURA

Membrana PVDF de dois cumes · curvas de nível a cada 0,40 m · bordas em catenária · pingadeiras nos pontos baixos · calha oculta no anel de beiral

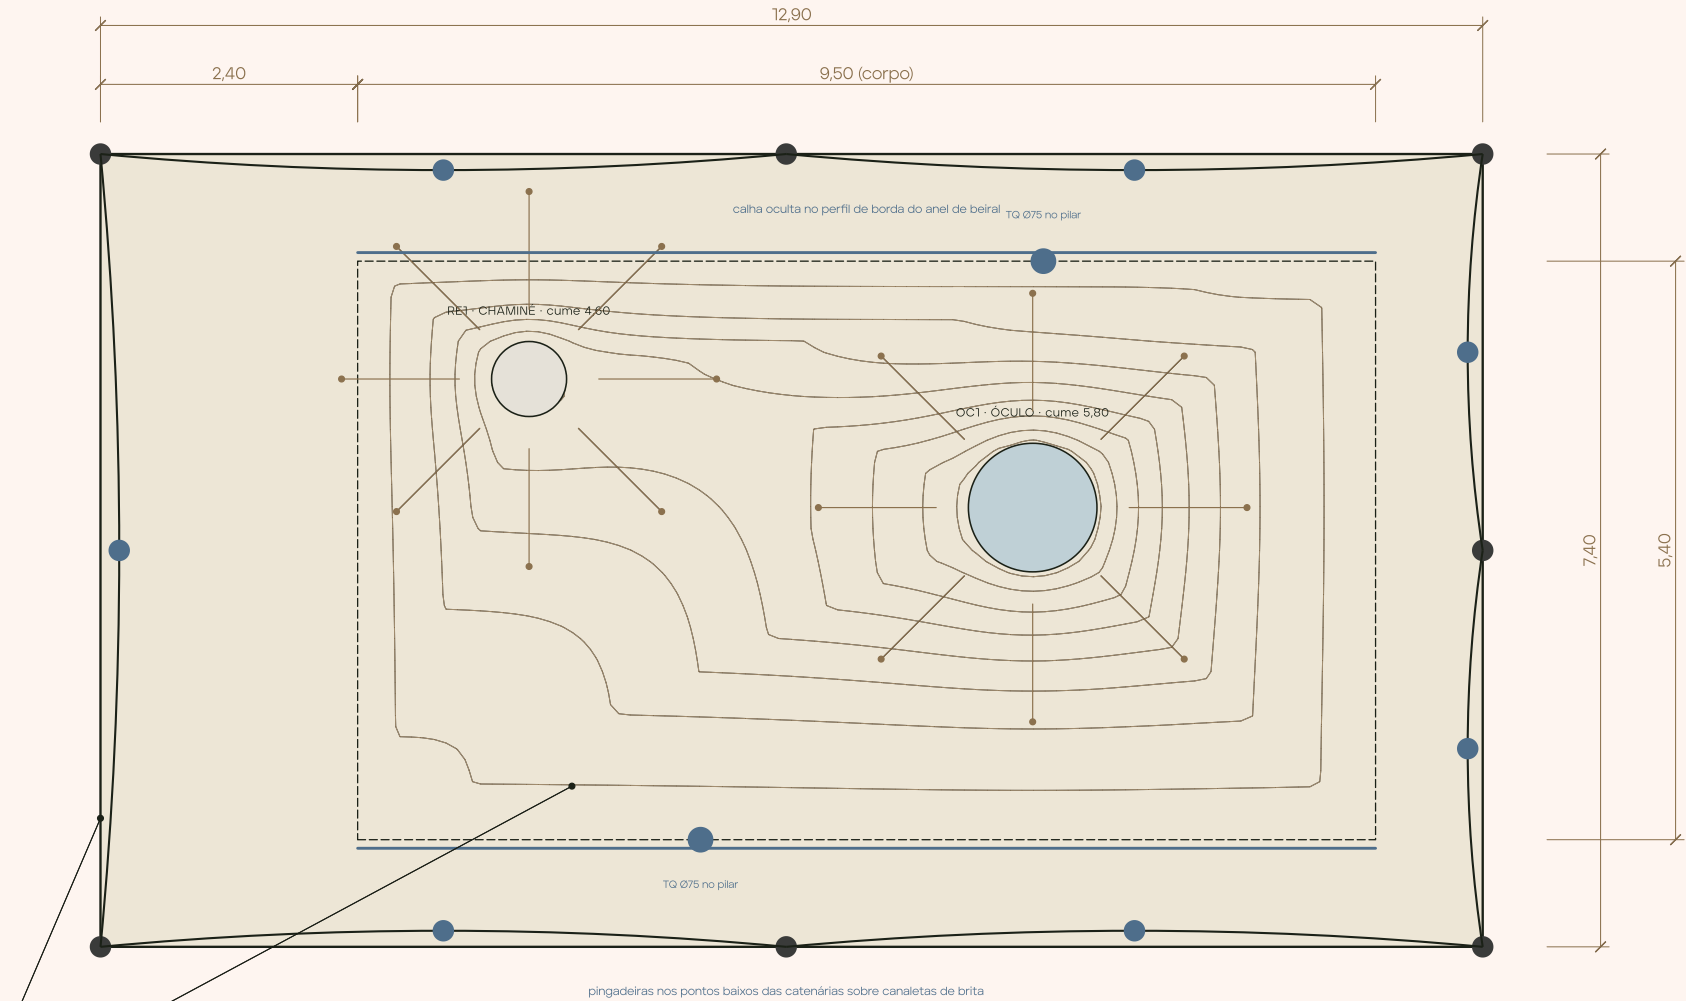

cabo de borda Ø12 inox em bolsa; postes PE inclinados 8°

membrana PVDF 1050 g/m2 em gomos radiais soldados por RF; i mín. 14° no vale



|   |                                                                                                |                         |
|---|------------------------------------------------------------------------------------------------|-------------------------|
|  <b>ZION SAFARI</b><br>ZION GLAMPING COLLECTION | <b>PLANTA DE COBERTURA</b><br>Escoamento, calhas, tubos de queda, claraboia / óculo e respiros |                         |
|   | ESCALA 1:50 (A1)<br>PROJETO CONCEITUAL · ESTUDO PRELIMINAR                                     | FOLHA PA-04<br>SET 2026 |

# VIDROS E ESQUADRIAS · QUADRO

42,3 m2 de vidro · peso estimado 30 kg/m2 (insulado 6 + 12 + 6) a 40 kg/m2 (laminado curvo) · panos ≤ 90 kg para transporte manual em montanha (acima disso, dividir o pano ou usar içador a vácuo)

| CÓD. | ESQUADRIA                                 | LARG. (M) | ALT. (M) | QTD | M2 UN. | KG UN. | ESPECIFICAÇÃO                                                                                  | LOCALIZAÇÃO                          |
|------|-------------------------------------------|-----------|----------|-----|--------|--------|------------------------------------------------------------------------------------------------|--------------------------------------|
| PC1  | Fachada de correr (2 fixas + 2 de correr) | 5,40      | 2,75     | 1   | 14,85  | 446    | 4 folhas 1,35 x 2,75; vidro insulado low-e; trilho embutido no piso com dreno                  | Fachada frontal, x 0                 |
| VF1  | Vidro lateral fixo                        | 1,60      | 2,75     | 4   | 4,4    | 132    | Painéis fixos de vidro insulado; montantes de alumínio RPT bronze                              | Lateral direita, x 0 a 6,40          |
| J1   | Janela do café (fixa)                     | 2,20      | 1,10     | 1   | 2,42   | 73     | Vidro insulado; peitoril 1,10                                                                  | Lateral esquerda, x 0,50 a 2,70      |
| J2   | Fresta alta do closet (basculante)        | 2,00      | 0,50     | 1   | 1      | 30     | Vidro insulado; peitoril 1,90; motorizada                                                      | Lateral esquerda, x 3,90 a 5,90      |
| J3   | Fresta da banheira (fixa)                 | 2,40      | 0,65     | 1   | 1,56   | 47     | Vidro insulado jateado; peitoril 1,50                                                          | Fundos, y -0,80 a +1,60              |
| J4   | Janela alta do chuveiro (basculante)      | 1,00      | 0,50     | 1   | 0,5    | 15     | Vidro insulado jateado; peitoril 1,90                                                          | Lateral direita, x 8,30 a 9,30       |
| OC1  | Óculo do Zênite                           | 1,20      | 1,20     | 1   | 1,44   | 43     | Cúpula de vidro laminado curvo Ø1,20 sobre anel; vidro interno plano; esquadria RPT calandrada | Cume principal, sobre a cama         |
| RE1  | Chaminé do Respiro                        | 0,70      | 0,70     | 1   | 0,49   | 15     | Tubo de alumínio Ø700 com veneziana motorizada e tela                                          | Cume secundário, sobre o café        |
| PC2  | Porta de correr do banho                  | 1,10      | 2,20     | 1   | 2,42   | 73     | Folha de madeira laminada, trilho superior                                                     | Parede da cabeceira, y +1,50 a +2,60 |

## REGRAS

Contramarcos de alumínio com ruptura térmica, anodizado bronze; furação e selagem só nos perfis, nunca na lona.

Vidro insulado low-e 6 lam + 12 Ar + 6 temp (fachadas); laminado 8 + 8 (claraboias, Espinha, lanterna); curvo laminado (Visor, Anel de Luz, lanterna); acidado nos banhos.

Cavaletes de vidro ≤ 2,2 x 2,4 m; panos numerados; calços de EPDM; silicone estrutural neutro; teste de água após a instalação.

Vidraceiro entrega: conferência de medidas na estrutura montada (lote 2 concluído) antes de cortar os vidros: tolerância ± 3 mm.

SEQUÊNCIA DE INSTALAÇÃO · LONA, ISOLAMENTO, FORRO E VIDROS

etapas do manual que pertencem a este lote · vento > 30 km/h suspende a lona

| ETAPA · EQUIPE · TEMPO                                                                                  | FERRAMENTAS E EQUIPAMENTOS   | RISCOS                                                                           | CHECKLIST   |
|---|---|----------------------------------------------------------------------------------|---|
| 08 <b>Instalação da membrana externa</b><br>2 instaladores de membrana + 2 montadores + líder · 1,5 dia | Puxadores de keder, cordas, esticadores, tensiômetro, ferro de solda portátil (reparos) · Andaime, guincho manual, cordas guia | Vento acima de 30 km/h: suspender; membrana arrastada em aresta: proteger cantos | <input type="checkbox"/> Membrana içada pelos anéis de cume e presa nos clamps<br><input type="checkbox"/> Cantos e estais tensionados em cruz, flecha das bordas ± 20 mm<br><input type="checkbox"/> Sem rugas; pré-tensão uniforme<br><input type="checkbox"/> Teste de água nos rodapés / bordas (15 min)                   |
| 09 <b>Instalação do isolamento</b><br>3 montadores · 1 dia                                              | Estilete, grampeador, arame, tesoura · Escada                                                                                  | Isolamento comprimido perde R; manta úmida: instalar com a membrana já fechada   | <input type="checkbox"/> Mantas PET presas à malha das terças (ou cabos do forro), sem vazios<br><input type="checkbox"/> Refletiva com face refletiva para a câmara<br><input type="checkbox"/> Fitas nas emendas<br><input type="checkbox"/> Passagens de eletrodutos previstas                                              |
| 10 <b>Instalação da membrana interna (forro tensionado)</b><br>2 instaladores + 1 montador · 1 dia      | Espátulas de harpão, soprador térmico, nível · Escada                                                                          | Forro tensionado antes das instalações elétricas: coordenar caixas e luminárias  | <input type="checkbox"/> Trilhos harpão fixados nos talões / cabos<br><input type="checkbox"/> 6 painéis seguindo os cumes, anéis internos fixados<br><input type="checkbox"/> Aberturas de difusores e luminárias recortadas com anel                                                                                         |
| 11 <b>Instalação das portas e vidros</b><br>Vidraceiro + 2 auxiliares · 2 dias                          | Ventosas, calços, nível, silicone estrutural, pistola · Cavaletes de vidro, carrinho de ventosa                                | Vidro de 90 kg (fachada): mínimo 3 pessoas ou içador a vácuo                     | <input type="checkbox"/> Anel de alumínio E07 sobre EPDM (Casulo) / contramarcos (Safari) no prumo<br><input type="checkbox"/> Vidros calçados e selados; porta pivotante ajustada<br><input type="checkbox"/> Janelas Olho com selante PU curado 24 h<br><input type="checkbox"/> Vidros da espinha / óculo com teste de água |

RFQ · PEDIDO DE COTAÇÃO DO LOTE 3

ZION SAFARI · o que a Zion envia, o que o fornecedor devolve, critérios de aceite · <span class="cotar">PREÇO A COTAR</span>

A ZION ENVIA

- |    |                                                                                                |
|----|------------------------------------------------------------------------------------------------|
| 1. | Este documento (quadro de painéis, materiais, fixações LN-90, quadro de esquadrias)            |
| 2. | Padrões de corte: ZS-LON-001_padroes.dxf e ZS-LON-001_coordenadas.xlsx; pranchas LN-01 a LN-90 |
| 3. | Modelo 3D (GLB) e malha da superfície para form-finding                                        |
| 4. | Detalhes DET-01 / DET-02 / DET-05                                                              |

O FORNECEDOR DEVOLVE

- |    |   |
|----|---|
| 1. | Cotação da lona externa (m2 confeccionado, por painel) e do forro; perfis e cabos por metro; instalação por dia de equipe |
| 2. | Padronagem proposta (rolos, emendas) e compensação adotada (laudo biaxial do tecido)                                      |
| 3. | Cotação dos vidros por pano (m2) e das esquadrias (un.), com prazo de medição em obra                                     |
| 4. | Amostra do tecido e do vidro; ficha técnica e garantia                                                                    |

CRITÉRIOS DE ACEITE E GARANTIA

- |   |
|---|
| Lona: sem rugas após tensionamento, pré-tensão de projeto medida, teste de água 15 min sem infiltração |
| Solda HF: ensaio de tração da emenda ≥ 80 % do tecido                                                  |
| Vidros: sem trincas, calços e selantes conforme, teste de água                                         |
| Garantia: lona 10 anos (PVDF) · forro 5 anos · vidros 5 anos (insulado)                                |

CONDIÇÕES GERAIS

- |   |
|---|
| Cotação por item e total, com prazo de fabricação e validade; impostos destacados; frete até o ponto de transbordo indicado. |
| Amostras / protótipo de nó antes da série (quando indicado); inspeção da Zion em fábrica antes da expedição.                 |
| Etiquetagem e embalagem conforme o pacote de transporte deste lote; lista de volumes assinada.                               |
| Sem alteração de material ou bitola sem aprovação escrita da Zion e do engenheiro responsável (ART).                         |
| Preços permanecem em documento interno da Zion; este documento circula sem preços.                                           |